


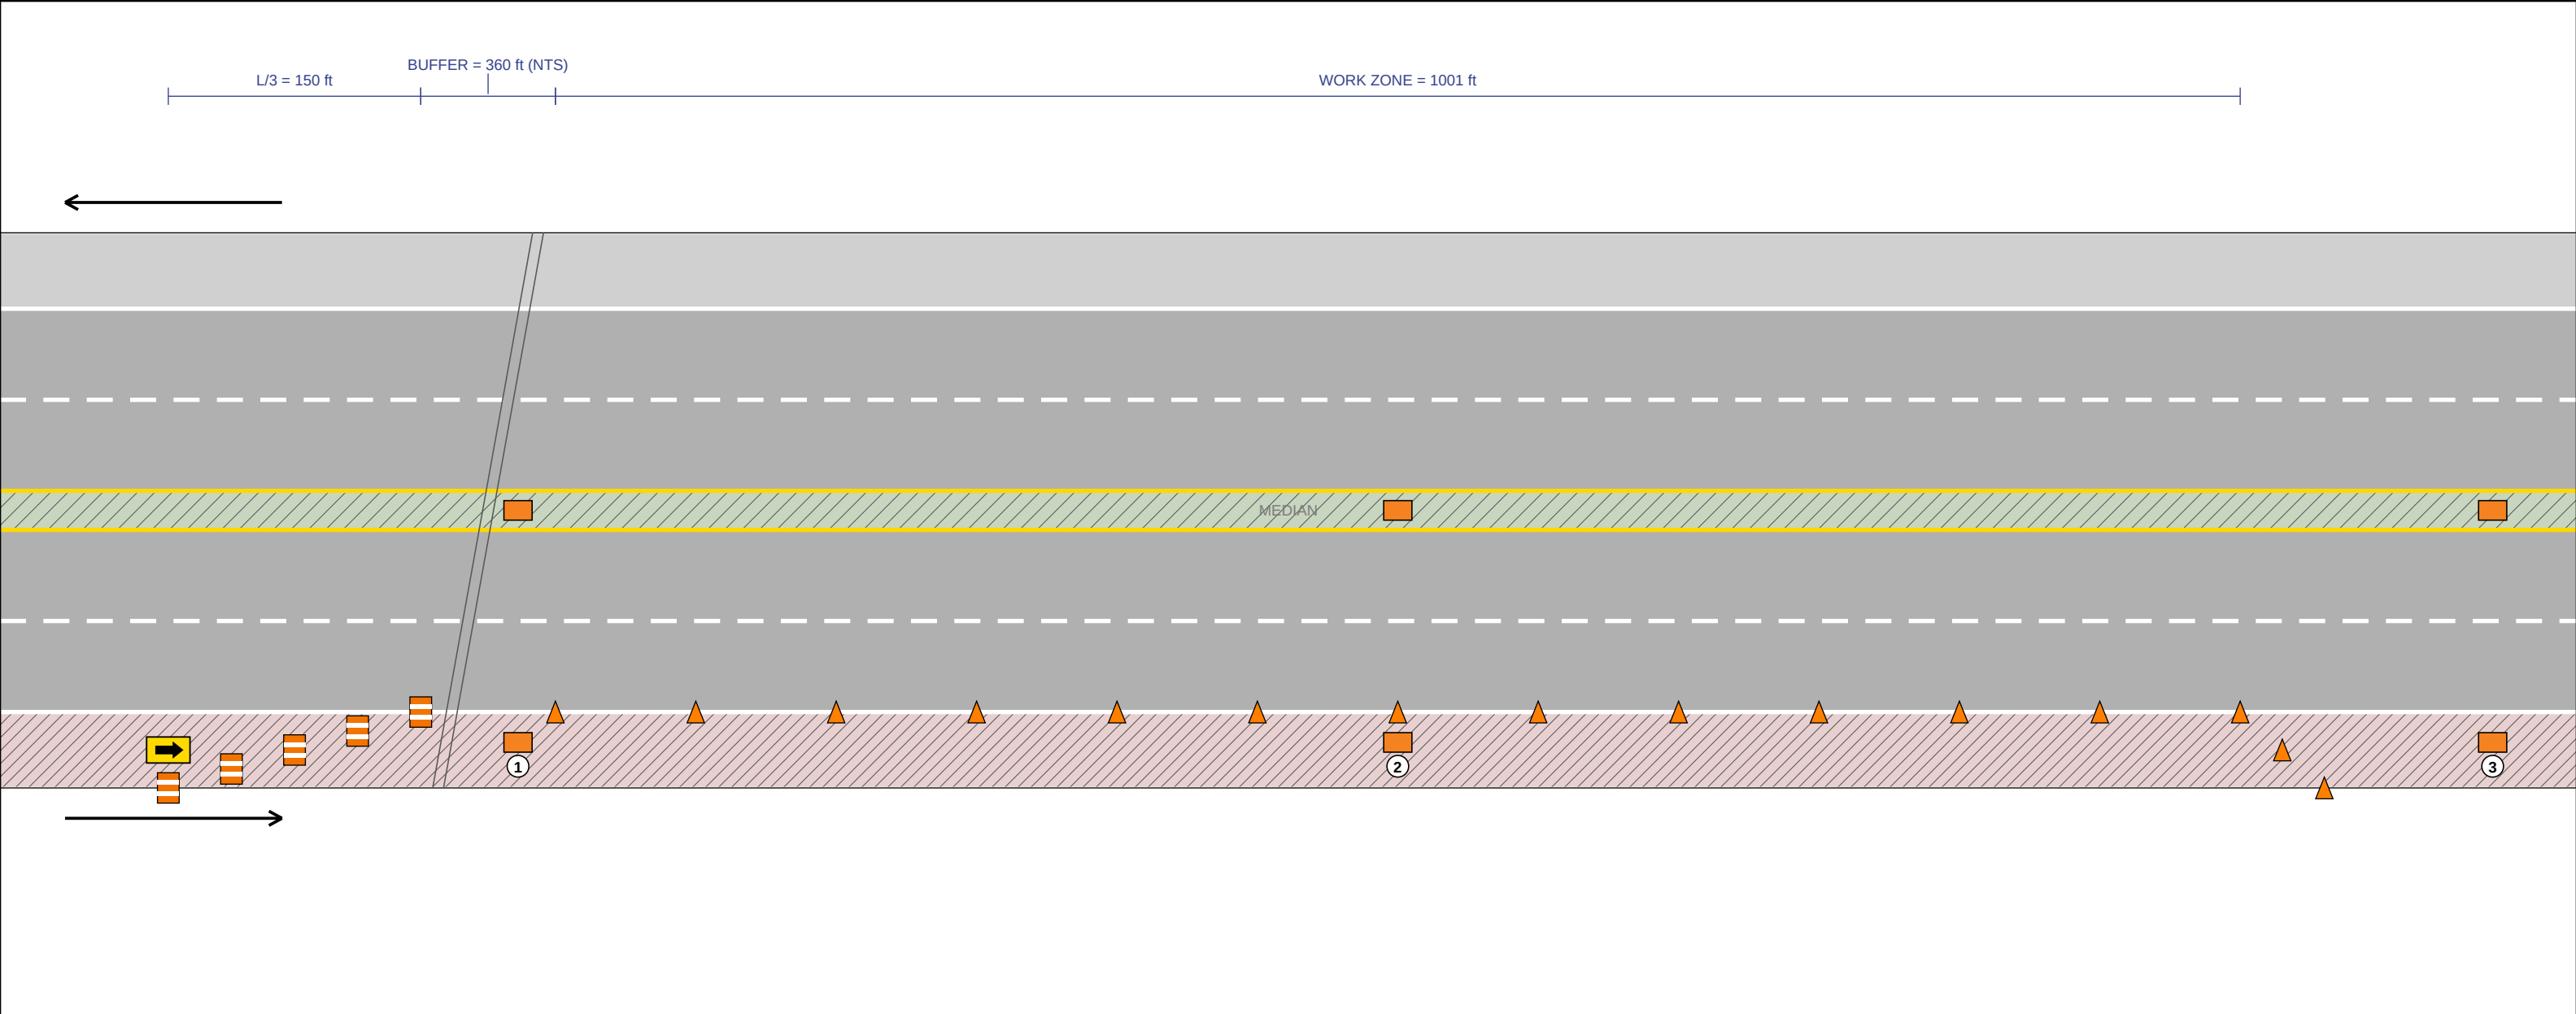

LEGEND

- Arrow Board
- Traffic Cone (36-inch)
- Channelizing Drum
- Warning sign (W series, e.g. W20-1)
- Construction guide (G series, e.g. G20-2)

ROAD GEOMETRY

Median (separates carriageways)

Left-side advance signs sit in the median per S-630-1 Sheet 2 General Note 8.

Scale 1" = 93 ft applies to the work zone + taper. Buffer compressed; lateral offset exaggerated.

NOTES & SIGN SCHEDULE

PARAMETERS			
Speed limit:	45 mph	Closure:	Shoulder Closure
Work zone:	1001 ft	Shoulder taper (L/3):	150 ft
Buffer:	360 ft		

SIGN SCHEDULE		
#	CODE	DESCRIPTION
1	G20-1	ROAD CONSTRUCTION (NEXT 1001 FT)
2	G20-5P	CONSTRUCTION ZONE plaque
3	G20-2	END ROAD WORK

ADVANCE WARNING SIGNS (off-page upstream of taper)		
CODE	DESCRIPTION	DISTANCE
W21-5aR	RIGHT SHOULDER CLOSED AHEAD	350 ft
W20-2	ROAD WORK 700 FT	700 ft
W20-1	ROAD WORK AHEAD	1050 ft

Reference: CDOT S-630-1, MUTCD 11th Ed. Part 6 (effective 2026-01-18), Colorado Supplement.
SITE CONDITIONS NOT CHECKED — service unavailable at generation.
GENERATED BY CONESTRUCT — DRAFT FOR PE REVIEW. NOT A SEALED PLAN.
Verify all dimensions before use.


TRAFFIC CONTROL DEVICE SUMMARY

MUTCD	DEVICE	QTY
G20-1	ROAD CONSTRUCTION (NEXT 1001 FT)	2
G20-2	END ROAD WORK	2
G20-5P	CONSTRUCTION ZONE plaque	2
W20-1	ROAD WORK AHEAD	2
W20-2	ROAD WORK 700 FT	2
W21-5aR	RIGHT SHOULDER CLOSED AHEAD	2
—	36-inch channelizing drum with alternating orange/white stripes	5
—	Traffic Cone (36-inch)	15
—	Trailer-mounted flashing arrow board (Type A, B, or C)	1

TOTAL DEVICES 33
SEE DEVICE LIST (XLSX) FOR BID QUANTITIES.

PROJECT:	s2a17 live check
LOCATION:	—
COORDINATES:	39.71130, -105.08150
MHT TYPE:	SHOULDER CLOSURE — DIVIDED HIGHWAY
MUTCD:	TA-3
CDOT:	S-630-1
SCALE:	1" = 93 ft
DATE:	2026-09-03
SHEET:	1 OF 2
AERIAL:	See page 2
DRAWN BY:	MHT Tool (auto-generated)
STATUS:	DRAFT — Not for stamping

AERIAL CONTEXT

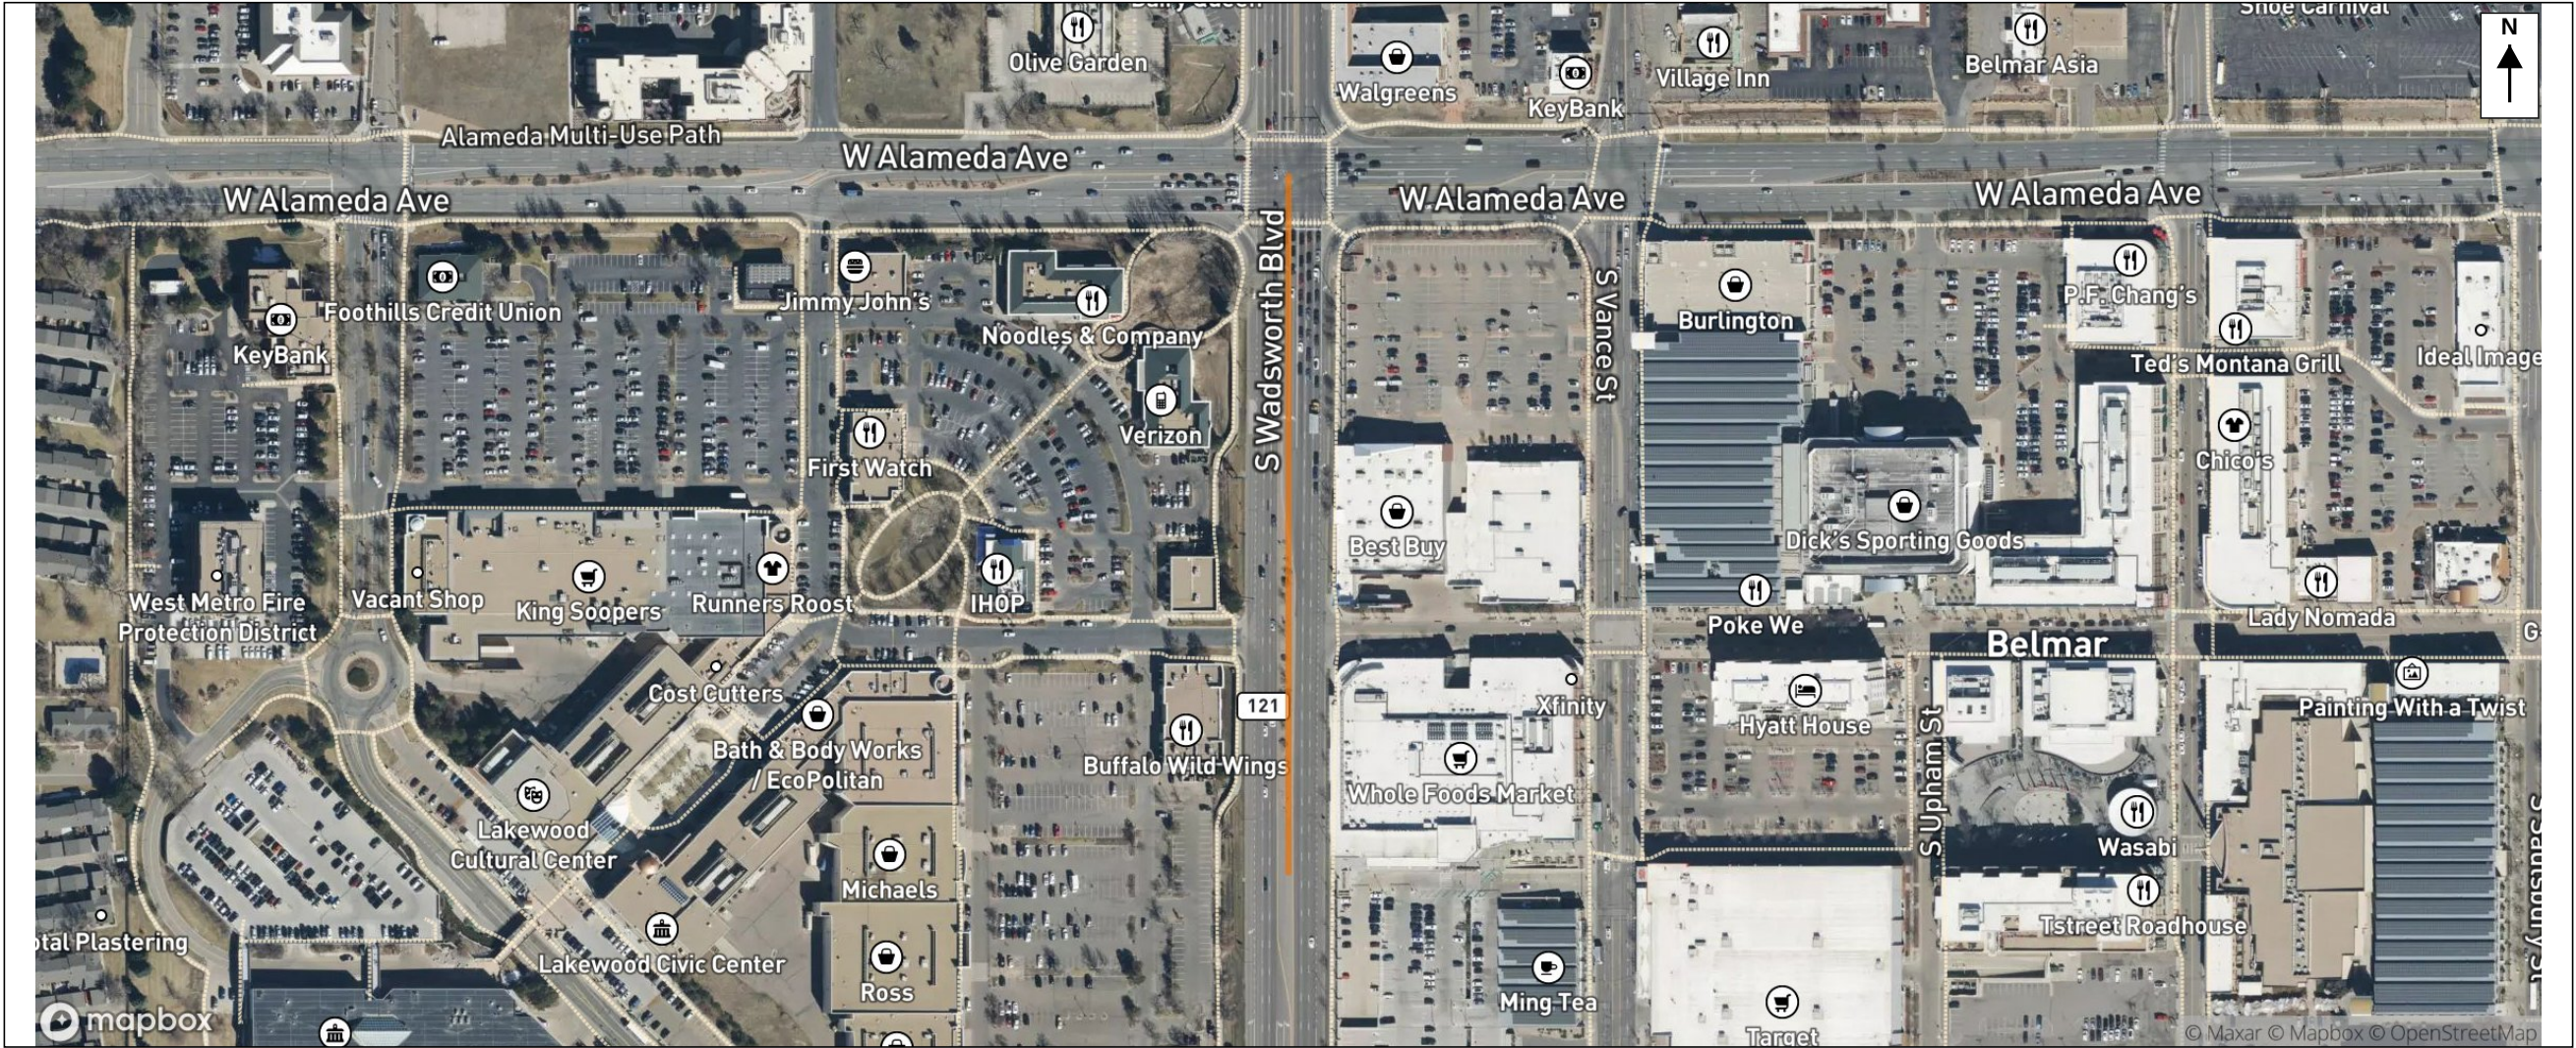

SITE: 39.71130, -105.08150

Work zone (1,001 ft) shown in orange. Advance warning, taper, and buffer not depicted. Mapbox satellite imagery with street labels — for context only. Not a survey product. Verify all field conditions on site.

CORRIDOR DETAILS

Anchor:	39.71130, -105.08150
Bearing:	180°
Total corridor:	2,661 ft (0.50 mi)
Advance warning:	1,050 ft
Taper:	150 ft
Buffer:	360 ft
Work zone:	1,001 ft
Downstream:	100 ft