
METHOD OF HANDLING TRAFFIC · 30 MPH

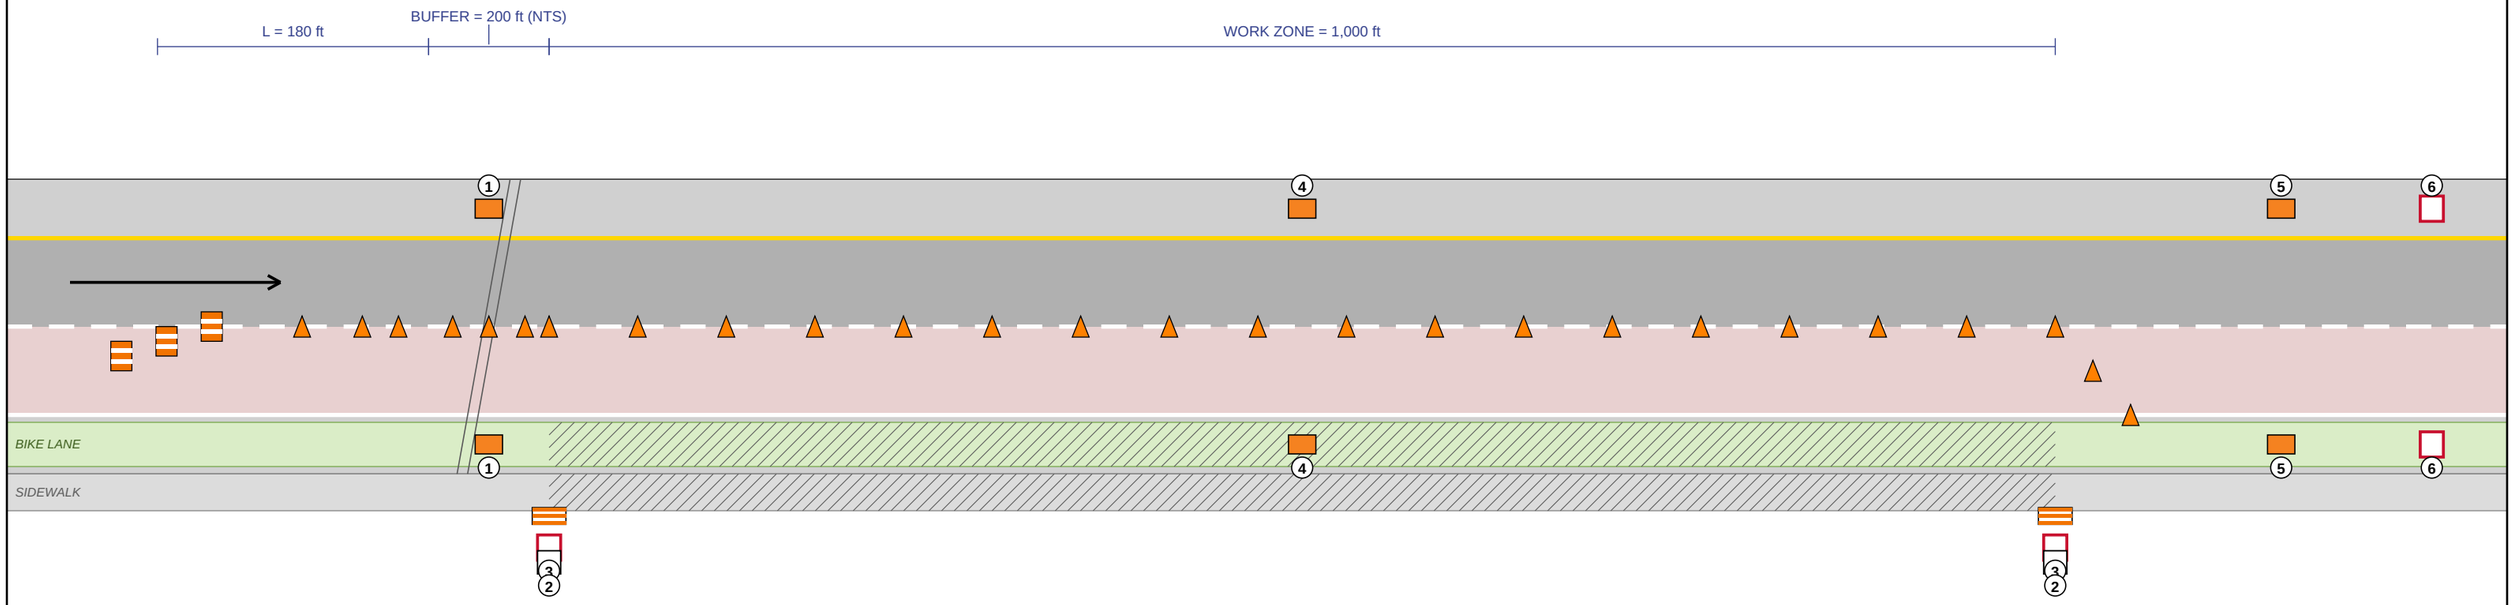

LEGEND

- Arrow Board
- Type III Barricade
- Traffic Cone (28-inch)
- Channelizing Drum

SIGN CATEGORIES

- Warning sign (W series, e.g. W20-1)
- Construction guide (G series, e.g. G20-2)
- Regulatory sign (R series, e.g. R9-9)
- Route guidance (M series, e.g. M4-9a)

+2 MORE. SEE DEVICE LIST (XLSX)

Scale 1" = 101 ft applies to the work zone + taper. Buffer compressed; lateral offset exaggerated.

NOTES & SIGN SCHEDULE

PARAMETERS

Speed limit:	**30 mph**	Closure:	**Lane Closure Near Intersection**
Work zone:	**1,000 ft**	Lane taper (L):	**180 ft**
Buffer:	**200 ft**		

SIGN SCHEDULE

#	CODE	DESCRIPTION
1	**G20-1**	ROAD CONSTRUCTION (NEXT 1000 FT)
2	**M4-9a**	BIKE DETOUR
3	**R9-9**	SIDEWALK CLOSED
4	**G20-5P**	WORK ZONE plaque
5	**G20-2**	END ROAD WORK
6	**R2-11**	END DOUBLE FINES ZONE

ADVANCE WARNING SIGNS (off-page upstream of taper)

CODE	DESCRIPTION	DISTANCE
W4-2R	RIGHT LANE ENDS	244 ft

+3 MORE ADVANCE SIGNS (W20-5R, R2-10, W20-1). SEE CREW NARRATIVE & DEVICE LIST

CROSS-STREET CONTROL PER CDOT S-630-1 SHEET 10, CASES 18/19: NOT DRAWN. PLATE DEPARTURES: SEE AUDIT. SEE DEVICE LIST, CREW NARRATIVE, AND AUDIT.
CLOSED LANE DRAWN AS THE RIGHTMOST LANE: A MODELING ASSUMPTION; NO MUTCD RULE SELECTS THE LANE (THE WORK LOCATION DOES). IF THE WORK OCCUPIES A DIFFERENT LANE, THIS PLAN DOES NOT APPLY AS DRAWN.

TRAFFIC CONTROL DEVICE SUMMARY

MUTCD	DEVICE	QTY
G20-1	ROAD CONSTRUCTION (NEXT 1000 FT)	2
G20-2	END ROAD WORK	2
G20-5P	WORK ZONE plaque	2
M4-9a	BIKE DETOUR	2
R2-10	BEGIN DOUBLE FINES ZONE	4
R2-11	END DOUBLE FINES ZONE	4
R9-9	SIDEWALK CLOSED	2
W20-1	ROAD WORK AHEAD	4
W20-5R	RIGHT LANE CLOSED AHEAD	2
W4-2R	RIGHT LANE ENDS	2
—	36-inch channelizing drum with alternating orange/white stripes	7
—	Traffic Cone (28-inch)	26
—	Type III barricade: three horizontal striped rails, full lane width	2
—	Trailer-mounted flashing arrow board (Type A, B, or C)	1
TOTAL DEVICES		**62**


SEE DEVICE LIST (XLSX) FOR BID QUANTITIES.

PROJECT:	Untitled Project
LOCATION:	1550 E Colfax Ave, Denver
COORDINATES:	39.73997, -104.96928
MHT TYPE:	LANE CLOSURE NEAR INTERSECTION · ONE-WAY STREET
MUTCD:	TA-22
CDOT:	S-630-1
SCALE:	1" = 101 ft
DATE:	2026-11-04
SHEET:	1 OF 2
AERIAL:	See page 2
DRAWN BY:	MHT Tool (auto-generated)
STATUS:	**DRAFT: Not for stamping**

Reference: CDOT S-630-1, MUTCD 11th Edition Part 6, Colorado Supplement (effective January 18, 2026).
GENERATED BY CONESTRUCT. DRAFT FOR PE REVIEW. NOT A SEALED PLAN.
Verify all dimensions before use.

METHOD OF HANDLING TRAFFIC · 30 MPH

AERIAL CONTEXT

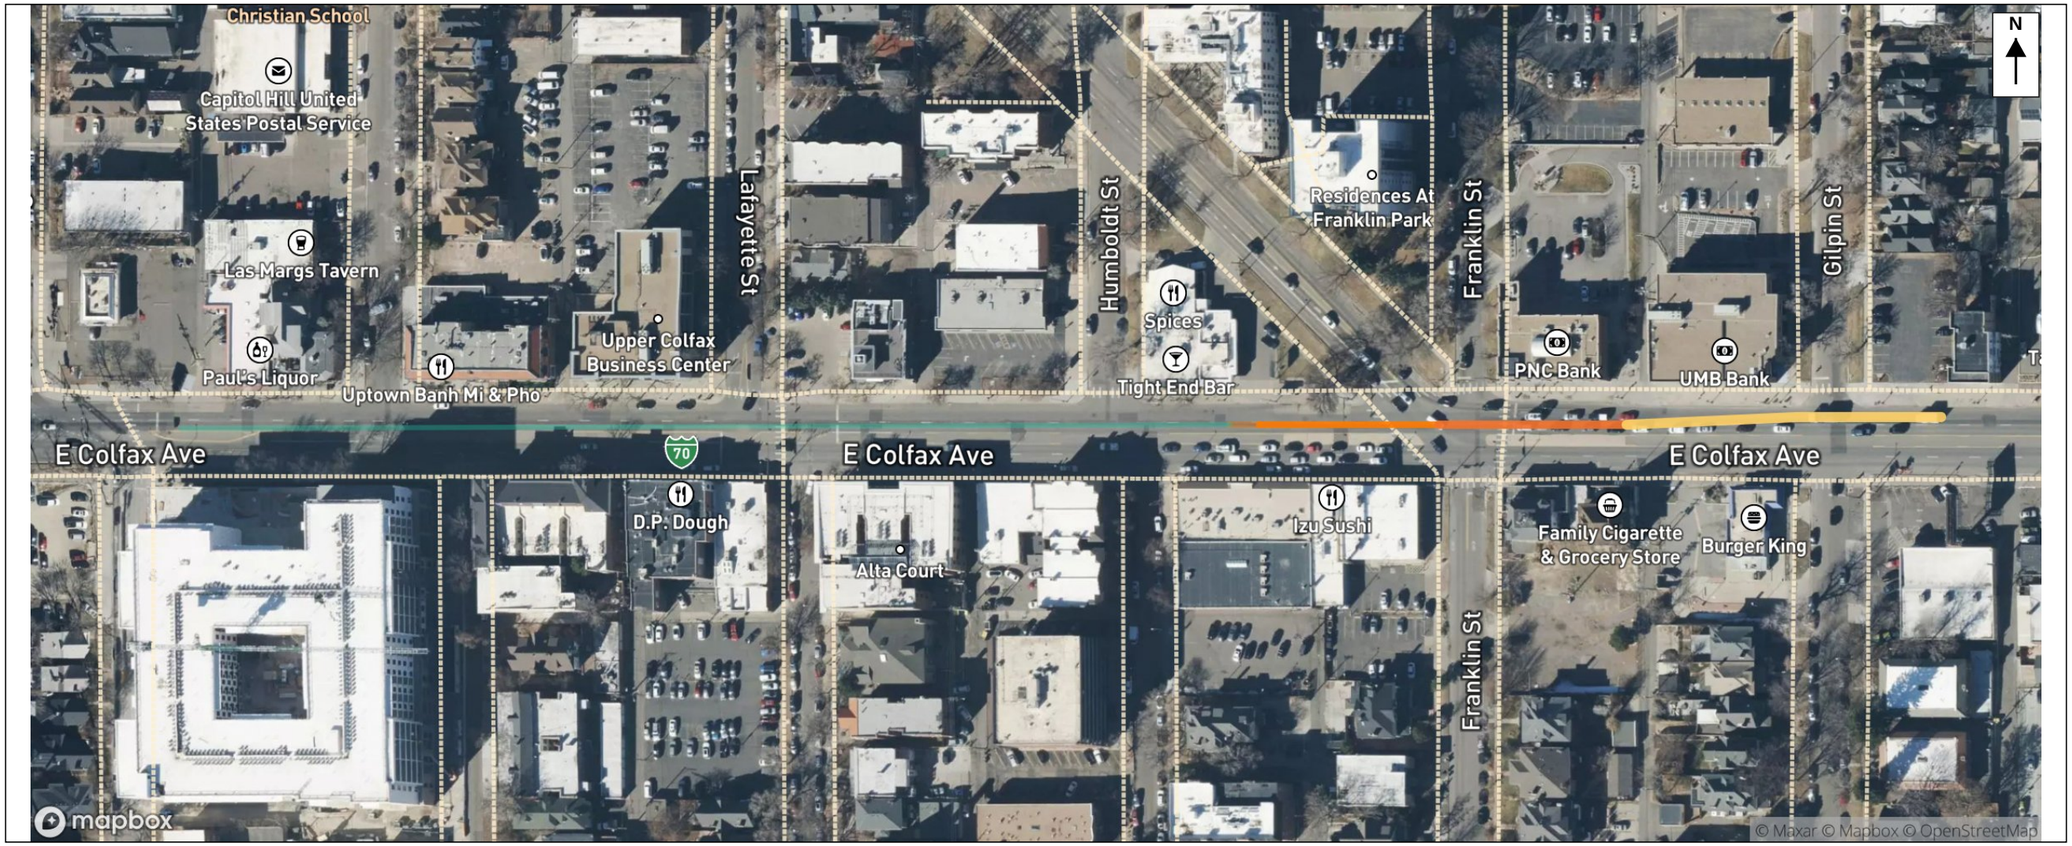

SITE: 1550 E Colfax Ave, Denver

39.73997, -104.96928

Advance warning · Taper · Buffer · Work zone · Downstream · faded: past the mapped road

Mapbox satellite imagery with street labels, for context only. Not a survey product. Verify all field conditions on site.

CORRIDOR DETAILS

Work starts:	39.73997, -104.96928
Direction of travel:	270°
Total corridor:	1,730 ft (0.33 mi)
Advance warning:	300 ft
Taper:	180 ft
Buffer:	200 ft
Work zone:	1,000 ft
Downstream:	50 ft
Centerline:	covers 1,080–1,730 ft, bearing beyond