


METHOD OF HANDLING TRAFFIC — 40 MPH

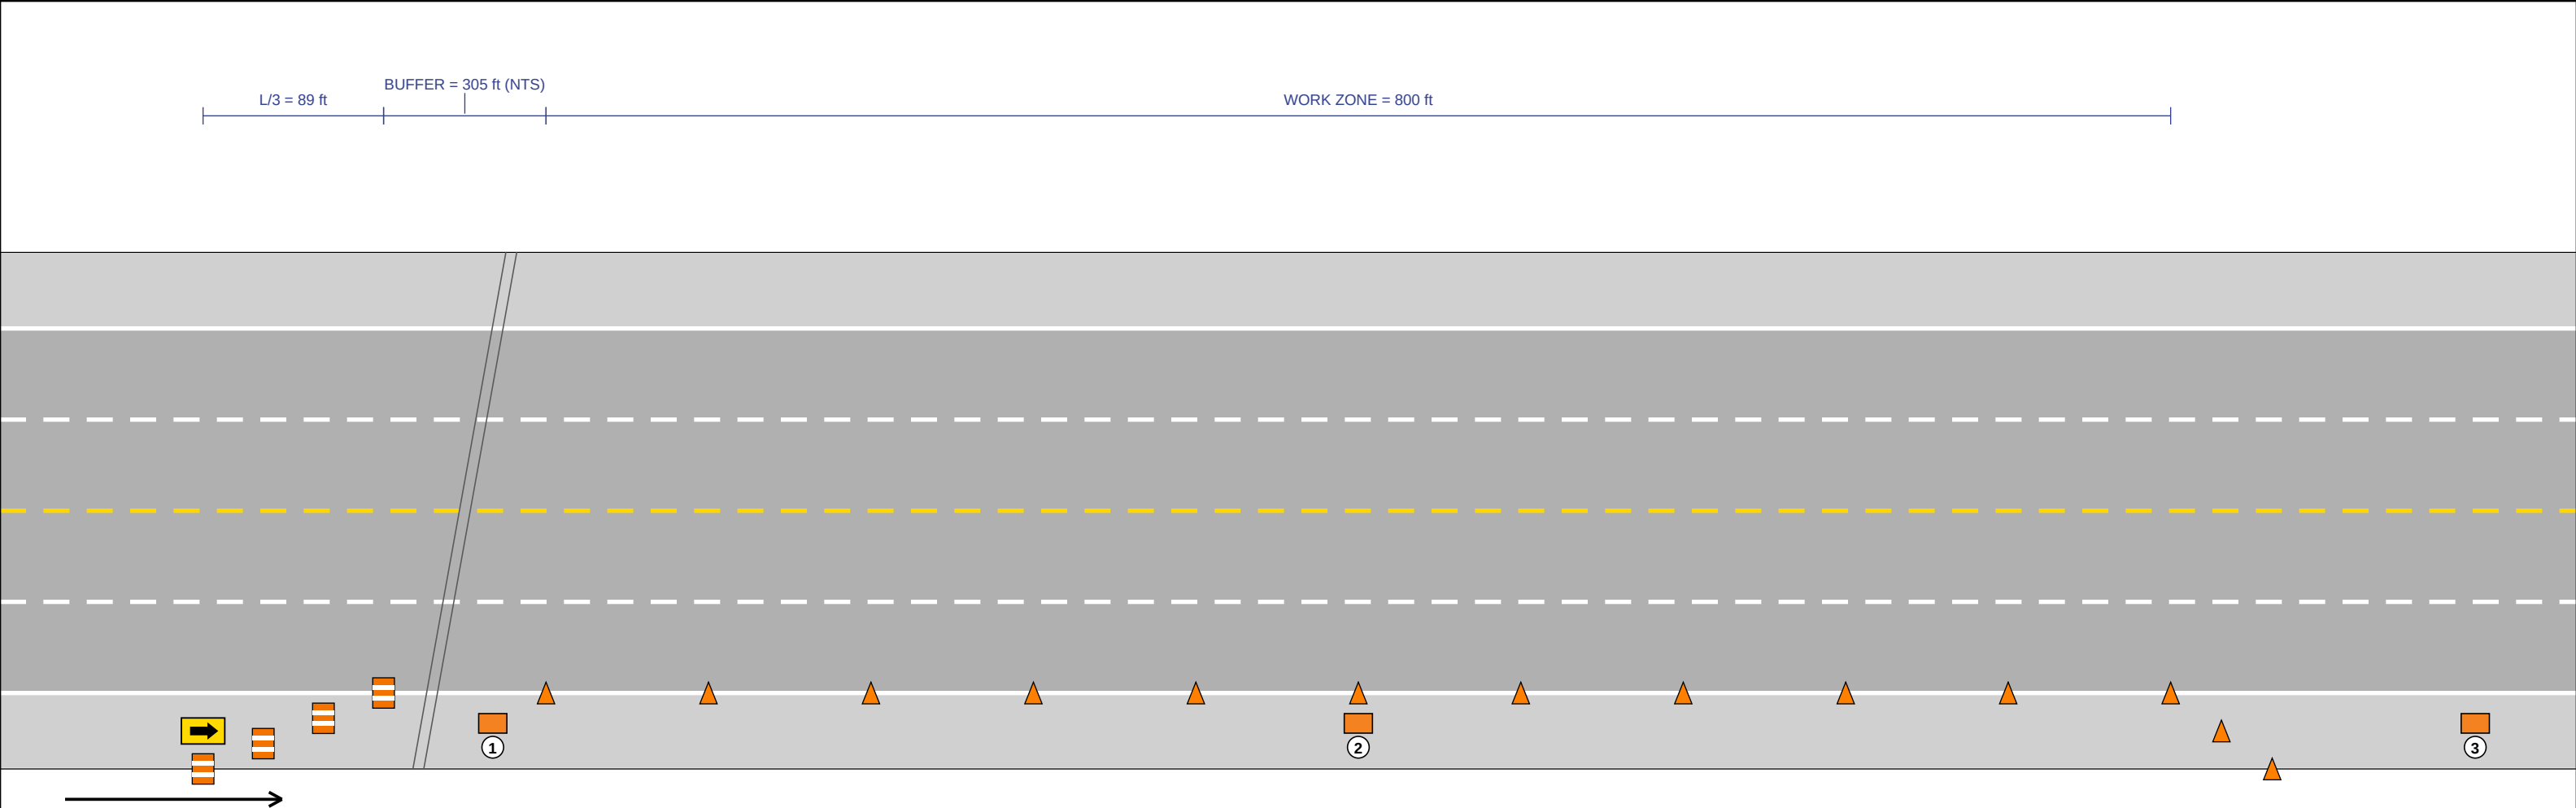

LEGEND

- Arrow Board
- Traffic Cone (28-inch)
- Channelizing Drum
- Warning sign (W series, e.g. W20-1)
- Construction guide (G series, e.g. G20-2)

SIGN CATEGORIES

NOTES & SIGN SCHEDULE

PARAMETERS			
Speed limit:	40 mph	Closure:	Shoulder Closure
Work zone:	800 ft	Shoulder taper (L/3):	89 ft
Buffer:	305 ft		
SIGN SCHEDULE			
#	CODE	DESCRIPTION	
1	G20-1	ROAD CONSTRUCTION (NEXT 800 FT)	
2	G20-5P	CONSTRUCTION ZONE plaque	
3	G20-2	END ROAD WORK	
ADVANCE WARNING SIGNS (off-page upstream of taper)			
CODE	DESCRIPTION	DISTANCE	
W21-5aR	RIGHT SHOULDER CLOSED AHEAD	350 ft	
W20-2	ROAD WORK 700 FT	700 ft	
W20-1	ROAD WORK AHEAD	1050 ft	

Reference: CDOT S-630-1, MUTCD 11th Ed. Part 6 (effective 2026-01-18), Colorado Supplement.
GENERATED BY CONESTRUCT — DRAFT FOR PE REVIEW. NOT A SEALED PLAN.
Verify all dimensions before use.

TRAFFIC CONTROL DEVICE SUMMARY

MUTCD	DEVICE	QTY
G20-1	ROAD CONSTRUCTION (NEXT 800 FT)	1
G20-2	END ROAD WORK	1
G20-5P	CONSTRUCTION ZONE plaque	1
W20-1	ROAD WORK AHEAD	1
W20-2	ROAD WORK 700 FT	1
W21-5aR	RIGHT SHOULDER CLOSED AHEAD	1
—	36-inch channelizing drum with alternating orange/white stripes	4
—	Traffic Cone (28-inch)	13
—	Trailer-mounted flashing arrow board (Type A, B, or C)	1

TOTAL DEVICES 24
SEE DEVICE LIST (XLSX) FOR BID QUANTITIES.

PROJECT:	Untitled Project
LOCATION:	Lookout Mountain Road, Golden, CO
COORDINATES:	39.74231, -105.23925
MHT TYPE:	SHOULDER CLOSURE — 4-LANE UNDIVIDED
MUTCD:	TA-3
CDOT:	S-630-1
SCALE:	1" = 77 ft
DATE:	2026-08-03
SHEET:	1 OF 2
AERIAL:	See page 2
DRAWN BY:	MHT Tool (auto-generated)
STATUS:	DRAFT — Not for stamping

AERIAL CONTEXT



SITE: Lookout Mountain Road, Golden, CO

39.74231, -105.23925

Work zone (800 ft) shown in orange. Advance warning, taper, and buffer not depicted. Mapbox satellite imagery with street labels — for context only. Not a survey product. Verify all field conditions on site.

CORRIDOR DETAILS

Anchor:	39.74231, -105.23925
Bearing:	156°
Total corridor:	2,344 ft (0.44 mi)
Advance warning:	1,050 ft
Taper:	89 ft
Buffer:	305 ft
Work zone:	800 ft
Downstream:	100 ft
Centerline:	OSM, full corridor