


METHOD OF HANDLING TRAFFIC — 30 MPH

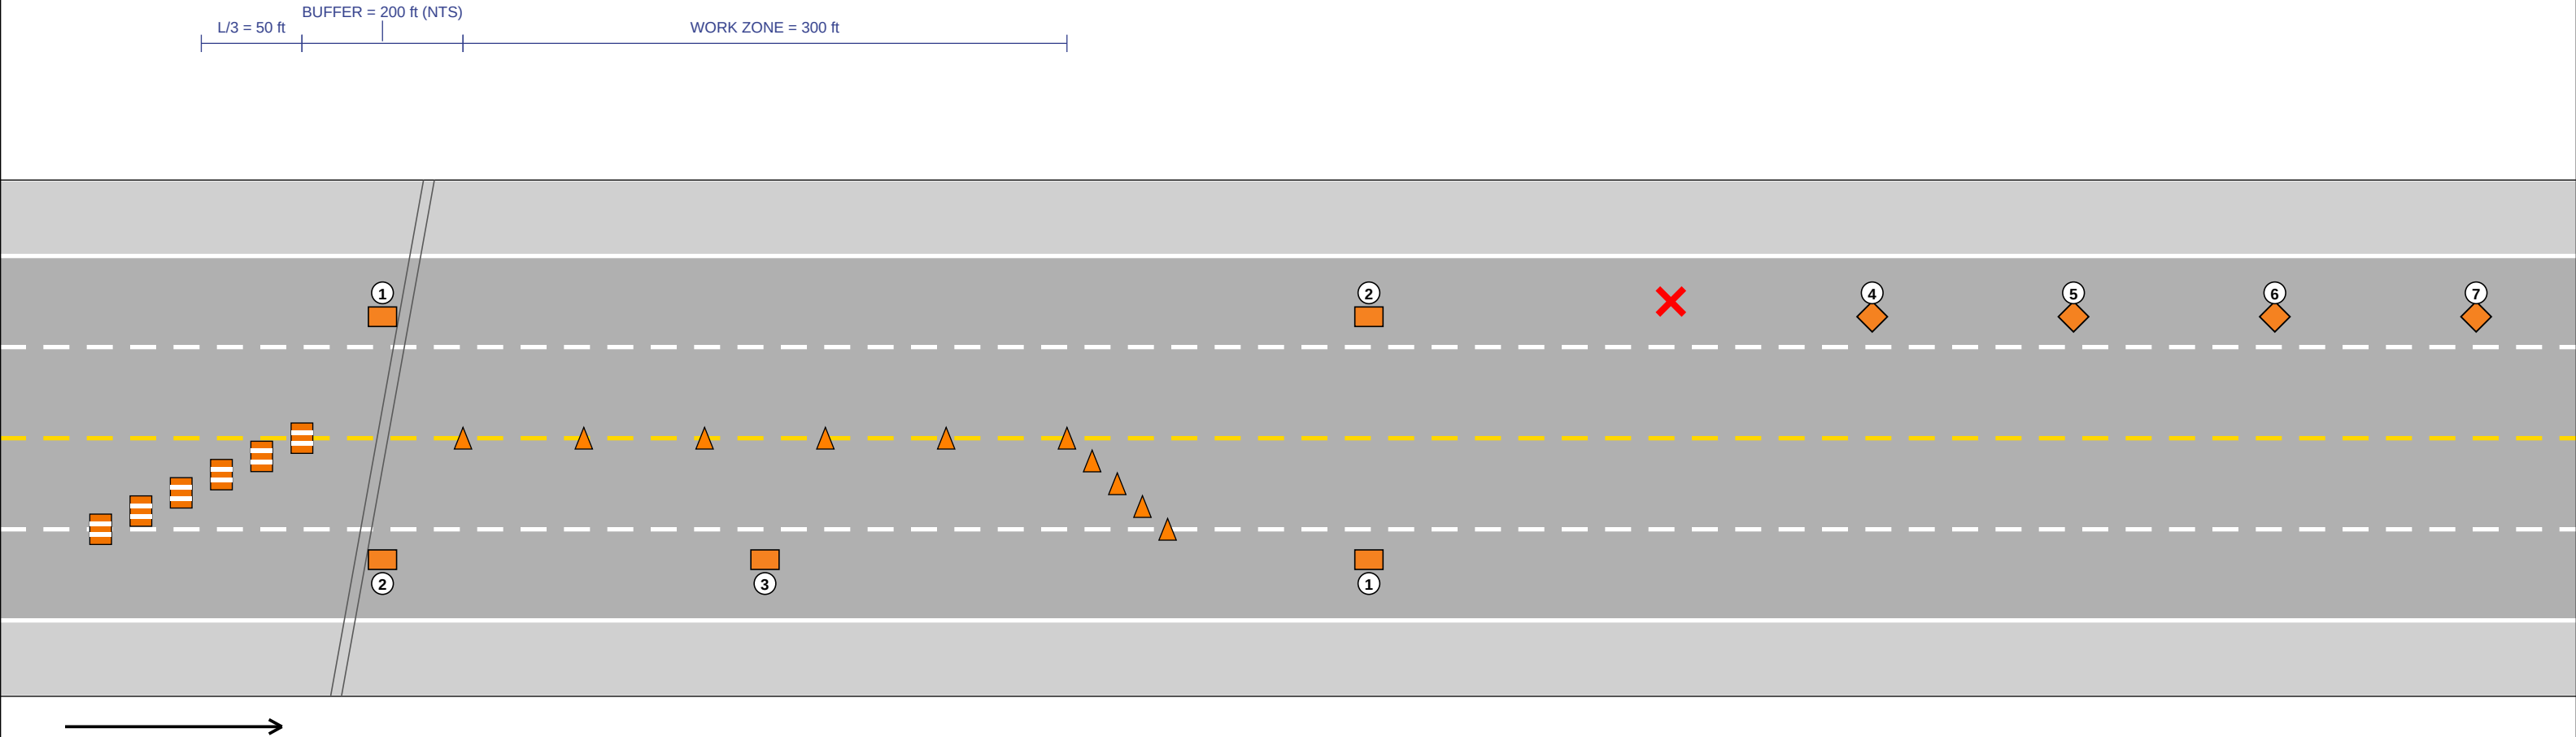

LEGEND

- Traffic Cone (28-inch)
- Channelizing Drum
- Flagger Station

SIGN CATEGORIES

- Warning sign (W series, e.g. W20-1)
- Construction guide (G series, e.g. G20-2)

NOTES & SIGN SCHEDULE

PARAMETERS			
Speed limit:	30 mph	Closure:	Shoulder Closure
Work zone:	300 ft	Shoulder taper (L/3):	50 ft
Buffer:	200 ft		

SIGN SCHEDULE		
#	CODE	DESCRIPTION
1	G20-2	END ROAD WORK
2	G20-1	ROAD CONSTRUCTION (NEXT 300 FT)
3	G20-5P	CONSTRUCTION ZONE plaque
4	W20-7	FLAGGER AHEAD
5	W3-4	BE PREPARED TO STOP
6	W20-4	ONE LANE ROAD AHEAD
7	W20-1	ROAD WORK AHEAD

ADVANCE WARNING SIGNS & FLAGGER STATIONS (off-page upstream of taper)					
CODE	DESCRIPTION	DISTANCE	CODE	DESCRIPTION	DISTANCE
—	FLAGGER STATION #1 (APPROACH)	150 ft	W20-4	ONE LANE ROAD AHEAD	450 ft
W20-7	FLAGGER AHEAD	250 ft	W20-1	ROAD WORK AHEAD	550 ft
W3-4	BE PREPARED TO STOP	350 ft			

Reference: CDOT S-630-1, MUTCD 11th Ed. Part 6 (effective 2026-01-18), Colorado Supplement.
GENERATED BY CONESTRUCT — DRAFT FOR PE REVIEW. NOT A SEALED PLAN.
Verify all dimensions before use.

TRAFFIC CONTROL DEVICE SUMMARY

MUTCD	DEVICE	QTY
G20-1	ROAD CONSTRUCTION (NEXT 300 FT)	2
G20-2	END ROAD WORK	2
G20-5P	CONSTRUCTION ZONE plaque	1
W20-1	ROAD WORK AHEAD	2
W20-4	ONE LANE ROAD AHEAD	2
W20-7	FLAGGER AHEAD	2
W3-4	BE PREPARED TO STOP	2
—	36-inch channelizing drum with alternating orange/white stripes	6
—	Traffic Cone (28-inch)	10
—	Flagger position with STOP/SLOW paddle and PPE	2

TOTAL DEVICES 31

SEE DEVICE LIST (XLSX) FOR BID QUANTITIES.

PROJECT:	Untitled Project
LOCATION:	23rd ave, greeley, co
COORDINATES:	39.73890, -104.98620

MHT TYPE:	SHOULDER CLOSURE — 4-LANE UNDIVIDED
MUTCD:	—
CDOT:	—

SCALE:	1" = 78 ft
DATE:	2026-08-03
SHEET:	1 OF 2
AERIAL:	See page 2

DRAWN BY:	MHT Tool (auto-generated)
STATUS:	DRAFT — Not for stamping

AERIAL CONTEXT



SITE: 23rd ave, greeley, co
39.73890, -104.98620

Work zone (300 ft) shown in orange. Advance warning, taper, and buffer not depicted. Mapbox satellite imagery with street labels — for context only. Not a survey product. Verify all field conditions on site.

CORRIDOR DETAILS

Anchor:	39.73890, -104.98620
Bearing:	0°
Total corridor:	1,000 ft (0.19 mi)
Advance warning:	300 ft
Taper:	100 ft
Buffer:	200 ft
Work zone:	300 ft
Downstream:	100 ft