METHOD OF HANDLING TRAFFIC · #312 Colorado Blvd at E Exposition Ave · 35 MPH

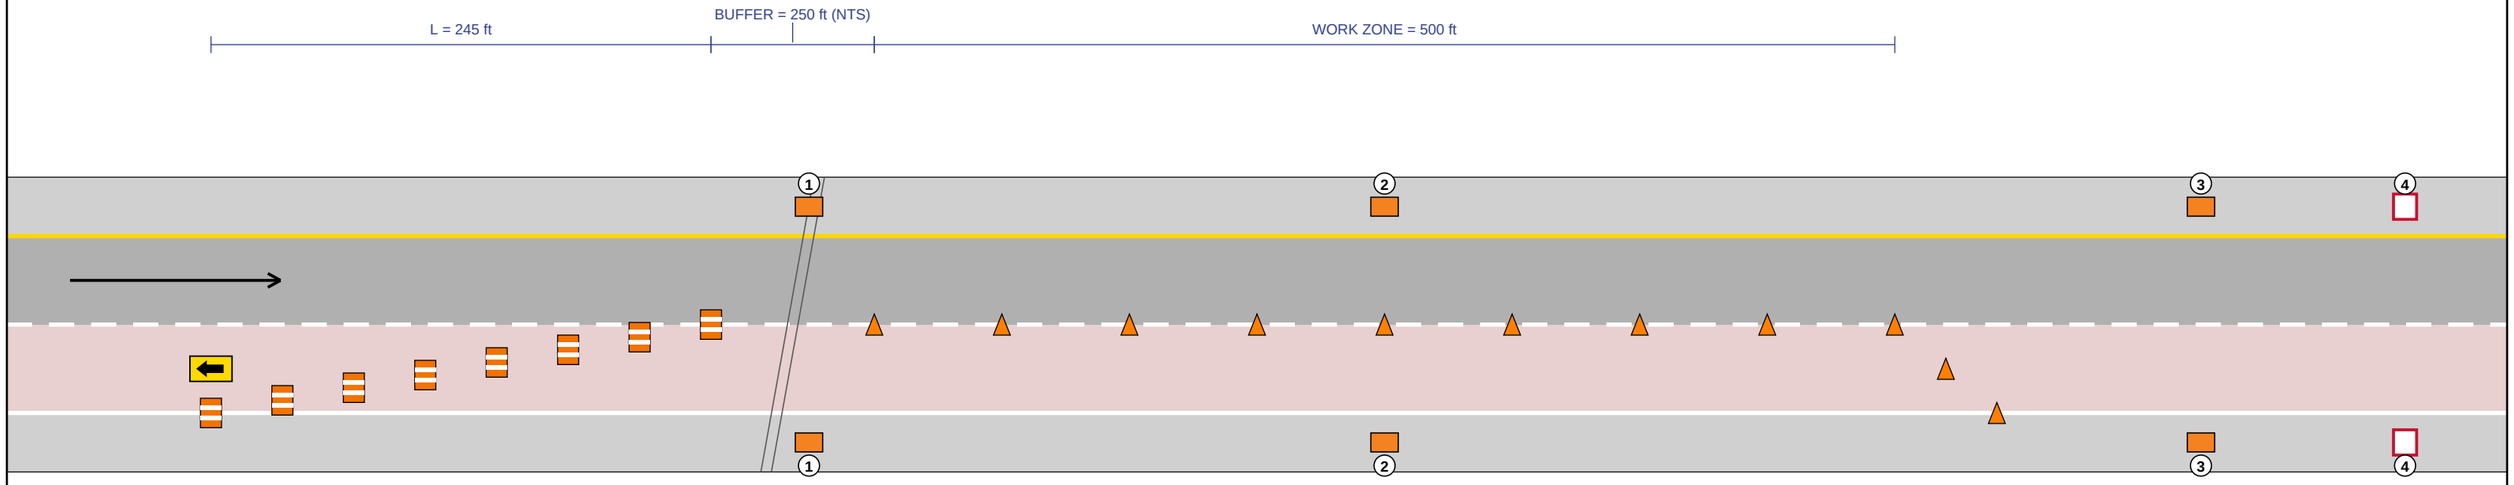

LEGEND

- Arrow Board
- Traffic Cone (28-inch)
- Channelizing Drum

SIGN CATEGORIES

- Warning sign (W series, e.g. W20-1)
- Construction guide (G series, e.g. G20-2)
- Regulatory sign (R series, e.g. R9-9)

Scale 1" = 74 ft applies to the work zone + taper. Buffer compressed; lateral offset exaggerated.

NOTES & SIGN SCHEDULE

PARAMETERS

Speed limit:	**35 mph**	Closure:	**Lane Closure Near Intersection**
Work zone:	**500 ft**	Lane taper (L):	**245 ft**
Buffer:	**250 ft**		

SIGN SCHEDULE

#	CODE	DESCRIPTION
1	**G20-1**	ROAD CONSTRUCTION (NEXT 500 FT)
2	**G20-5P**	CONSTRUCTION ZONE plaque
3	**G20-2**	END ROAD WORK
4	**R2-11**	END DOUBLE FINES ZONE

4 ADVANCE SIGNS OFF-PAGE (W4-2R, W20-5R, R2-10, W20-1). SEE CREW NARRATIVE & DEVICE LIST

Reference: CDOT S-630-1, MUTCD 11th Ed. Part 6 (effective 2026-01-18), Colorado Supplement.

CROSS-STREET CONTROL PER CDOT S-630-1 SHEET 10, CASES 18/19: NOT DRAWN. PLATE DEPARTURES: SEE AUDIT. SEE DEVICE LIST, CREW NARRATIVE, AND AUDIT.

CLOSED LANE DRAWN AS THE RIGHTMOST LANE: A MODELING ASSUMPTION; NO MUTCD RULE SELECTS THE LANE (THE WORK LOCATION DOES). IF THE WORK OCCUPIES A DIFFERENT LANE, THIS PLAN DOES NOT APPLY AS DRAWN.

GENERATED BY CONESTRUCT. DRAFT FOR PE REVIEW. NOT A SEALED PLAN.

Verify all dimensions before use.

TRAFFIC CONTROL DEVICE SUMMARY

MUTCD	DEVICE	QTY
G20-1	ROAD CONSTRUCTION (NEXT 500 FT)	2
G20-2	END ROAD WORK	2
G20-5P	CONSTRUCTION ZONE plaque	2
R2-10	BEGIN DOUBLE FINES ZONE	2
R2-11	END DOUBLE FINES ZONE	2
W20-1	ROAD WORK AHEAD	2
W20-5R	RIGHT LANE CLOSED AHEAD	2
W4-2R	RIGHT LANE ENDS	2
—	36-inch channelizing drum with alternating orange/white stripes	8
—	Traffic Cone (28-inch)	11
—	Trailer-mounted flashing arrow board (Type A, B, or C)	1
TOTAL DEVICES		**36**

SEE DEVICE LIST (XLSX) FOR BID QUANTITIES.

PROJECT:	#312 Colorado Blvd at E Exposition Ave
LOCATION:	S Colorado Blvd, Denver
COORDINATES:	39.70900, -104.94070
MHT TYPE:	LANE CLOSURE NEAR INTERSECTION · DIVIDED HIGHWAY
MUTCD:	TA-21
CDOT:	S-630-1
SCALE:	1" = 74 ft
DATE:	2026-10-12
SHEET:	1 OF 1
DRAWN BY:	MHT Tool (auto-generated)
STATUS:	**DRAFT: Not for stamping**