


METHOD OF HANDLING TRAFFIC — 30 MPH

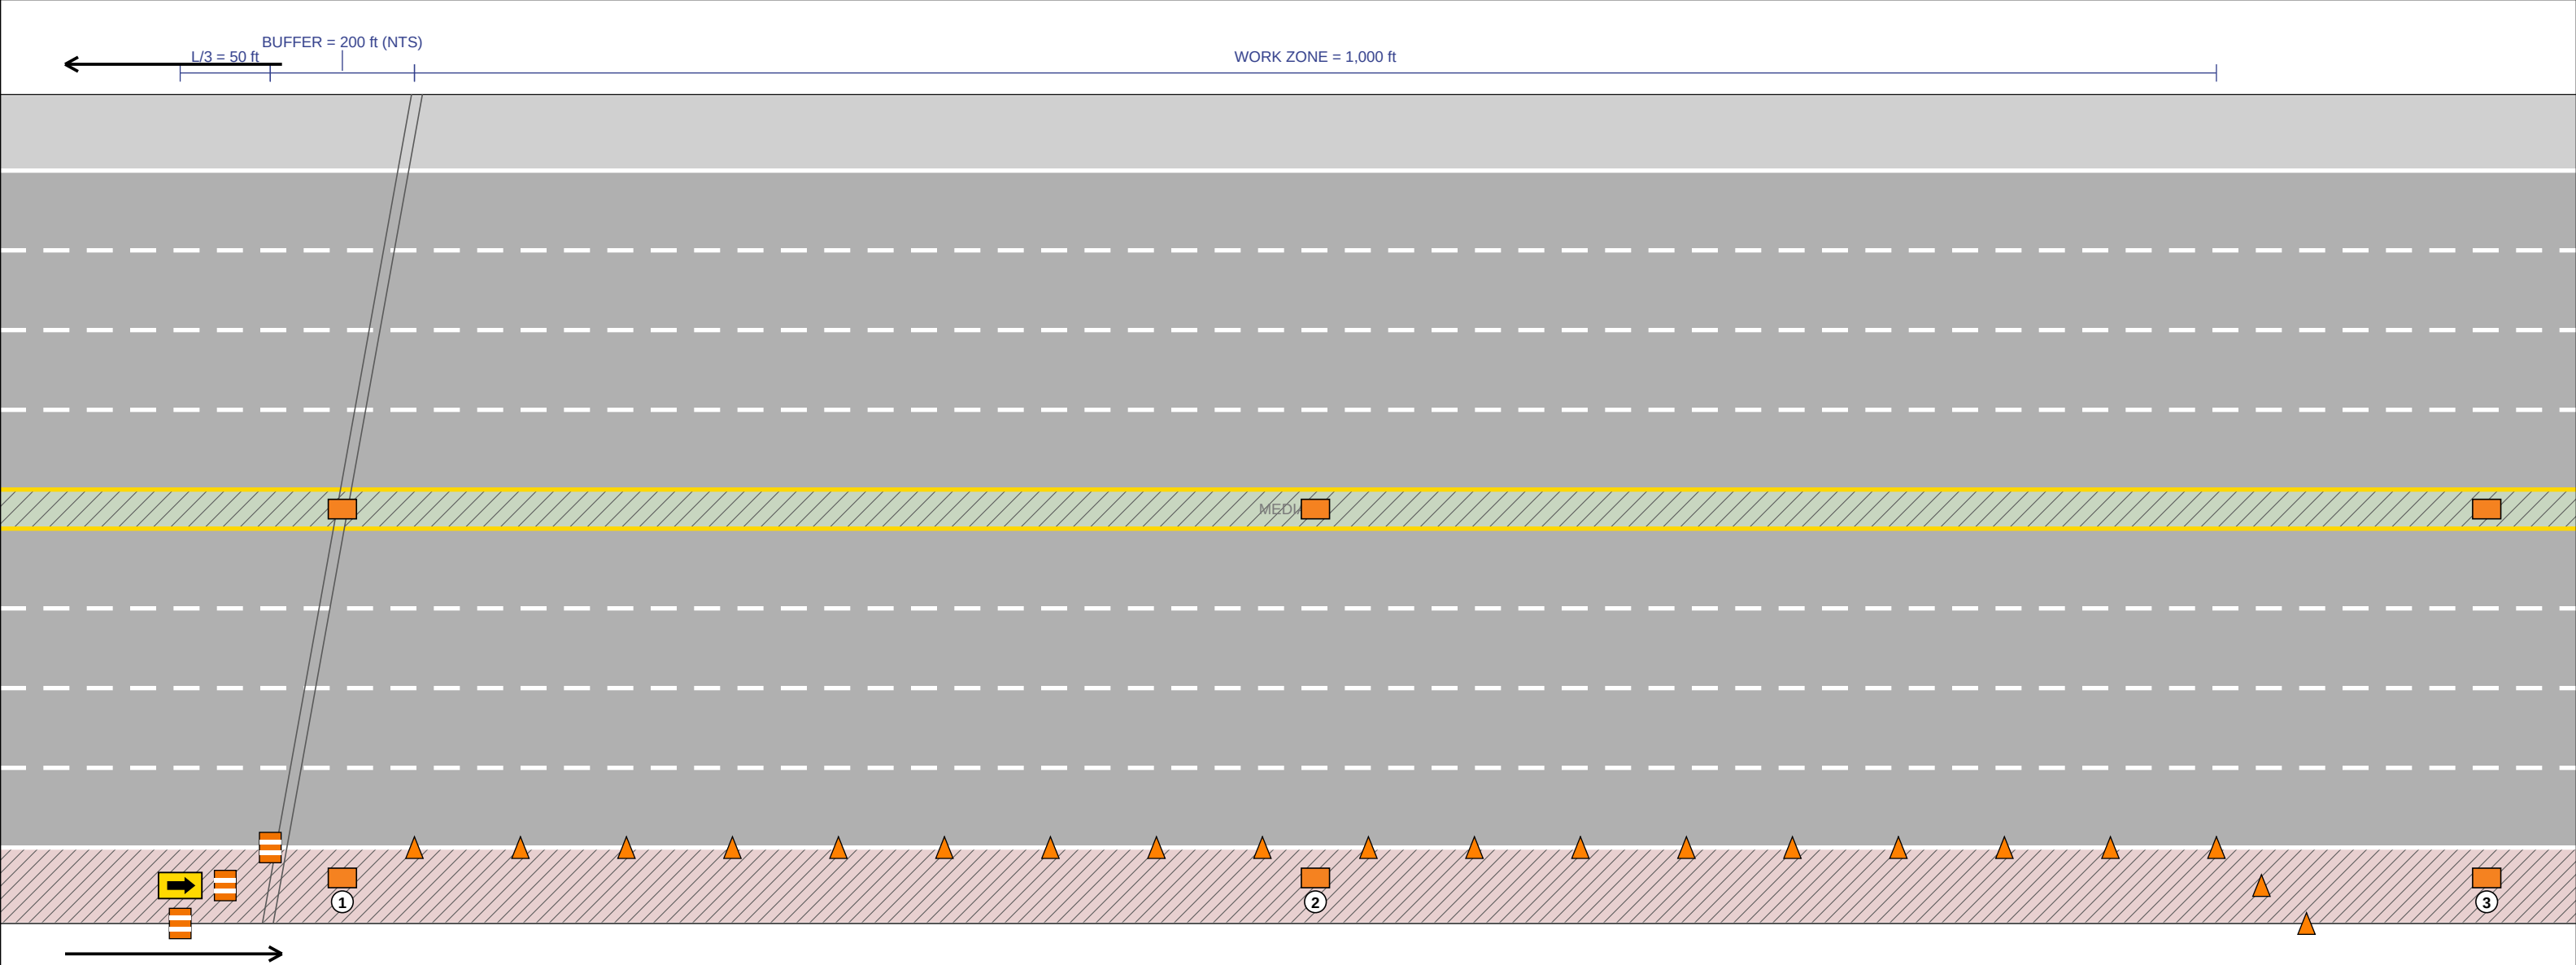

LEGEND

- Arrow Board
- Traffic Cone (28-inch)
- Channelizing Drum
- Warning sign (W series, e.g. W20-1)
- Construction guide (G series, e.g. G20-2)

ROAD GEOMETRY

Median (separates carriageways)

Left-side advance signs sit in the median
per S-630-1 Sheet 2 General Note 8.

Scale 1" = 87 ft applies to the work zone + taper. Buffer compressed; lateral offset exaggerated.

NOTES & SIGN SCHEDULE

PARAMETERS

Speed limit:	30 mph	Closure:	Shoulder Closure
Work zone:	1,000 ft	Shoulder taper (L/3):	50 ft
Buffer:	200 ft		

SIGN SCHEDULE

#	CODE	DESCRIPTION
1	G20-1	ROAD CONSTRUCTION (NEXT 1000 FT)
2	G20-5P	CONSTRUCTION ZONE plaque
3	G20-2	END ROAD WORK

ADVANCE WARNING SIGNS (off-page upstream of taper)

CODE	DESCRIPTION	DISTANCE
W21-5aR	RIGHT SHOULDER CLOSED AHEAD	100 ft
W20-2	ROAD WORK 200 FT	200 ft
W20-1	ROAD WORK AHEAD	300 ft

Reference: CDOT S-630-1, MUTCD 11th Ed. Part 6 (effective 2026-01-18), Colorado Supplement.
GENERATED BY CONESTRUCT — DRAFT FOR PE REVIEW. NOT A SEALED PLAN.
Verify all dimensions before use.

TRAFFIC CONTROL DEVICE SUMMARY

MUTCD	DEVICE	QTY
G20-1	ROAD CONSTRUCTION (NEXT 1000 FT)	2
G20-2	END ROAD WORK	2
G20-5P	CONSTRUCTION ZONE plaque	2
W20-1	ROAD WORK AHEAD	2
W20-2	ROAD WORK 200 FT	2
W21-5aR	RIGHT SHOULDER CLOSED AHEAD	2
—	36-inch channelizing drum with alternating orange/white stripes	3
—	Traffic Cone (28-inch)	20
—	Trailer-mounted flashing arrow board (Type A, B, or C)	1


TOTAL DEVICES

36

SEE DEVICE LIST (XLSX) FOR BID QUANTITIES.

PROJECT:	Untitled Project
LOCATION:	—
COORDINATES:	39.73370, -104.98753
MHT TYPE:	SHOULDER CLOSURE — DIVIDED HIGHWAY
MUTCD:	TA-3
CDOT:	S-630-1
SCALE:	1" = 87 ft
DATE:	2026-09-25
SHEET:	1 OF 2
AERIAL:	See page 2
DRAWN BY:	MHT Tool (auto-generated)
STATUS:	DRAFT — Not for stamping

AERIAL CONTEXT

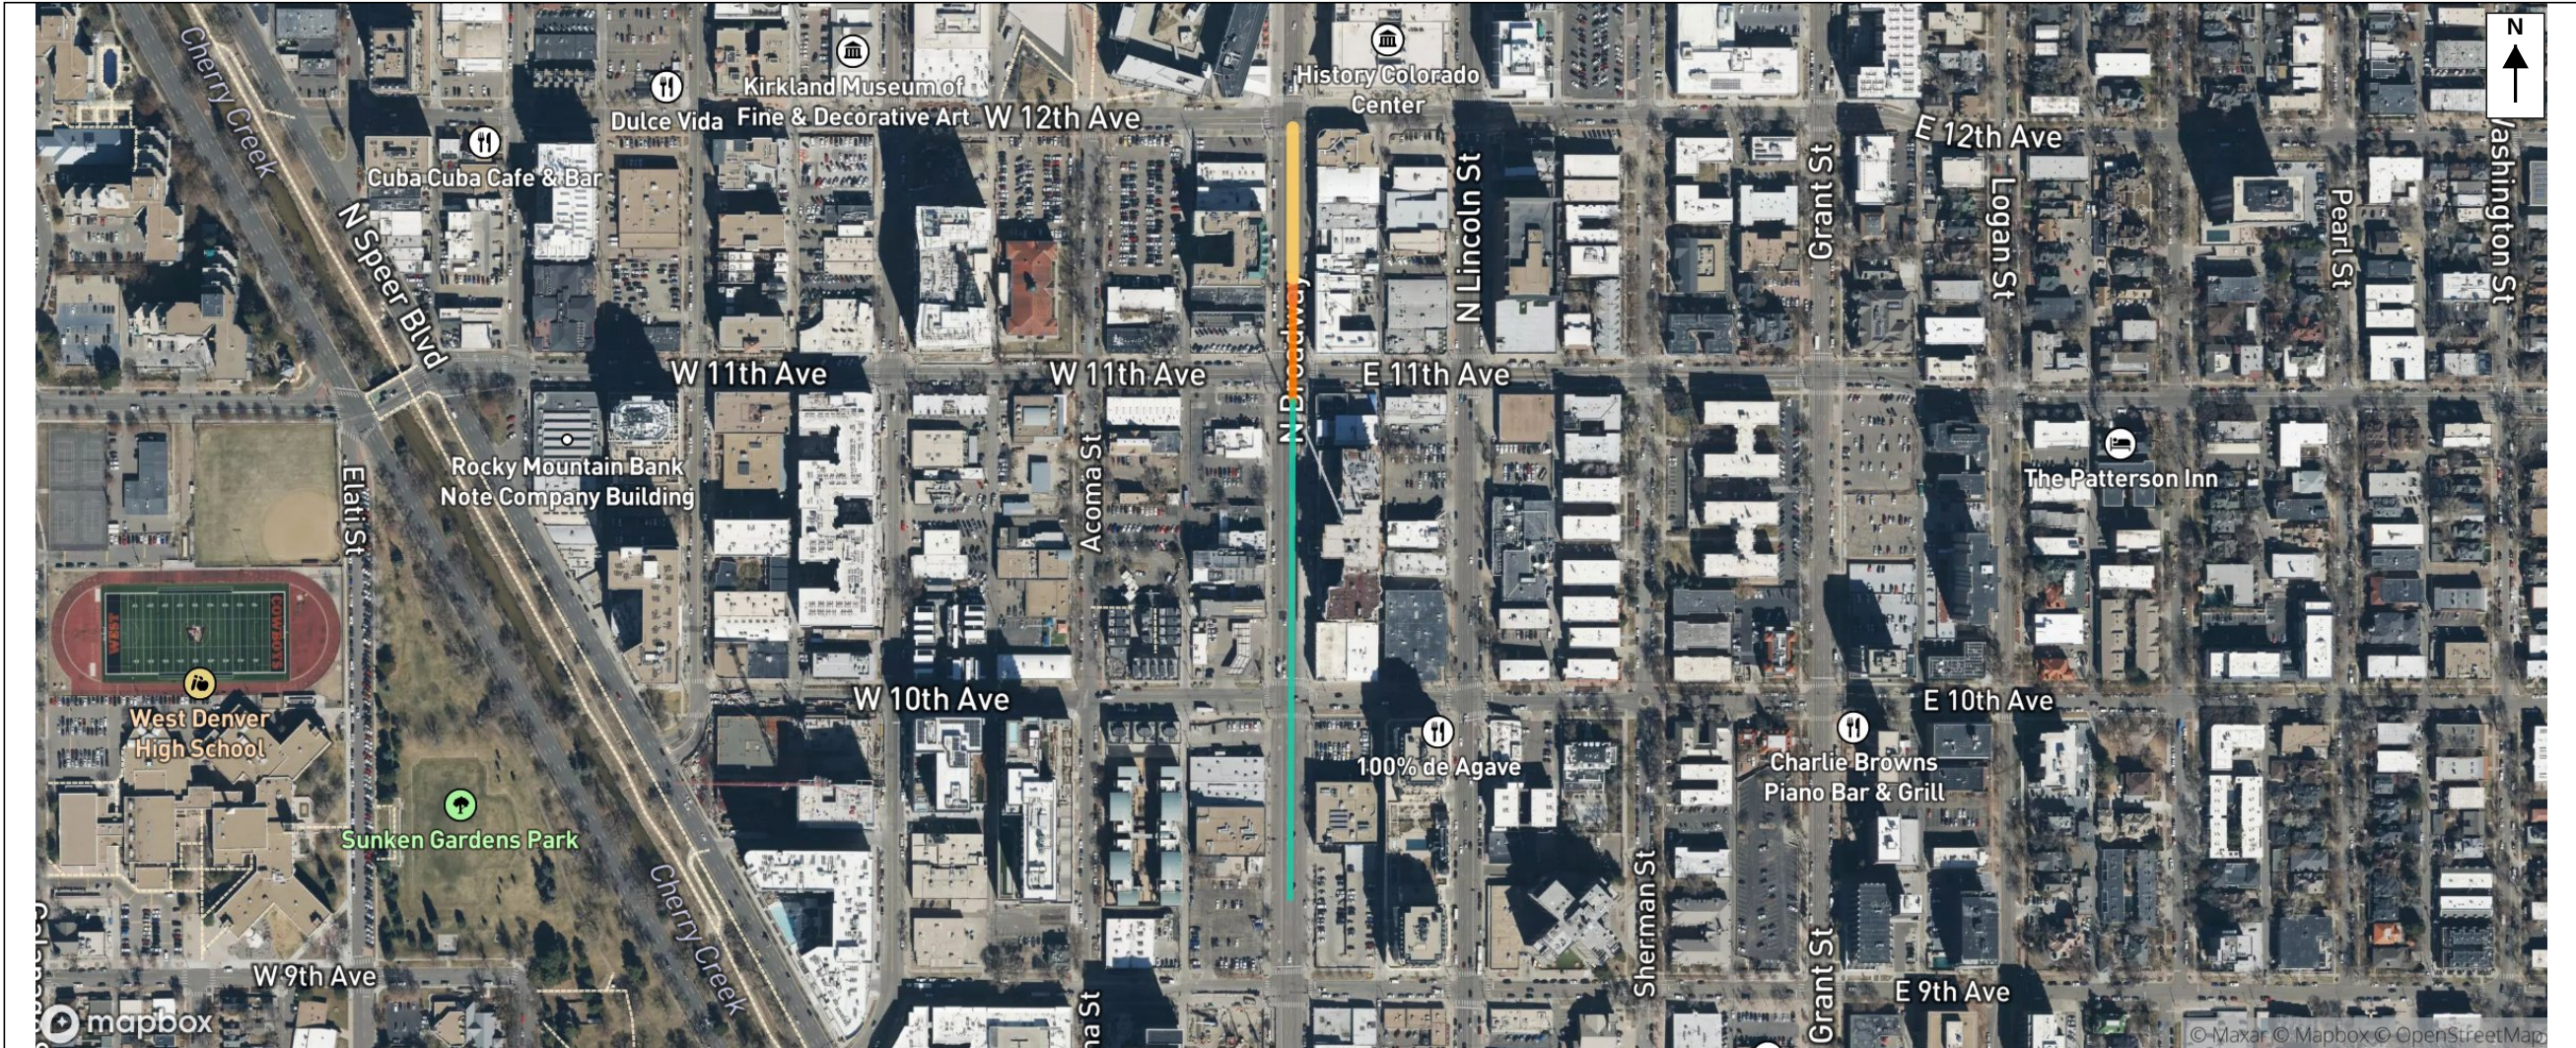

SITE: 39.73370, -104.98753

Advance warning Taper Buffer Work zone Downstream faded: past the mapped road
Mapbox satellite imagery with street labels — for context only. Not a survey product. Verify all field conditions on site.

CORRIDOR DETAILS

Work starts:	39.73370, -104.98753
Direction of travel:	180°
Total corridor:	1,600 ft (0.30 mi)
Advance warning:	300 ft
Taper:	50 ft
Buffer:	200 ft
Work zone:	1,000 ft
Downstream:	50 ft
Centerline:	OSM, full corridor