


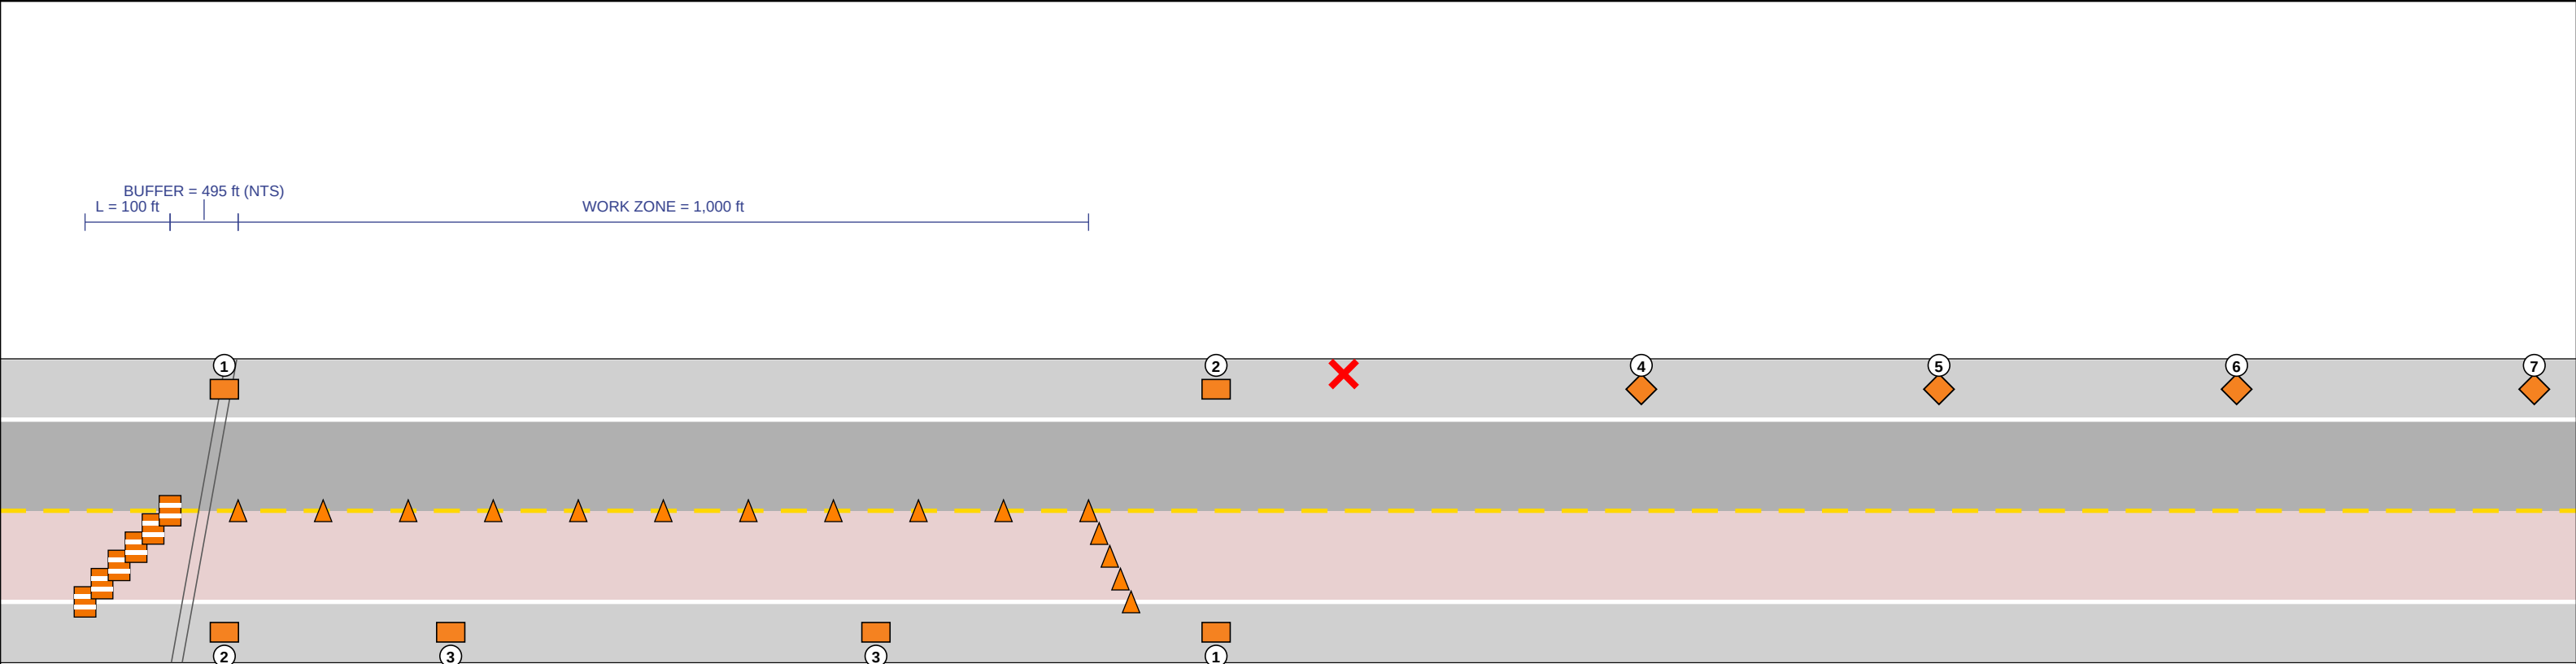

LEGEND

- Traffic Cone (36-inch)
- Channelizing Drum
- Flagger Station

SIGN CATEGORIES

- Warning sign (W series, e.g. W20-1)
- Construction guide (G series, e.g. G20-2)

Scale 1" = 184 ft applies to the work zone + taper. Buffer compressed; lateral offset exaggerated.

NOTES & SIGN SCHEDULE

PARAMETERS			
Speed limit:	55 mph	Closure:	Flagger Alternating Traffic
Work zone:	1,000 ft	One-lane two-way taper:	100 ft
Buffer:	495 ft		

SIGN SCHEDULE		
#	CODE	DESCRIPTION
1	G20-2	END ROAD WORK
2	G20-1	ROAD CONSTRUCTION (NEXT 1000 FT)
3	G20-5P	CONSTRUCTION ZONE plaque
4	W20-7	FLAGGER AHEAD
5	W3-4	BE PREPARED TO STOP
6	W20-4	ONE LANE ROAD AHEAD
7	W20-1	ROAD WORK AHEAD

ADVANCE WARNING SIGNS & FLAGGER STATIONS (off-page upstream of taper)					
CODE	DESCRIPTION	DISTANCE	CODE	DESCRIPTION	DISTANCE
—	FLAGGER STATION #1 (APPROACH)	100 ft	W20-4	ONE LANE ROAD AHEAD	1150 ft
W20-7	FLAGGER AHEAD	450 ft	W20-1	ROAD WORK AHEAD	1500 ft
W3-4	BE PREPARED TO STOP	800 ft			

Reference: CDOT S-630-1, MUTCD 11th Ed. Part 6 (effective 2026-01-18), Colorado Supplement.
GENERATED BY CONESTRUCT — DRAFT FOR PE REVIEW. NOT A SEALED PLAN.
Verify all dimensions before use.

TRAFFIC CONTROL DEVICE SUMMARY


MUTCD	DEVICE	QTY
G20-1	ROAD CONSTRUCTION (NEXT 1000 FT)	2
G20-2	END ROAD WORK	2
G20-5P	CONSTRUCTION ZONE plaque	2
W20-1	ROAD WORK AHEAD	2
W20-4	ONE LANE ROAD AHEAD	2
W20-7	FLAGGER AHEAD	2
W3-4	BE PREPARED TO STOP	2
—	36-inch channelizing drum with alternating orange/white stripes	6
—	Traffic Cone (36-inch)	15
—	Flagger position with STOP/SLOW paddle and PPE	2

TOTAL DEVICES 37

SEE DEVICE LIST (XLSX) FOR BID QUANTITIES.

PROJECT:	Untitled Project
LOCATION:	—
COORDINATES:	39.74362, -104.97070
MHT TYPE:	FLAGGER ALTERNATING TRAFFIC — 2-LANE UNDIVIDED
MUTCD:	TA-10
CDOT:	S-630-1
SCALE:	1" = 184 ft
DATE:	2026-09-25
SHEET:	1 OF 2
AERIAL:	See page 2
DRAWN BY:	MHT Tool (auto-generated)
STATUS:	DRAFT — Not for stamping

AERIAL CONTEXT

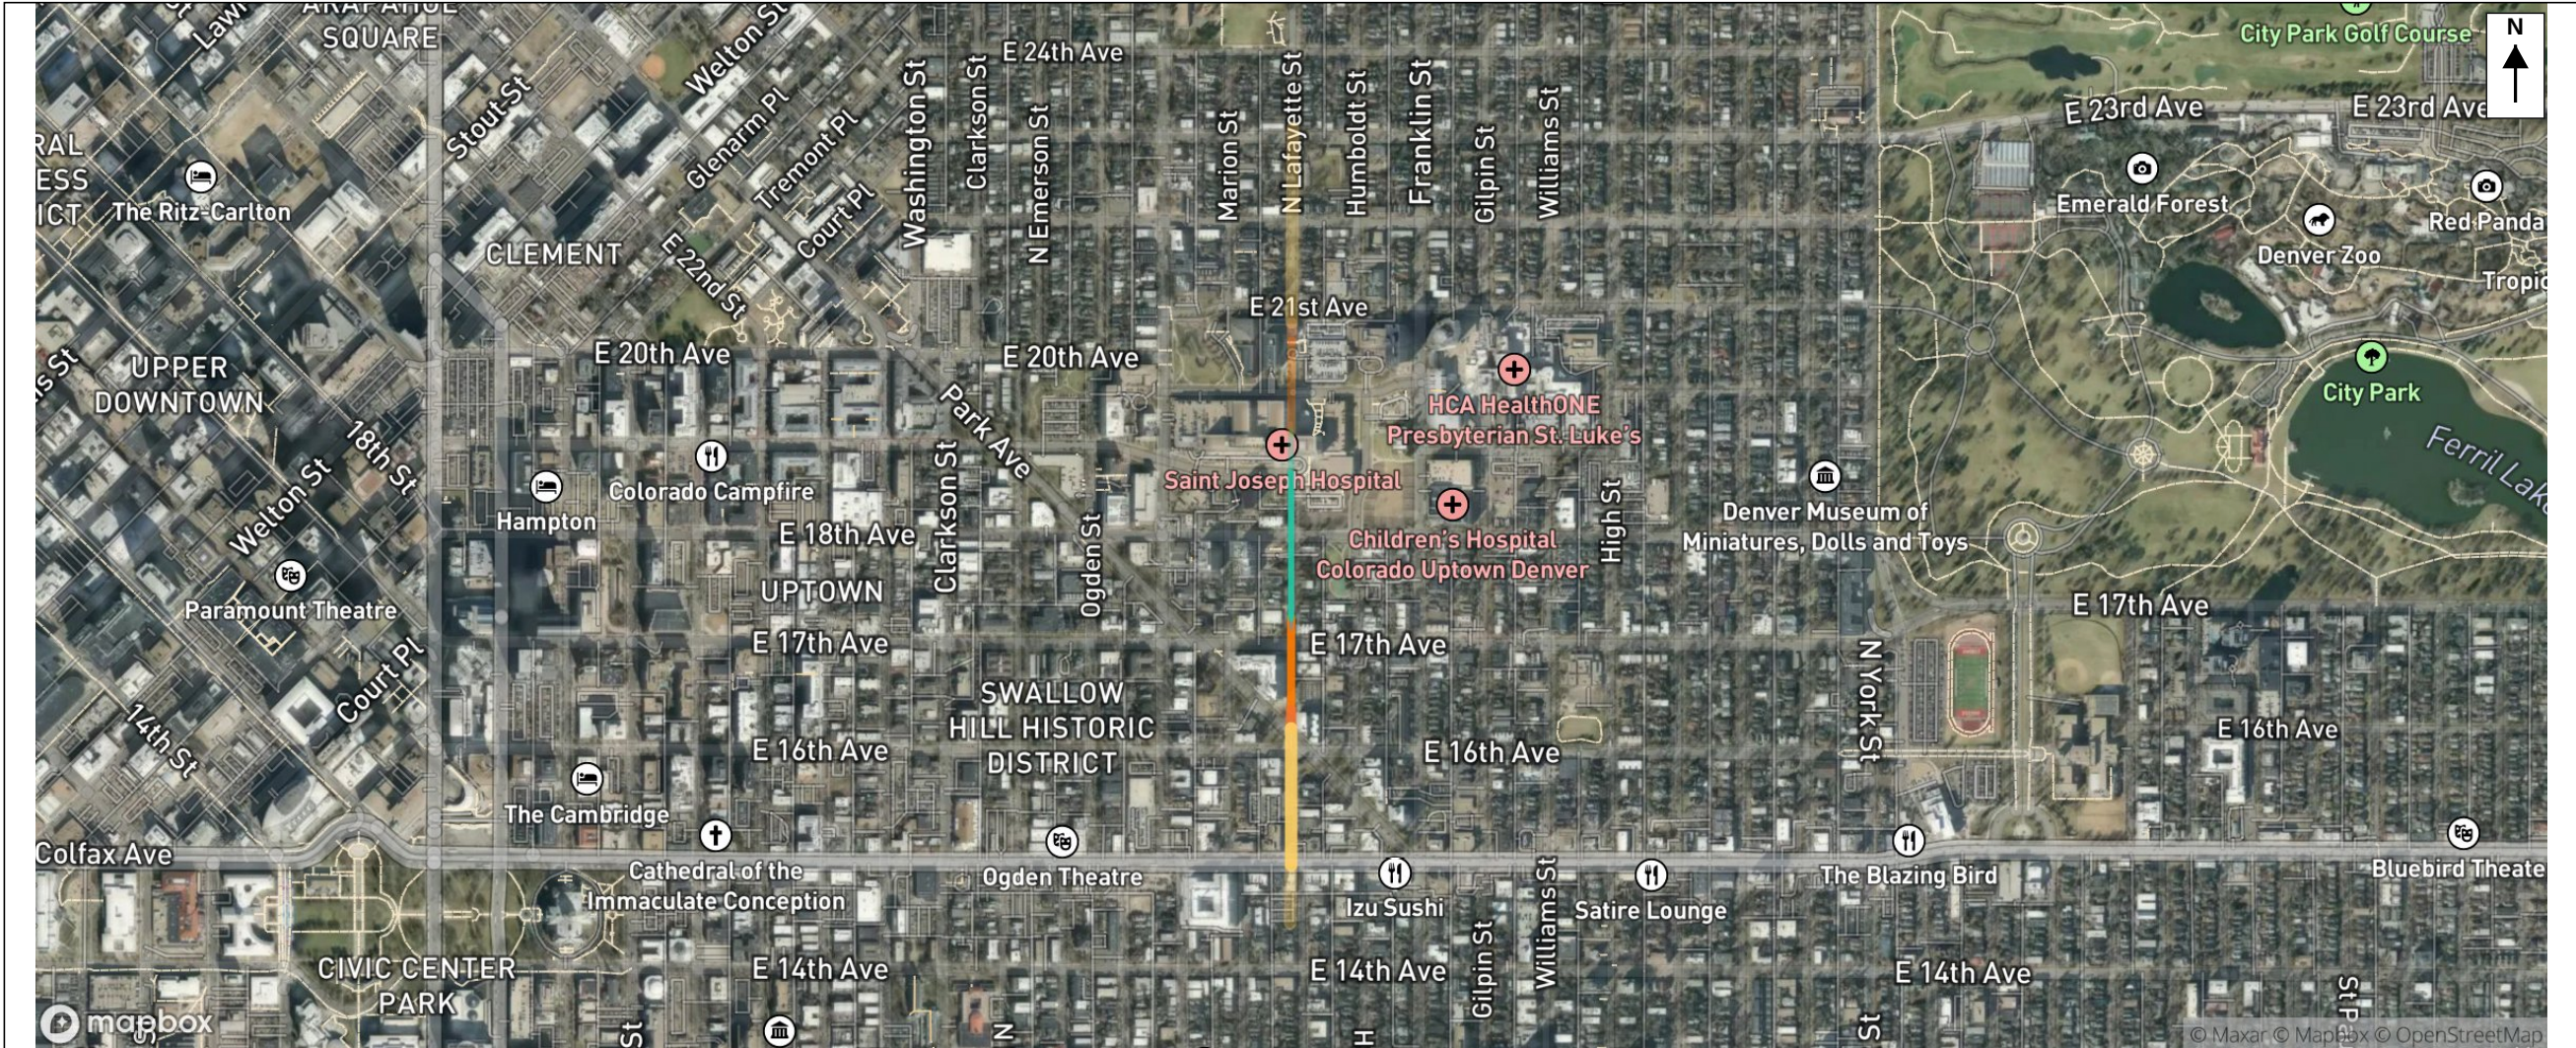

SITE: 39.74362, -104.97070

Advance warning Taper Buffer Work zone Downstream faded: past the mapped road · Two approaches: northbound (the work's side) and southbound

Mapbox satellite imagery with street labels — for context only. Not a survey product. Verify all field conditions on site.

CORRIDOR DETAILS

Work starts:	39.74362, -104.97070
Direction of travel:	0°
Total corridor:	2,695 ft (0.51 mi)
Advance warning:	1,050 ft
Taper:	100 ft
Buffer:	495 ft
Work zone:	1,000 ft
Downstream:	50 ft
Centerline:	covers 265–2,381 ft, bearing beyond