
METHOD OF HANDLING TRAFFIC · 55 MPH

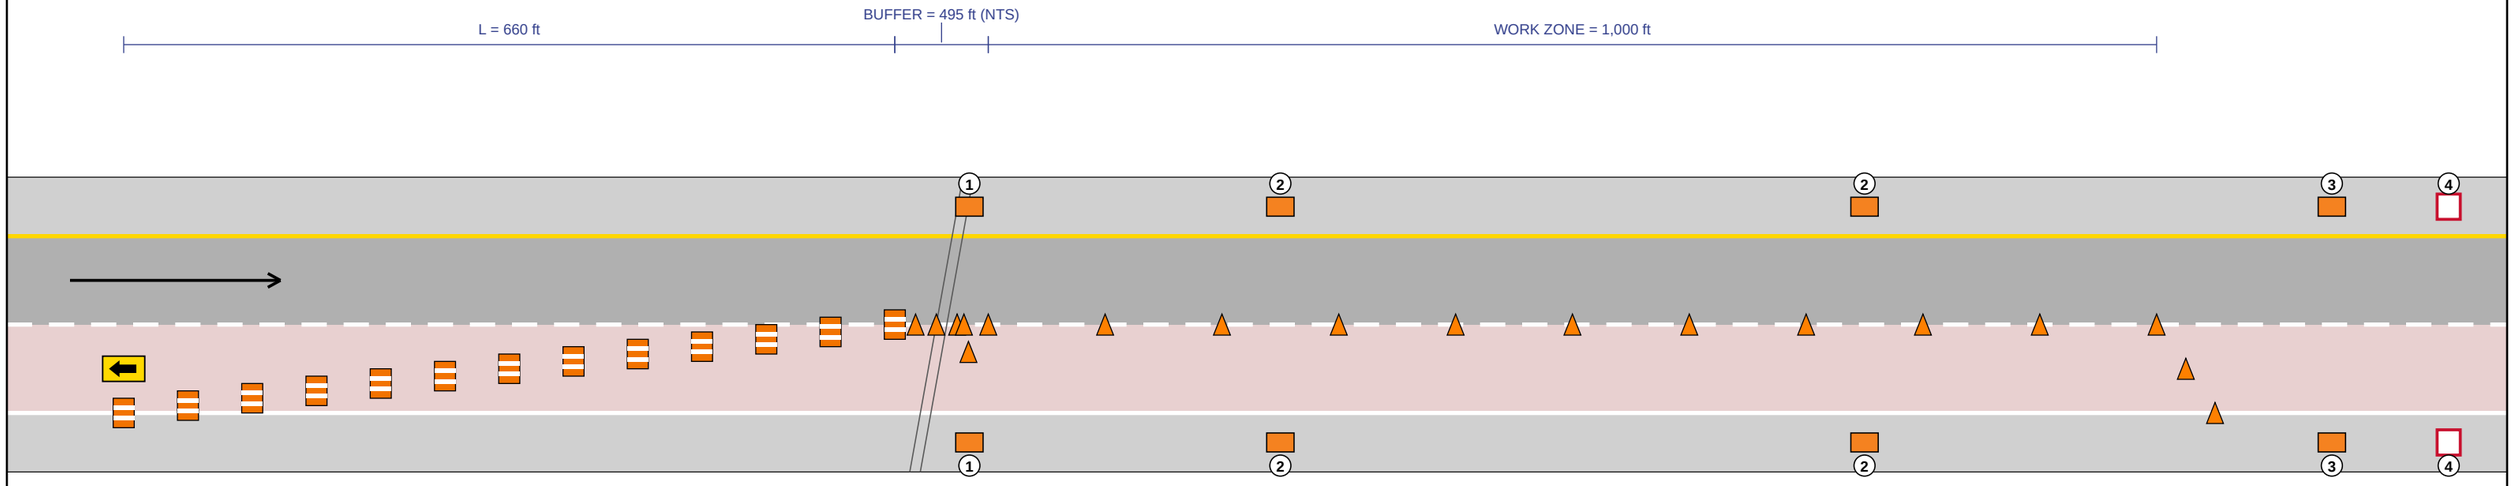

LEGEND

- Arrow Board
- Traffic Cone (36-inch)
- Channelizing Drum

SIGN CATEGORIES

- Warning sign (W series, e.g. W20-1)
- Construction guide (G series, e.g. G20-2)
- Regulatory sign (R series, e.g. R9-9)

Scale 1" = 130 ft applies to the work zone + taper. Buffer compressed; lateral offset exaggerated.

NOTES & SIGN SCHEDULE

PARAMETERS

Speed limit:	**55 mph**	Closure:	**Lane Closure Near Intersection**
Work zone:	**1,000 ft**	Lane taper (L):	**660 ft**
Buffer:	**495 ft**		

SIGN SCHEDULE

#	CODE	DESCRIPTION
1	**G20-1**	ROAD CONSTRUCTION (NEXT 1000 FT)
2	**G20-5P**	CONSTRUCTION ZONE plaque
3	**G20-2**	END ROAD WORK
4	**R2-11**	END DOUBLE FINES ZONE

4 ADVANCE SIGNS OFF-PAGE (W4-2R, W20-5R, R2-10, W20-1). SEE CREW NARRATIVE & DEVICE LIST

Reference: CDOT S-630-1, MUTCD 11th Edition Part 6, Colorado Supplement (effective January 18, 2026).
SPEED GUESSED FROM THE ROAD CLASS. CONFIRM THE POSTED SPEED ON SITE.
CROSS-STREET CONTROL PER CDOT S-630-1 SHEET 10, CASES 18/19: NOT DRAWN. PLATE DEPARTURES: SEE AUDIT. SEE DEVICE LIST, CREW NARRATIVE, AND AUDIT.
CLOSED LANE DRAWN AS THE RIGHTMOST LANE: A MODELING ASSUMPTION; NO MUTCD RULE SELECTS THE LANE (THE WORK LOCATION DOES). IF THE WORK OCCUPIES A DIFFERENT LANE, THIS PLAN DOES NOT APPLY AS DRAWN.
GENERATED BY CONESTRUCT. DRAFT FOR PE REVIEW. NOT A SEALED PLAN.
Verify all dimensions before use.

TRAFFIC CONTROL DEVICE SUMMARY


MUTCD	DEVICE	QTY
G20-1	ROAD CONSTRUCTION (NEXT 1000 FT)	2
G20-2	END ROAD WORK	2
G20-5P	CONSTRUCTION ZONE plaque	4
R2-10	BEGIN DOUBLE FINES ZONE	2
R2-11	END DOUBLE FINES ZONE	2
W20-1	ROAD WORK AHEAD	2
W20-5R	RIGHT LANE CLOSED AHEAD	2
W4-2R	RIGHT LANE ENDS	2
—	36-inch channelizing drum with alternating orange/white stripes	13
—	Traffic Cone (36-inch)	18
—	Trailer-mounted flashing arrow board (Type A, B, or C)	1
TOTAL DEVICES		**50**

SEE DEVICE LIST (XLSX) FOR BID QUANTITIES.

PROJECT:	Untitled Project
LOCATION:	—
COORDINATES:	39.69322, -104.99425
MHT TYPE:	LANE CLOSURE NEAR INTERSECTION · DIVIDED HIGHWAY
MUTCD:	TA-22
CDOT:	S-630-1
SCALE:	1" = 130 ft
DATE:	2026-10-14
SHEET:	1 OF 2
AERIAL:	See page 2
DRAWN BY:	MHT Tool (auto-generated)
STATUS:	**DRAFT: Not for stamping**

METHOD OF HANDLING TRAFFIC · 55 MPH

AERIAL CONTEXT

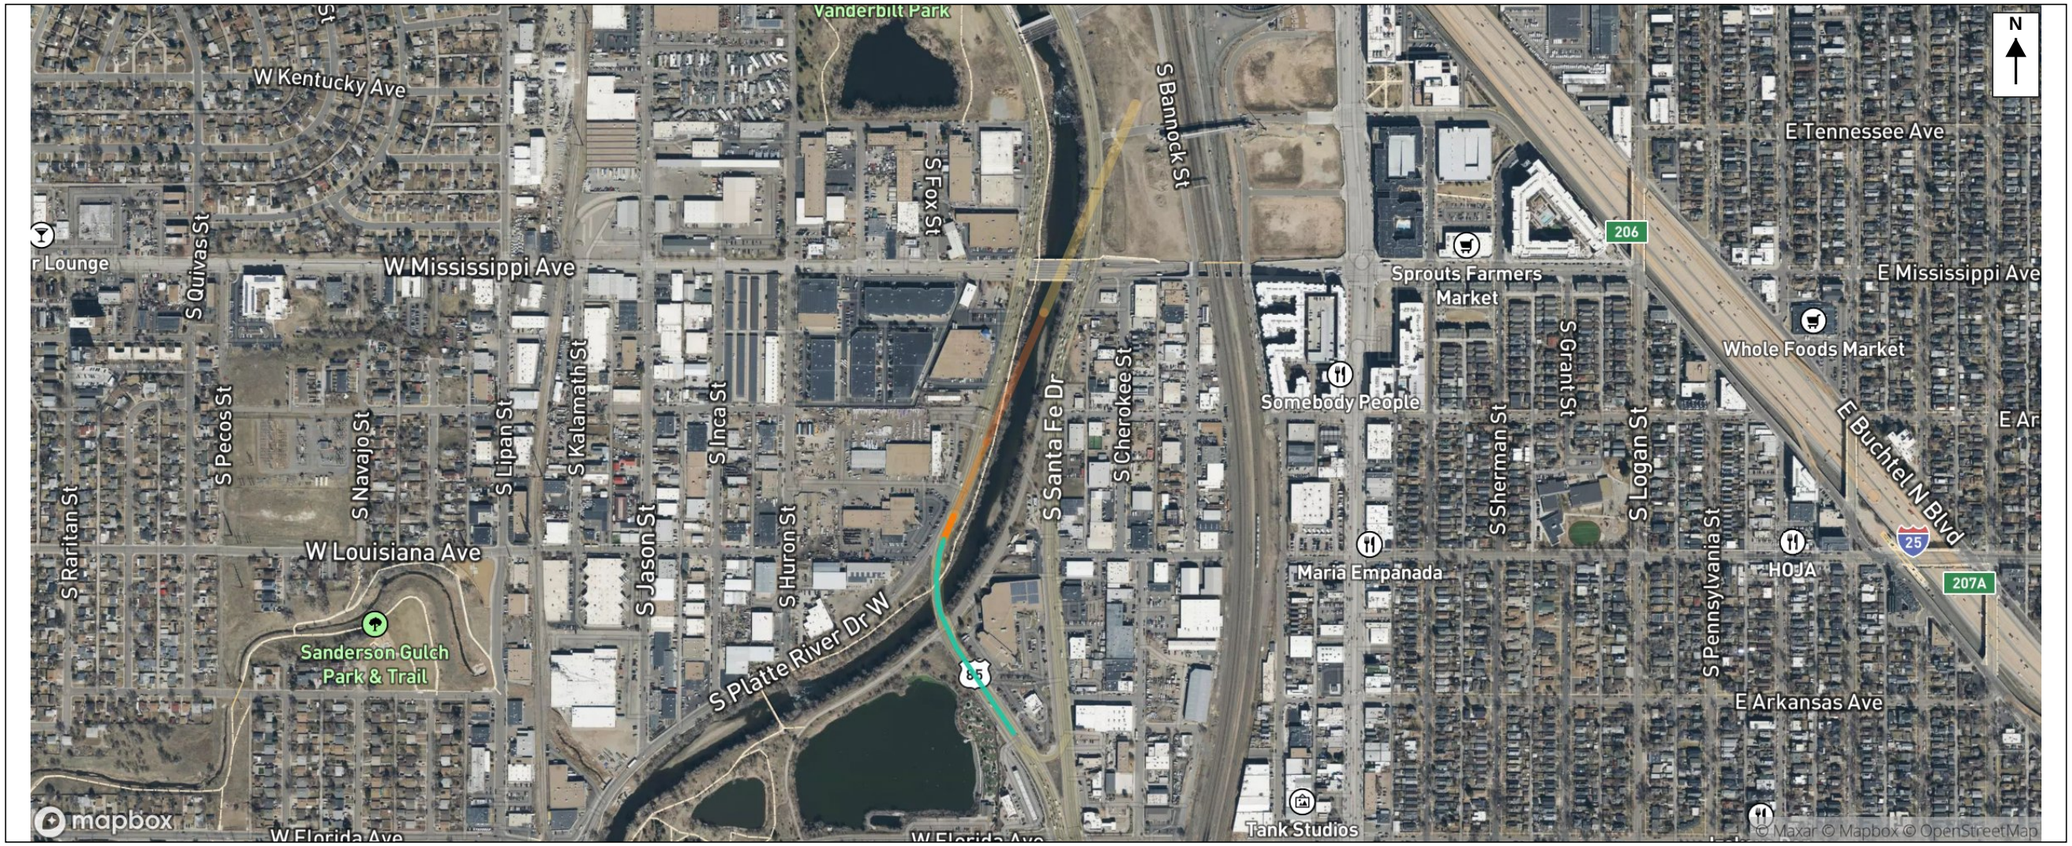

SITE: 39.69322, -104.99425

Advance warning — Taper — Buffer — Work zone — Downstream — faded: past the mapped road

Mapbox satellite imagery with street labels, for context only. Not a survey product. Verify all field conditions on site.

CORRIDOR DETAILS

Work starts:	39.69322, -104.99425
Direction of travel:	196°
Total corridor:	3,255 ft (0.62 mi)
Advance warning:	1,050 ft
Taper:	660 ft
Buffer:	495 ft
Work zone:	1,000 ft
Downstream:	50 ft
Centerline:	covers 0–1,167 ft, bearing beyond