


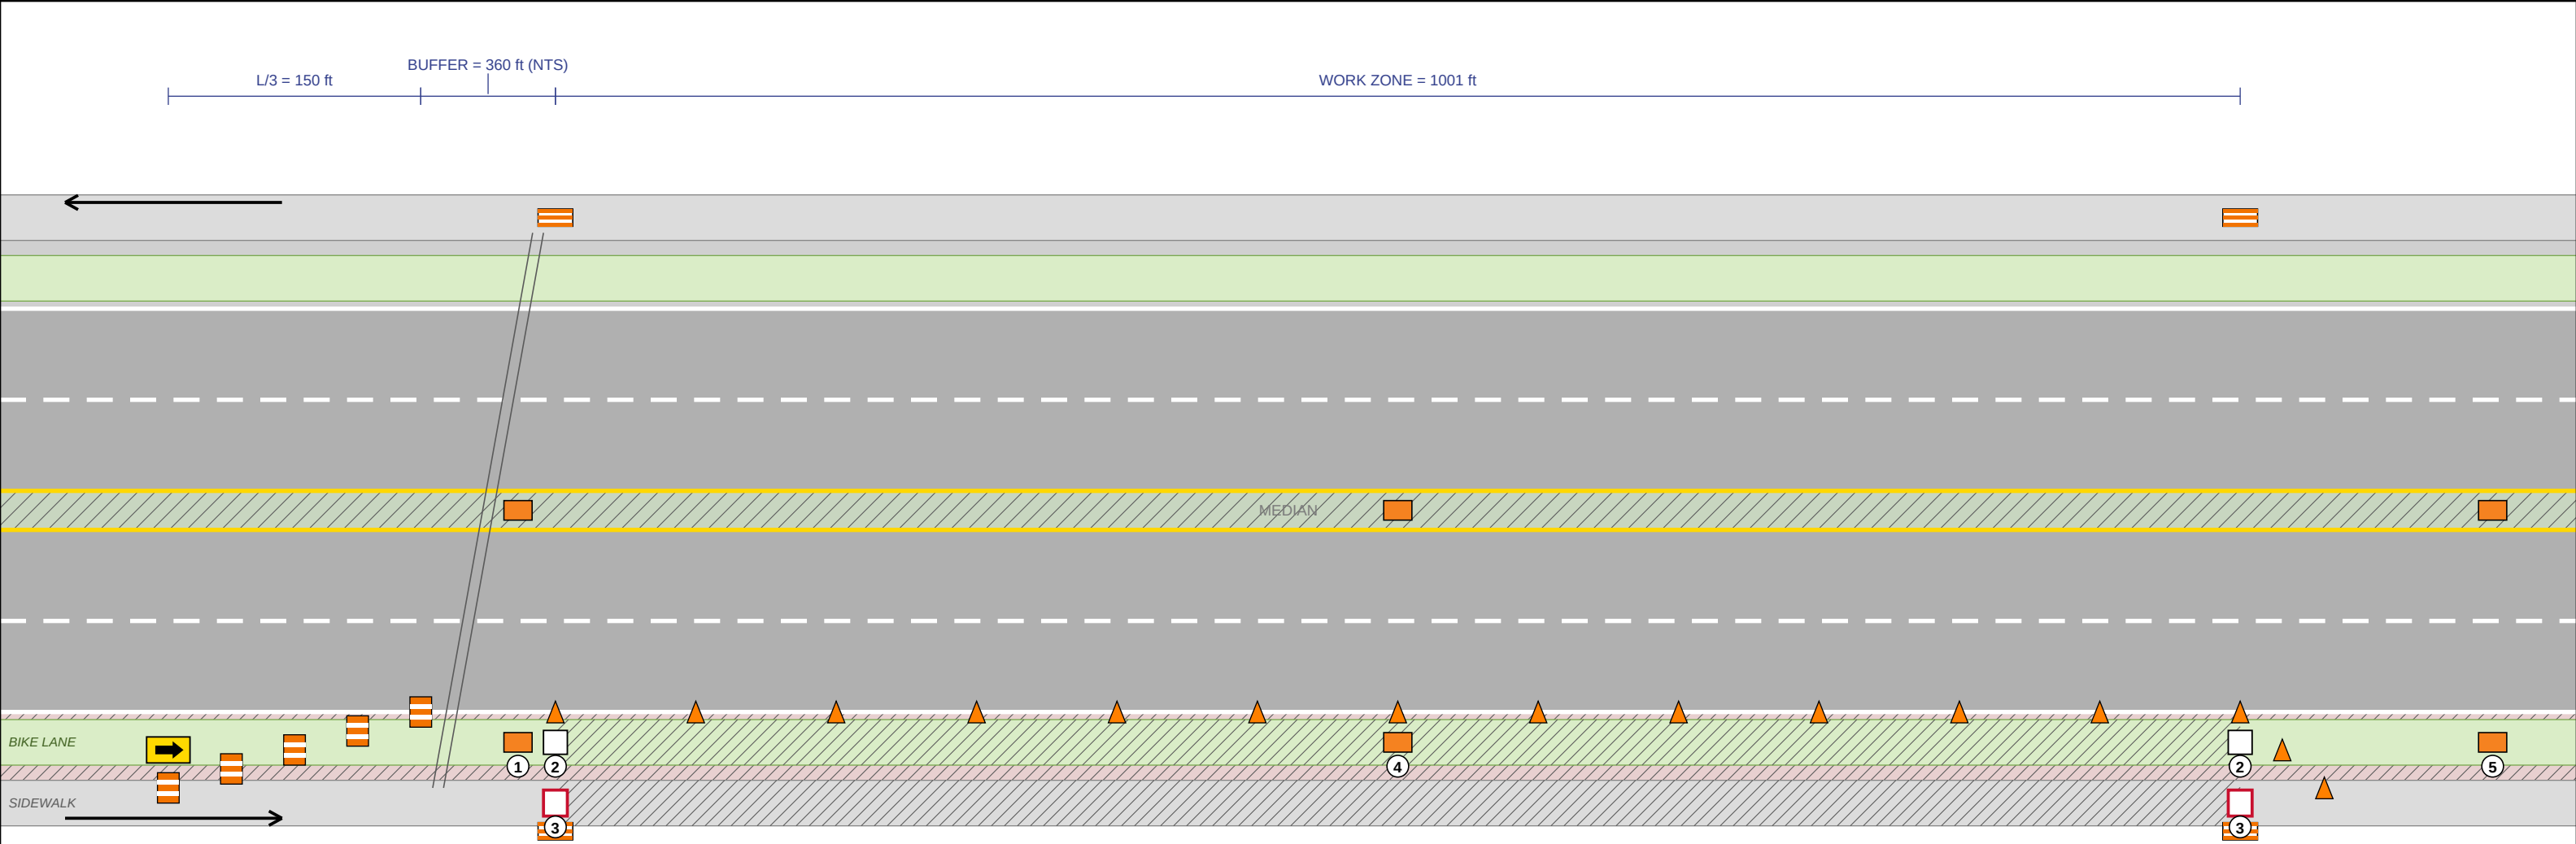

LEGEND

- Arrow Board
- Type III Barricade
- Traffic Cone (36-inch)
- Channelizing Drum
- Warning sign (W series, e.g. W20-1)
- Construction guide (G series, e.g. G20-2)
- Regulatory sign (R series, e.g. R9-9)
- Route guidance (M series, e.g. M4-9a)

+3 MORE — SEE DEVICE LIST (XLSX)

Scale 1" = 93 ft applies to the work zone + taper. Buffer compressed; lateral offset exaggerated.

NOTES & SIGN SCHEDULE


PARAMETERS			
Speed limit:	45 mph	Closure:	Shoulder Closure
Work zone:	1001 ft	Shoulder taper (L/3):	150 ft
Buffer:	360 ft		
SIGN SCHEDULE			
#	CODE	DESCRIPTION	
1	G20-1	ROAD CONSTRUCTION (NEXT 1001 FT)	
2	M4-9a	BIKE DETOUR	
3	R9-9	SIDEWALK CLOSED	
4	G20-5P	CONSTRUCTION ZONE plaque	
5	G20-2	END ROAD WORK	
ADVANCE WARNING SIGNS (off-page upstream of taper)			
CODE	DESCRIPTION	DISTANCE	
W21-5aR	RIGHT SHOULDER CLOSED AHEAD	350 ft	
W20-2	ROAD WORK 700 FT	700 ft	
W20-1	ROAD WORK AHEAD	1050 ft	
Reference: CDOT S-630-1, MUTCD 11th Ed. Part 6 (effective 2026-01-18), Colorado Supplement.			
GENERATED BY CONSTRUCT — DRAFT FOR PE REVIEW. NOT A SEALED PLAN.			
Verify all dimensions before use.			

TRAFFIC CONTROL DEVICE SUMMARY

MUTCD	DEVICE	QTY
G20-1	ROAD CONSTRUCTION (NEXT 1001 FT)	2
G20-2	END ROAD WORK	2
G20-5P	CONSTRUCTION ZONE plaque	2
M4-9a	BIKE DETOUR	2
R9-9	SIDEWALK CLOSED	2
W20-1	ROAD WORK AHEAD	2
W20-2	ROAD WORK 700 FT	2
W21-5aR	RIGHT SHOULDER CLOSED AHEAD	2
—	36-inch channelizing drum with alternating orange/white stripes	5
—	Traffic Cone (36-inch)	15
—	Type III barricade — three horizontal striped rails, full lane width	4
—	Trailer-mounted flashing arrow board (Type A, B, or C)	1
TOTAL DEVICES		41
SEE DEVICE LIST (XLSX) FOR BID QUANTITIES.		

PROJECT:	s2a17 live check
LOCATION:	—
COORDINATES:	39.71130, -105.08150
MHT TYPE:	SHOULDER CLOSURE — DIVIDED HIGHWAY
MUTCD:	TA-3
CDOT:	S-630-1
SCALE:	1" = 93 ft
DATE:	2026-09-04
SHEET:	1 OF 2
AERIAL:	See page 2
DRAWN BY:	MHT Tool (auto-generated)
STATUS:	DRAFT — Not for stamping

AERIAL CONTEXT

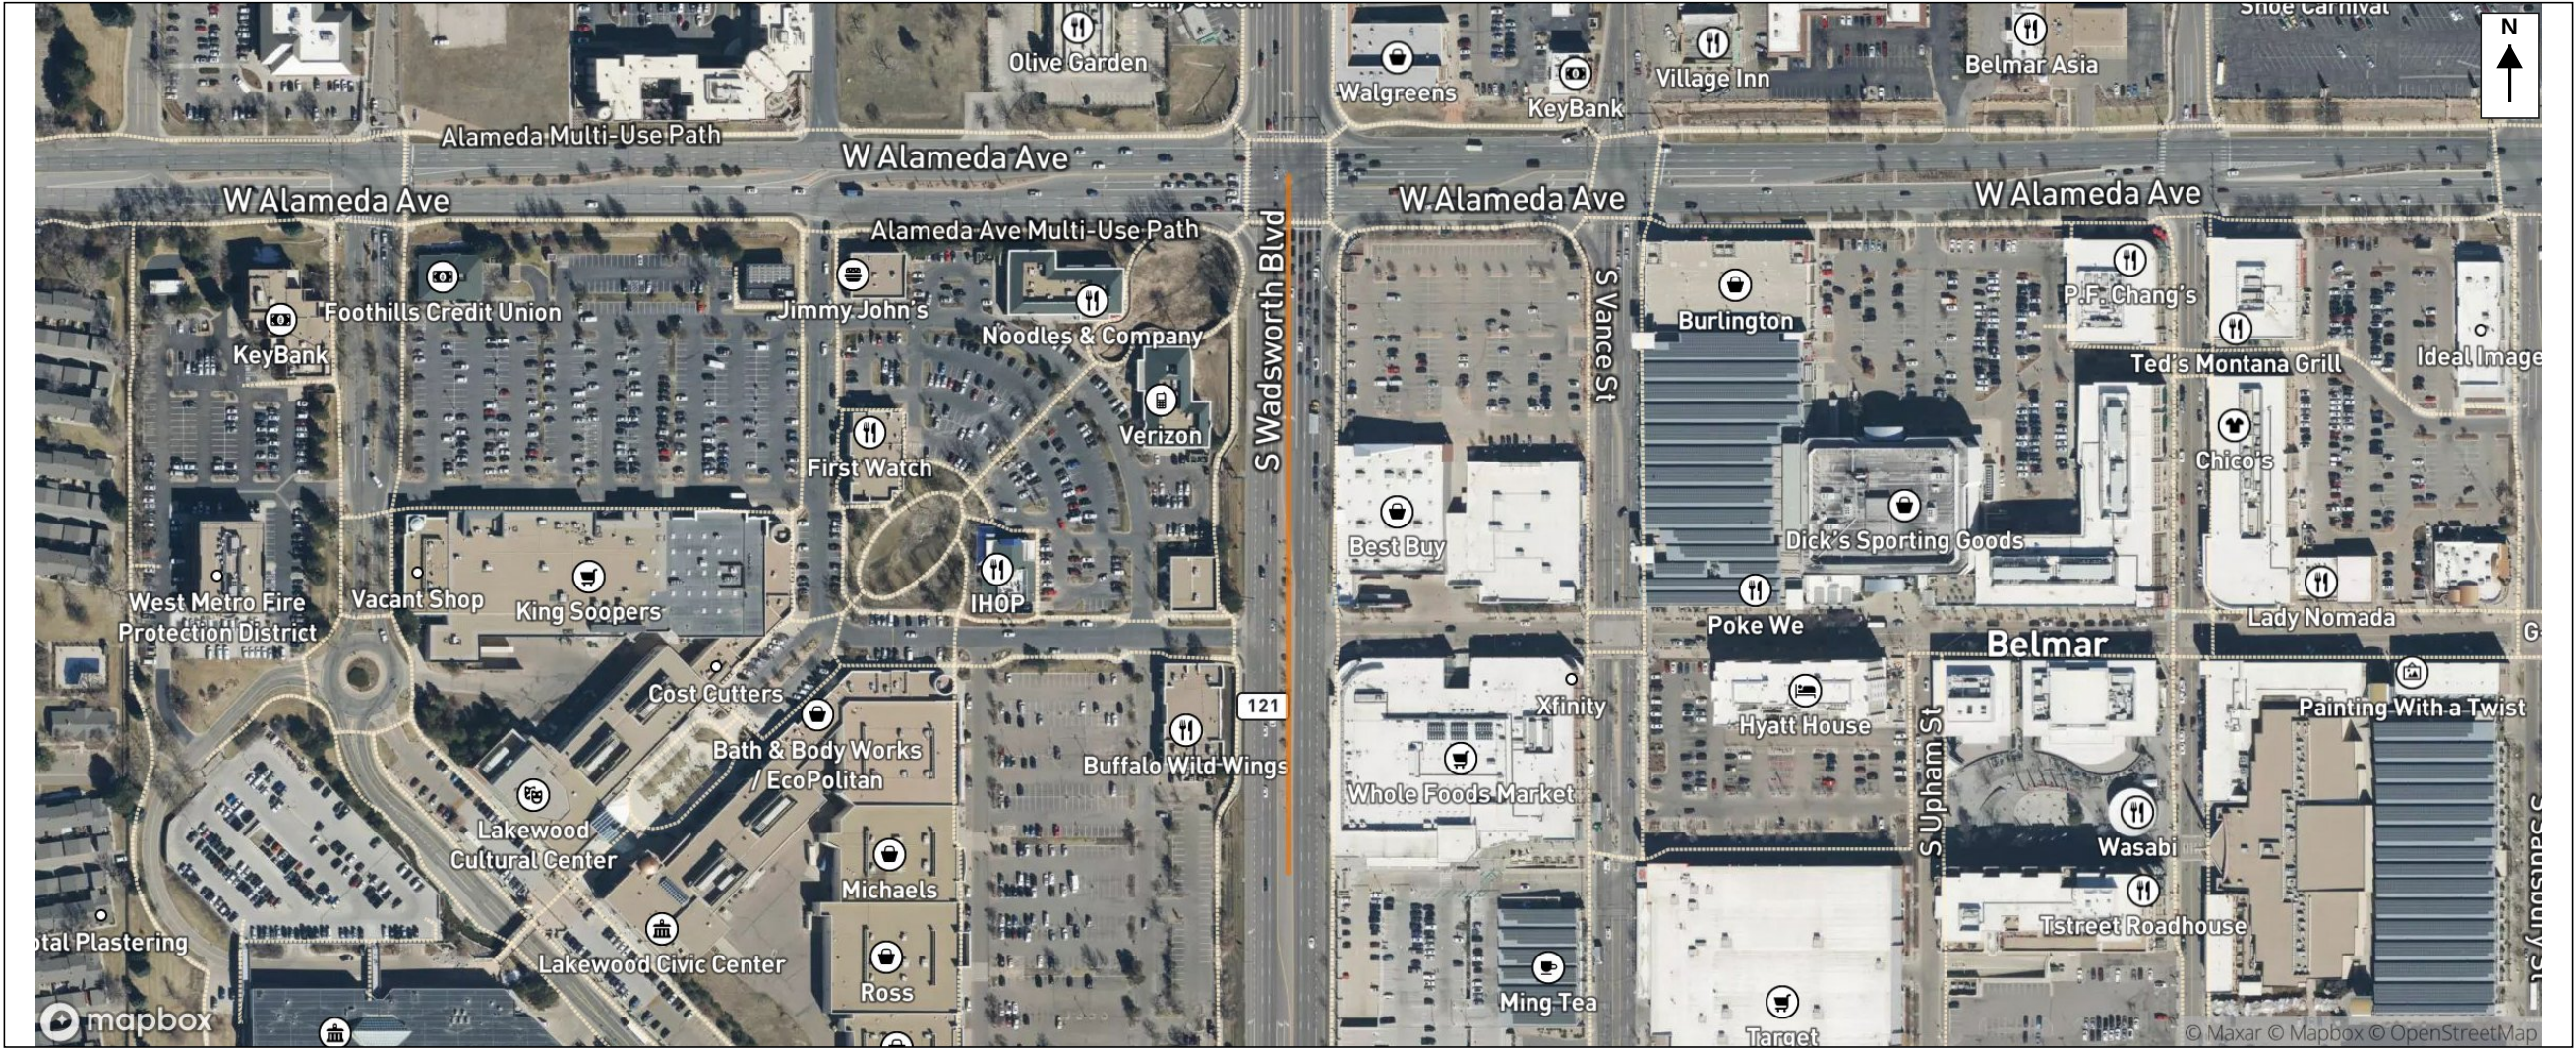

SITE: 39.71130, -105.08150

Work zone (1,001 ft) shown in orange. Advance warning, taper, and buffer not depicted. Mapbox satellite imagery with street labels — for context only. Not a survey product. Verify all field conditions on site.

CORRIDOR DETAILS

Anchor:	39.71130, -105.08150
Bearing:	180°
Total corridor:	2,661 ft (0.50 mi)
Advance warning:	1,050 ft
Taper:	150 ft
Buffer:	360 ft
Work zone:	1,001 ft
Downstream:	100 ft