


METHOD OF HANDLING TRAFFIC · Colfax Water Main · 35 MPH

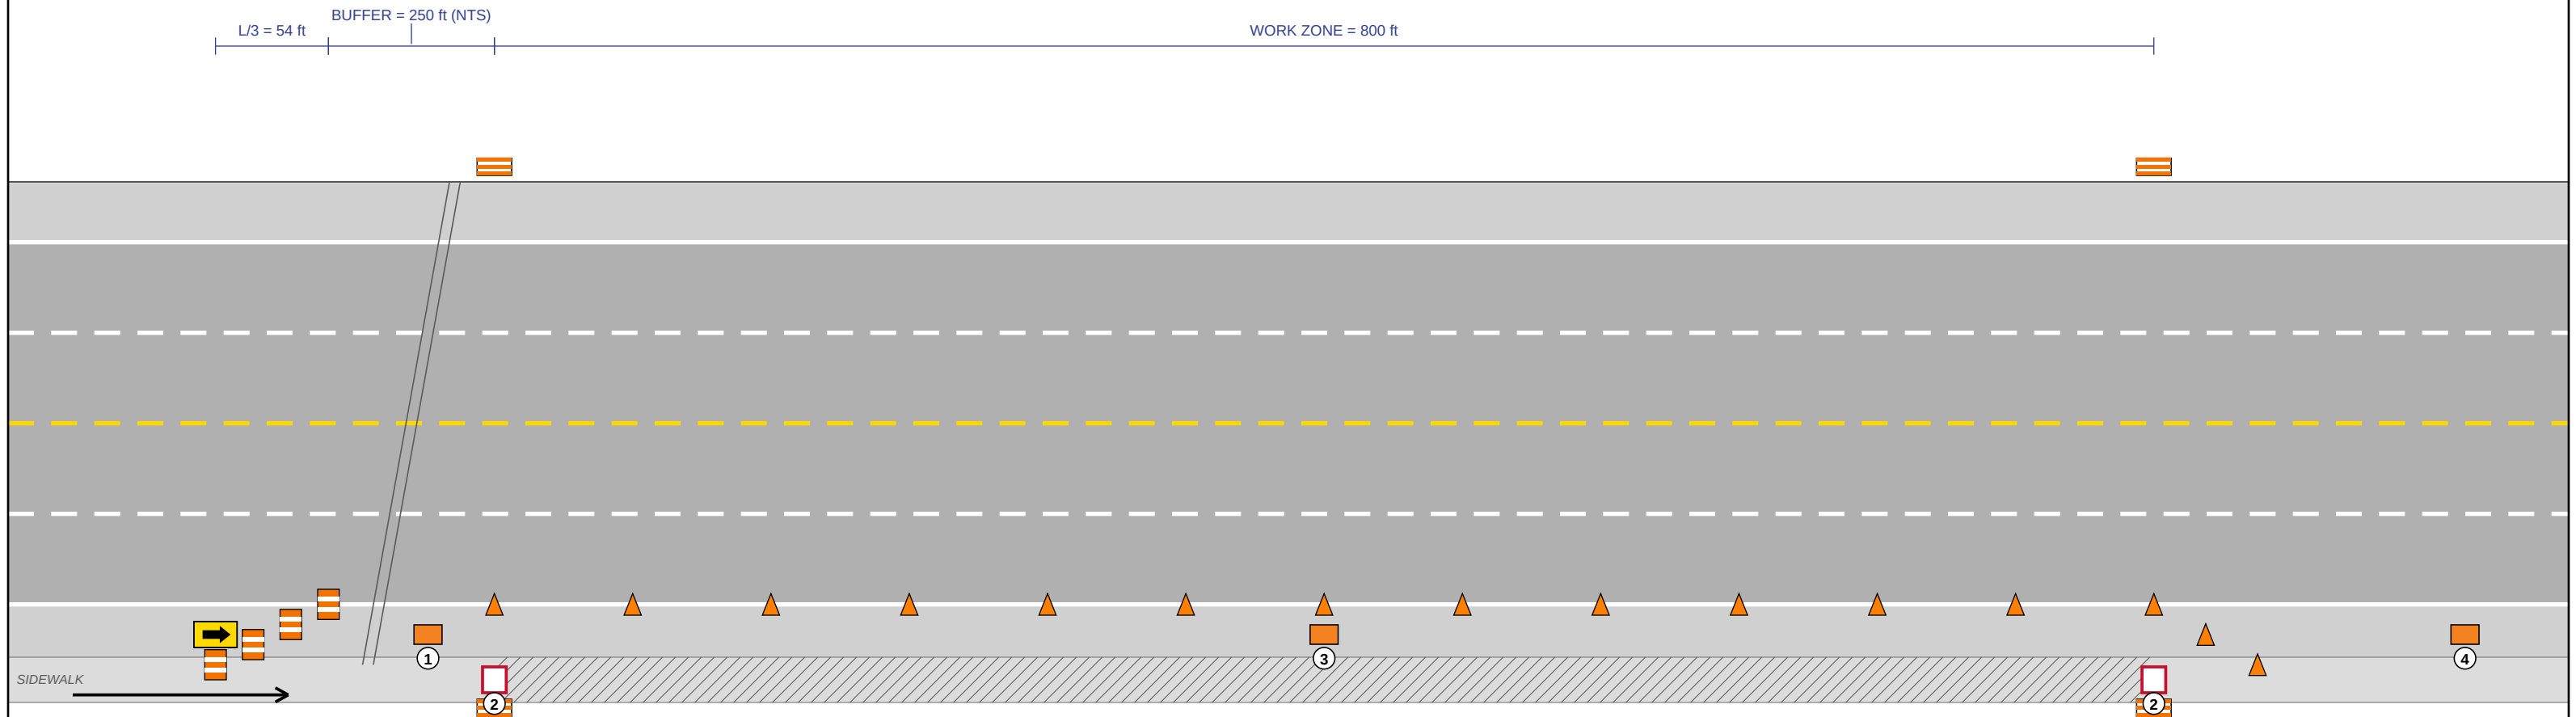

LEGEND

-  Arrow Board
-  Type III Barricade
-  Traffic Cone (28-inch)
-  Channelizing Drum

SIGN CATEGORIES

- | | |
|---|---|
|  | Warning sign (W series, e.g. W20-1) |
|  | Construction guide (G series, e.g. G20-2) |
|  | Regulatory sign (R series, e.g. R9-9) |

SITE CONTEXT

- Sidewalk (hatched within work zone = closed)

Scale 1" = 75 ft applies to the work zone + taper. Buffer compressed; lateral offset exaggerated.

NOTES & SIGN SCHEDULE

PARAMETERS

Speed limit:	35 mph	Closure:	Shoulder Closure
Work zone:	800 ft	Shoulder taper (L/3):	54 ft
Buffer:	250 ft		

SIGN SCHEDULE

#	CODE	DESCRIPTION
1	G20-1	ROAD CONSTRUCTION (NEXT 800 FT)
2	R9-9	SIDEWALK CLOSED
3	G20-5P	CONSTRUCTION ZONE plaque
4	G20-2	END ROAD WORK

ADVANCE WARNING SIGNS (off-page upstream of taper)

CODE	DESCRIPTION	DISTANCE
W21-5aR	RIGHT SHOULDER CLOSED AHEAD	100 FT
W20-2	ROAD WORK 200 FT	200 FT
W20-1	ROAD WORK AHEAD	300 FT

Reference: CDOT S-630-1, MUTCD 11th Ed. Part 6 (effective 2026-01-18), Colorado Supplement.

GENERATED BY CONSTRUCT. DRAFT FOR PE REVIEW. NOT A SEALED PLAN.

Verify all dimensions before use.

TRAFFIC CONTROL DEVICE SUMMARY

MUTCD	DEVICE	QTY
G20-1	ROAD CONSTRUCTION (NEXT 800 FT)	1
G20-2	END ROAD WORK	1
G20-5P	CONSTRUCTION ZONE plaque	1
R9-9	SIDEWALK CLOSED	2
W20-1	ROAD WORK AHEAD	1
W20-2	ROAD WORK 200 FT	1
W21-5aR	RIGHT SHOULDER CLOSED AHEAD	1
—	36-inch channelizing drum with alternating orange/white stripes	4
—	Traffic Cone (28-inch)	15
—	Type III barricade: three horizontal striped rails, full lane width	4
—	Trailer-mounted flashing arrow board (Type A, B, or C)	1

TOTAL DEVICES

32

SEE DEVICE LIST (XLSX) FOR BID QUANTITIES.

PROJECT: Colfax Water Main
LOCATION: E Colfax Ave at Race St
COORDINATES: —

MHT TYPE: SHOULDER CLOSURE · 4-LANE UNDIVIDED
MUTCD: TA-3
CDOT: S-630-1
ORIENTATION: *Site bearing not provided*

SCALE: 1" = 75 ft
DATE: 2026-09-29
SHEET: 1 OF 1

DRAWN BY: MHT Tool (auto-generated)
STATUS: **DRAFT: Not for stamping**