


METHOD OF HANDLING TRAFFIC — 65 MPH

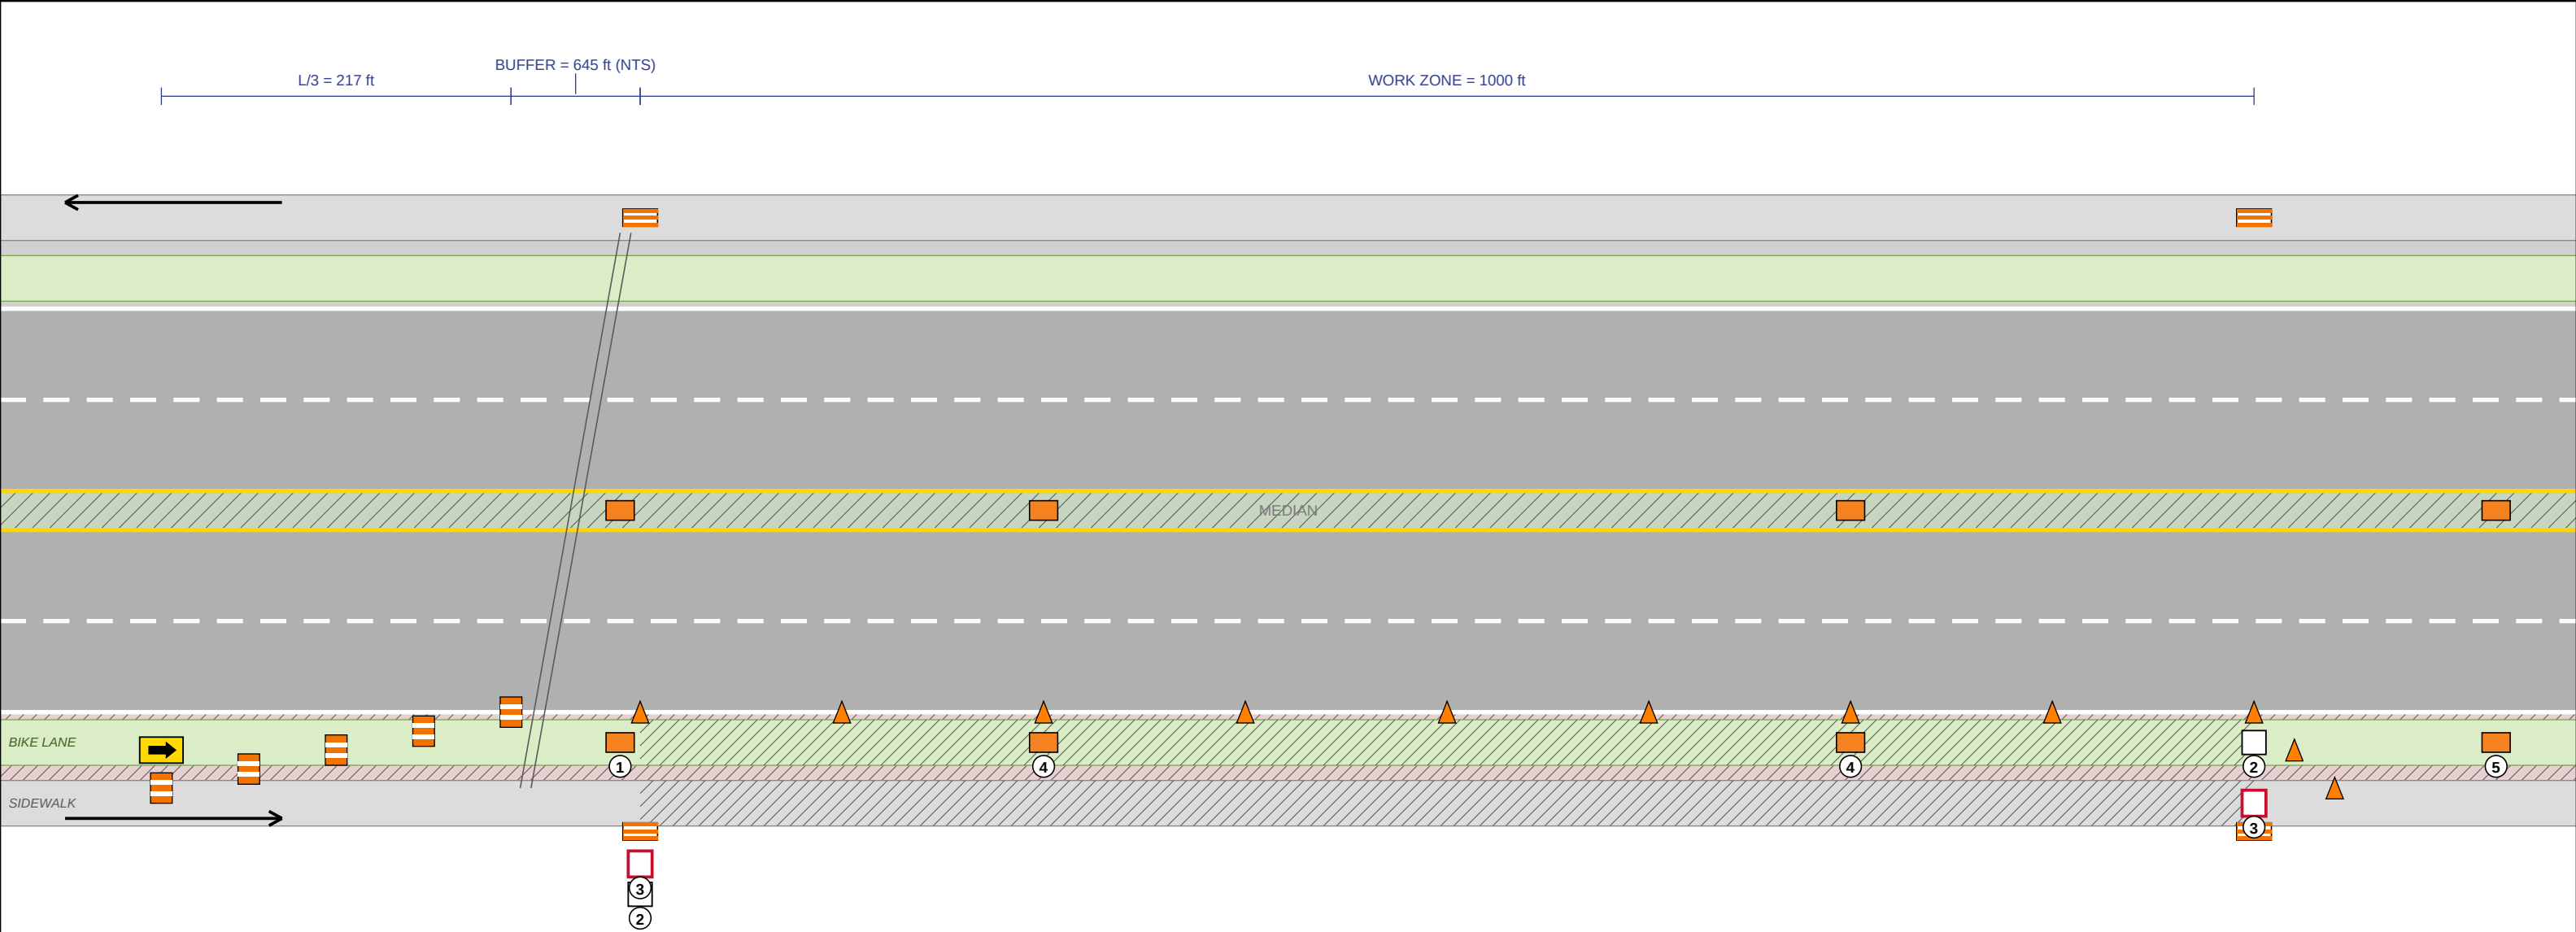

LEGEND

- Arrow Board
- Type III Barricade
- Traffic Cone (36-inch)
- Channelizing Drum
- Warning sign (W series, e.g. W20-1)
- Construction guide (G series, e.g. G20-2)
- Regulatory sign (R series, e.g. R9-9)
- Route guidance (M series, e.g. M4-9a)

+3 MORE — SEE DEVICE LIST (XLSX)

Scale 1" = 97 ft applies to the work zone + taper. Buffer compressed; lateral offset exaggerated.

NOTES & SIGN SCHEDULE

PARAMETERS			
Speed limit:	65 mph	Closure:	Shoulder Closure
Work zone:	1000 ft	Shoulder taper (L/3):	217 ft
Buffer:	645 ft		
SIGN SCHEDULE			
#	CODE	DESCRIPTION	
1	G20-1	ROAD CONSTRUCTION (NEXT 1000 FT)	
2	M4-9a	BIKE DETOUR	
3	R9-9	SIDEWALK CLOSED	
4	G20-5P	CONSTRUCTION ZONE plaque	
5	G20-2	END ROAD WORK	
ADVANCE WARNING SIGNS (off-page upstream of taper)			
CODE	DESCRIPTION		DISTANCE
W21-5aR	RIGHT SHOULDER CLOSED AHEAD		500 ft
W20-2	ROAD WORK 1000 FT		1000 ft
W20-1	ROAD WORK AHEAD		1500 ft

Reference: CDOT S-630-1, MUTCD 11th Ed. Part 6 (effective 2026-01-18), Colorado Supplement.
GENERATED BY CONSTRUCT — DRAFT FOR PE REVIEW. NOT A SEALED PLAN.
Verify all dimensions before use.

TRAFFIC CONTROL DEVICE SUMMARY


MUTCD	DEVICE	QTY
G20-1	ROAD CONSTRUCTION (NEXT 1000 FT)	2
G20-2	END ROAD WORK	2
G20-5P	CONSTRUCTION ZONE plaque	4
M4-9a	BIKE DETOUR	2
R9-9	SIDEWALK CLOSED	2
W20-1	ROAD WORK AHEAD	2
W20-2	ROAD WORK 1000 FT	2
W21-5aR	RIGHT SHOULDER CLOSED AHEAD	2
—	36-inch channelizing drum with alternating orange/white stripes	5
—	Traffic Cone (36-inch)	11
—	Type III barricade — three horizontal striped rails, full lane width	4
—	Trailer-mounted flashing arrow board (Type A, B, or C)	1

TOTAL DEVICES 39

SEE DEVICE LIST (XLSX) FOR BID QUANTITIES.

PROJECT:	Untitled Project
LOCATION:	—
COORDINATES:	39.72690, -104.98730
MHT TYPE:	SHOULDER CLOSURE — DIVIDED HIGHWAY
MUTCD:	TA-3
CDOT:	S-630-1
SCALE:	1" = 97 ft
DATE:	2026-09-08
SHEET:	1 OF 2
AERIAL:	See page 2
DRAWN BY:	MHT Tool (auto-generated)
STATUS:	DRAFT — Not for stamping

AERIAL CONTEXT

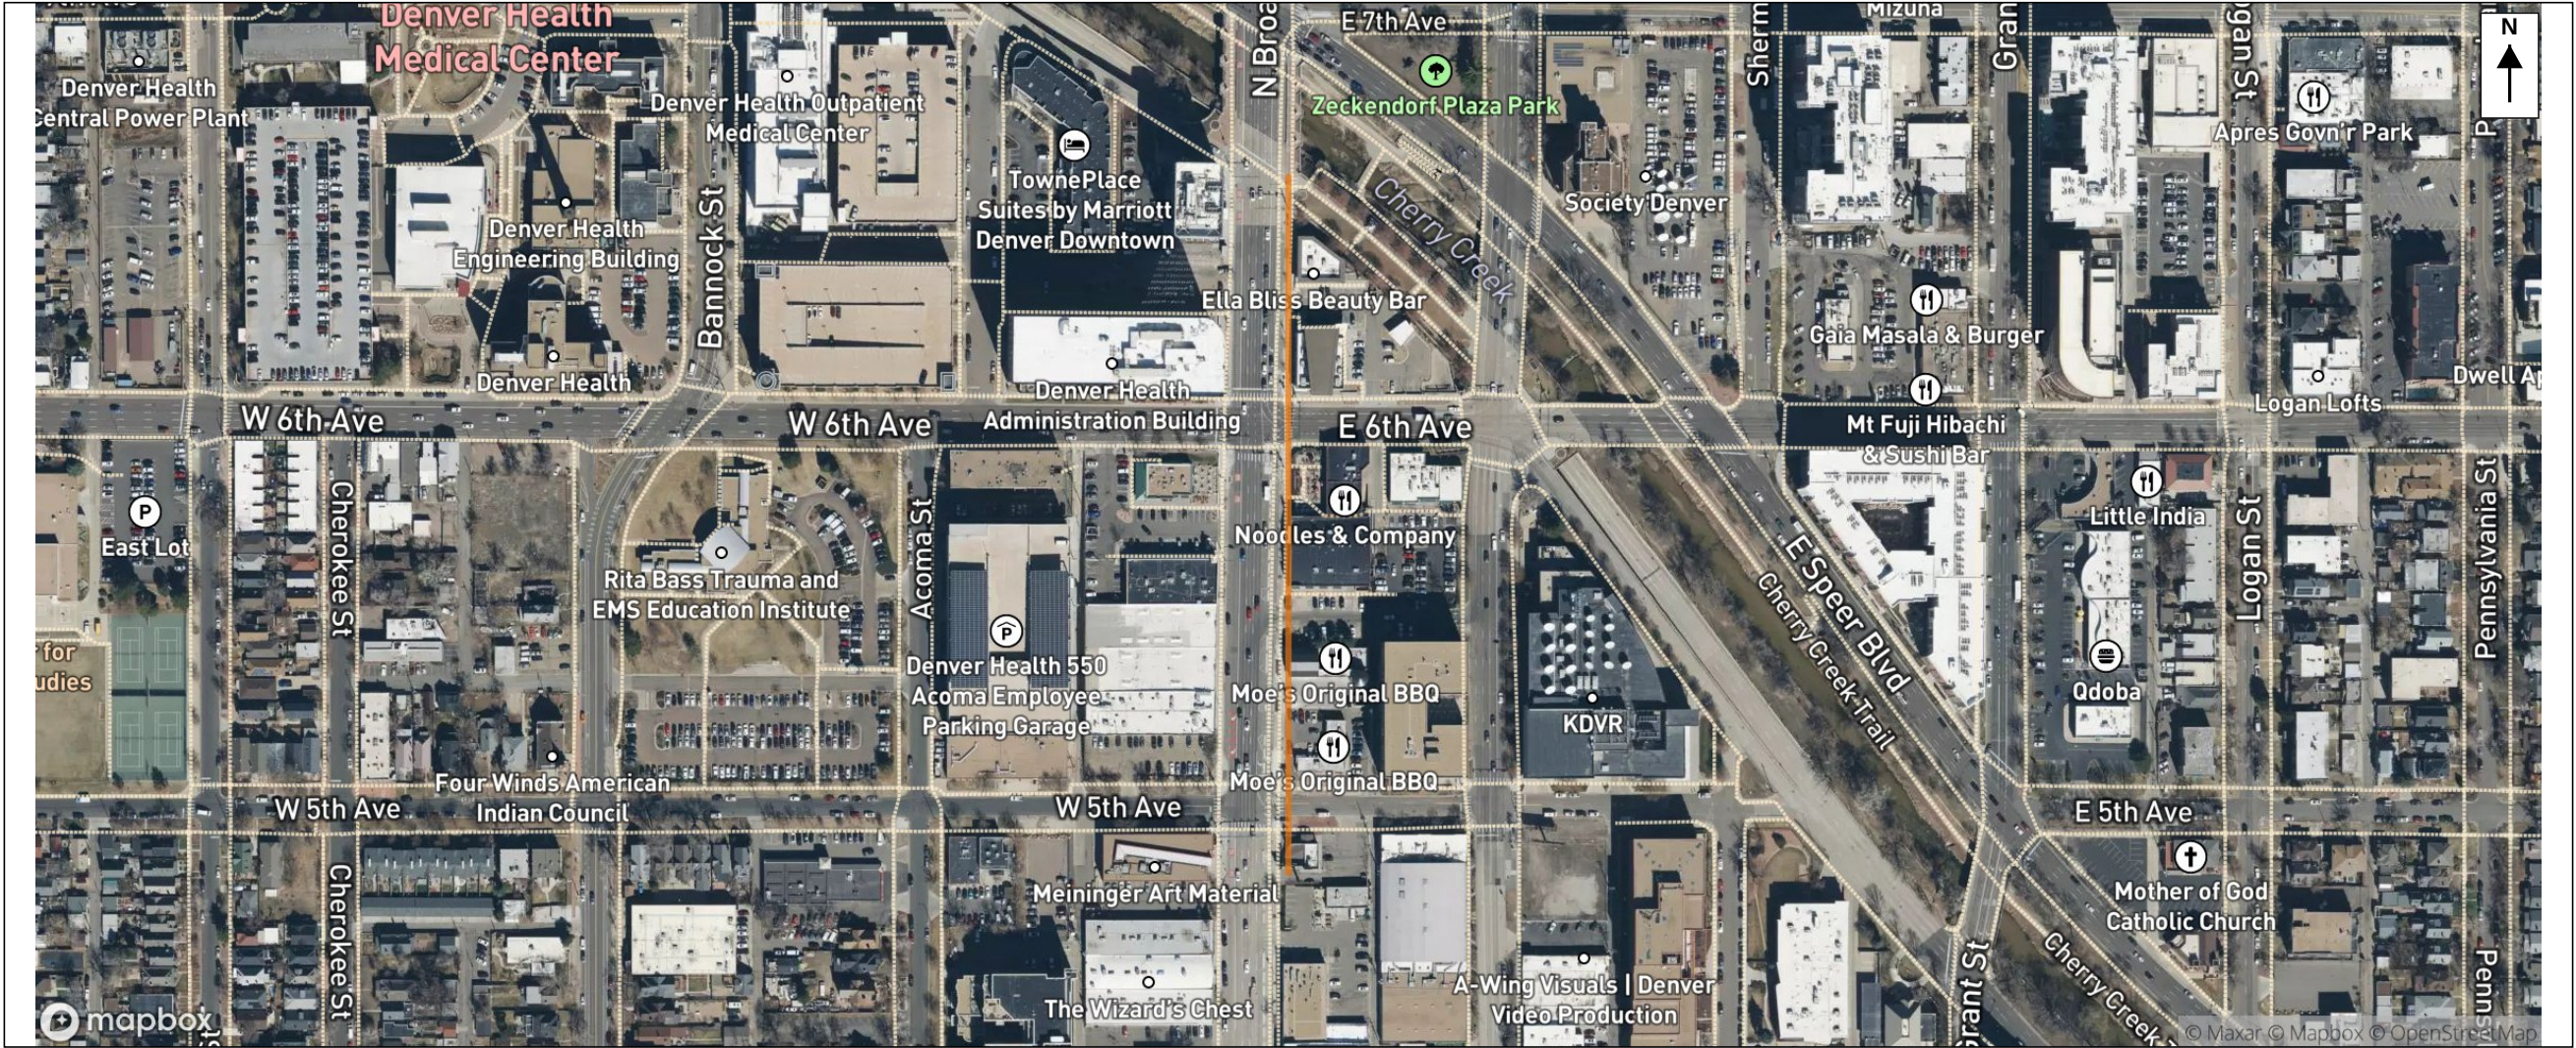

SITE: 39.72690, -104.98730

Work zone (1,000 ft) shown in orange. Advance warning, taper, and buffer not depicted. Mapbox satellite imagery with street labels — for context only. Not a survey product. Verify all field conditions on site.

CORRIDOR DETAILS

Anchor:	39.72690, -104.98730
Bearing:	180°
Total corridor:	3,462 ft (0.66 mi)
Advance warning:	1,500 ft
Taper:	217 ft
Buffer:	645 ft
Work zone:	1,000 ft
Downstream:	100 ft