


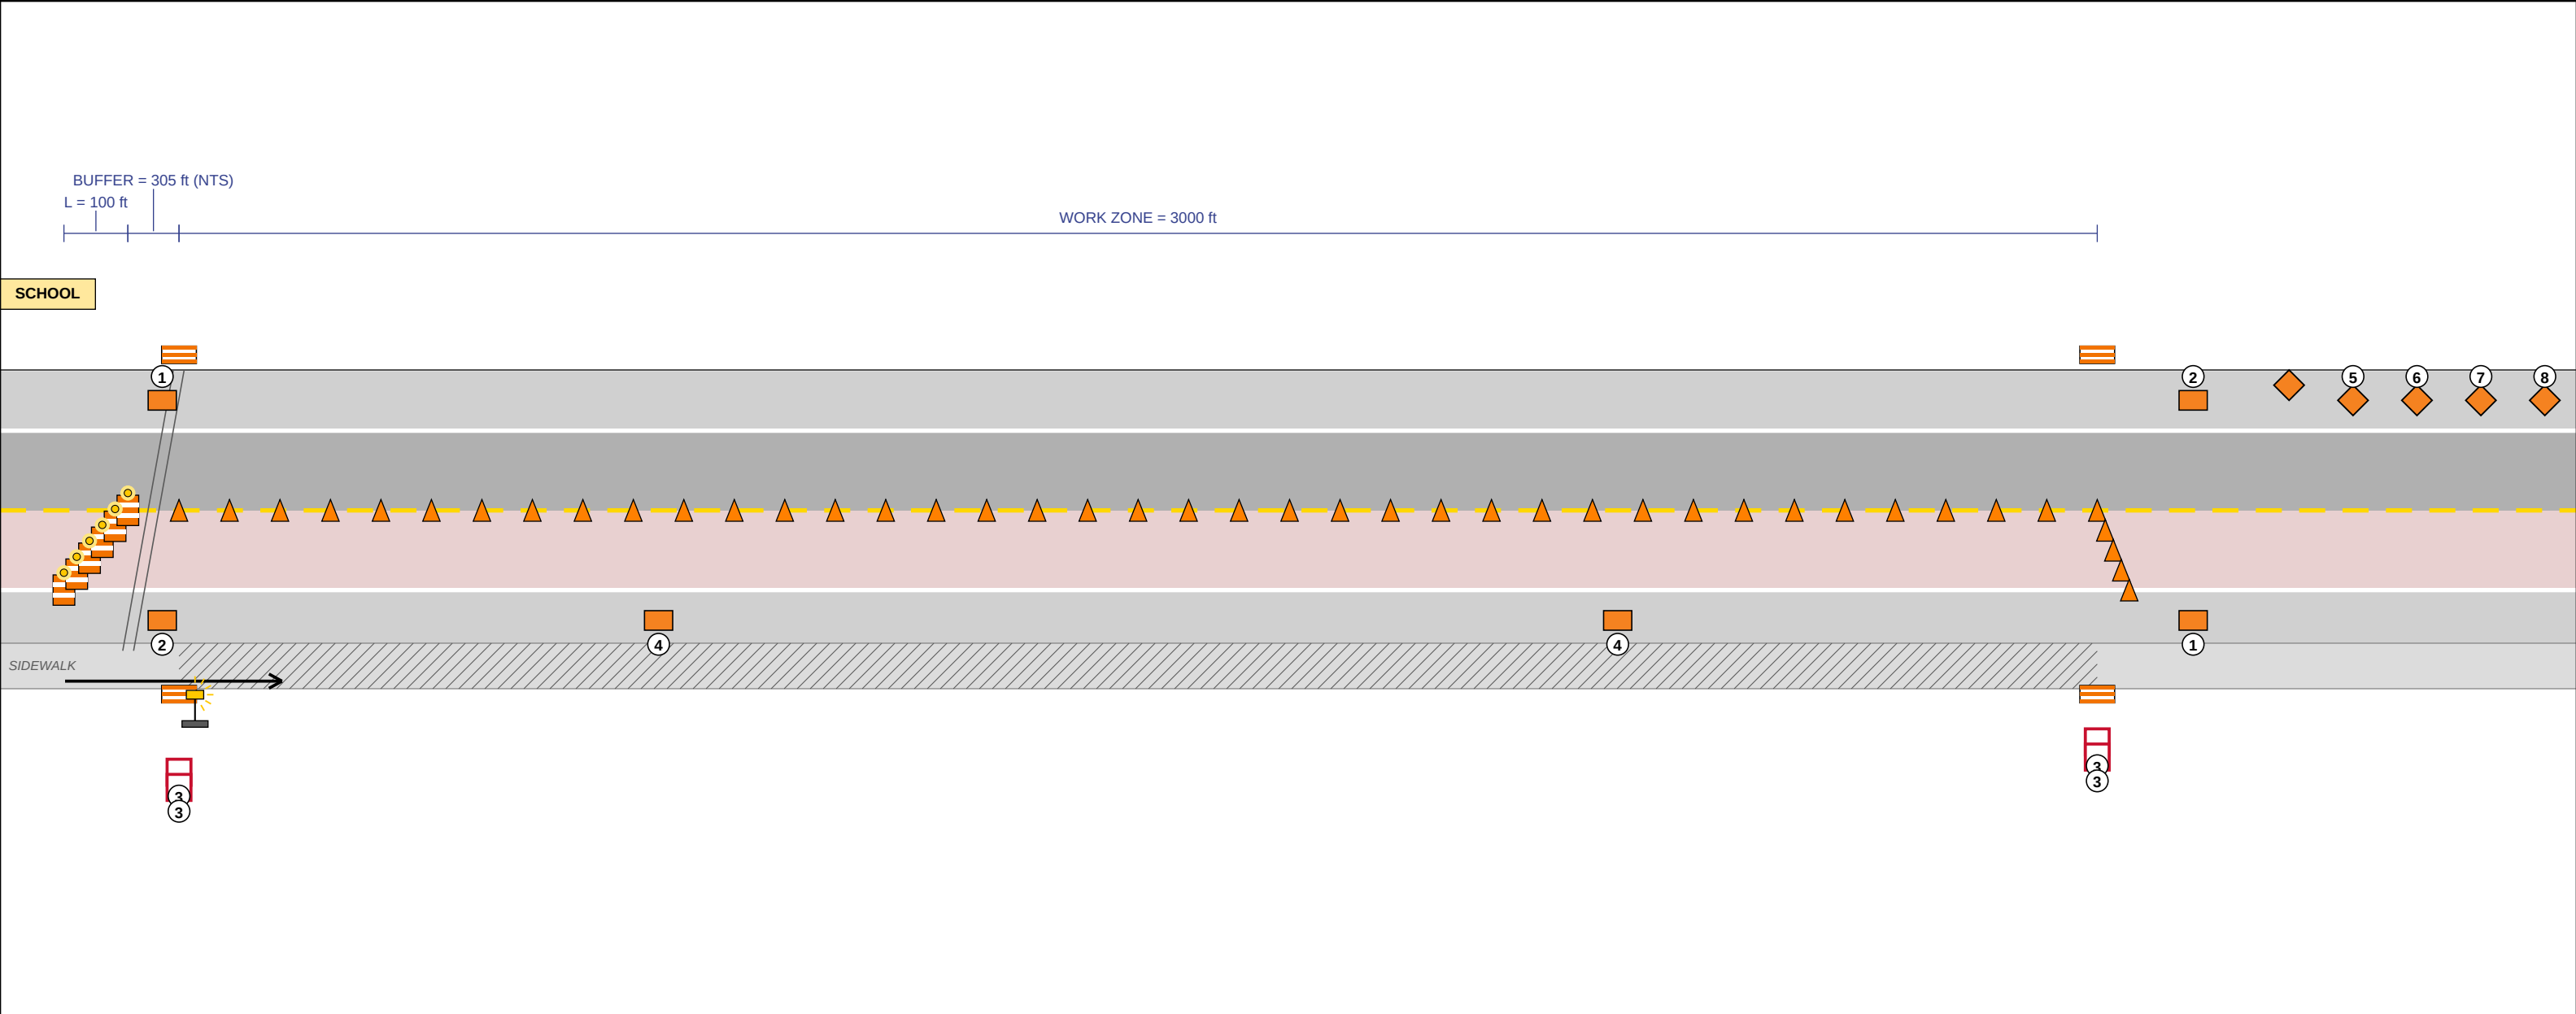

LEGEND

- Type III Barricade
- Traffic Cone (28-inch)
- Channelizing Drum
- Portable Light Plant
- Temporary Signal
- Type C Warning Light (steady)

SIGN CATEGORIES

- Warning sign (W series, e.g. W20-1)
- Construction guide (G series, e.g. G20-2)
- Regulatory sign (R series, e.g. R9-9)
- School sign (S series, e.g. S1-1)

+2 MORE — SEE DEVICE LIST (XLSX)

Scale 1" = 244 ft applies to the work zone + taper. Buffer compressed; lateral offset exaggerated.

NOTES & SIGN SCHEDULE

PARAMETERS			
Speed limit:	40 mph	Closure:	Flagger Alternating Traffic
Work zone:	3000 ft	One-lane two-way taper:	100 ft
Buffer:	305 ft		

SIGN SCHEDULE		
#	CODE	DESCRIPTION
1	G20-2	END ROAD WORK
2	G20-1	ROAD CONSTRUCTION (NEXT 3000 FT)
3	R9-9	SIDEWALK CLOSED
4	G20-5P	CONSTRUCTION ZONE plaque
5	W20-7a	AFAD AHEAD
6	W3-4	BE PREPARED TO STOP
7	W20-4	ONE LANE ROAD AHEAD
8	W20-1	ROAD WORK AHEAD

ADVANCE WARNING SIGNS & FLAGGER STATIONS (off-page upstream of taper)					
CODE	DESCRIPTION	DISTANCE	CODE	DESCRIPTION	DISTANCE
—	AFAD #1 (APPROACH)	100 ft	W20-7a	AFAD AHEAD	200 ft
+4 MORE ADVANCE SIGNS — SEE CREW NARRATIVE & DEVICE LIST					

Reference: CDOT S-630-1, MUTCD 11th Ed. Part 6 (effective 2026-01-18), Colorado Supplement.
† MINIMUM TRAVEL LANE WIDTH — Both current, both Littleton. Plausible reconciliation (flagger closures carry two-way traffic through one lane) not adopted; render 10 ft general, 12 ft on flagger configurations. (LEDS §131 (2025): 10 ft; One/Two/Three Flagger Closure templates: Minimum 12 ft travel lane must be maintained at all times)
GENERATED BY CONSTRUCT — DRAFT FOR PE REVIEW. NOT A SEALED PLAN.
Verify all dimensions before use.

TRAFFIC CONTROL DEVICE SUMMARY

MUTCD	DEVICE	QTY
G20-1	ROAD CONSTRUCTION (NEXT 3000 FT)	2
G20-2	END ROAD WORK	2
G20-5P	CONSTRUCTION ZONE plaque	2
R9-9	SIDEWALK CLOSED	4
S1-1	SCHOOL	2
W20-1	ROAD WORK AHEAD	2
W20-4	ONE LANE ROAD AHEAD	2
W20-7a	AFAD AHEAD	2
W3-4	BE PREPARED TO STOP	2
—	36-inch channelizing drum with alternating orange/white stripes	6
—	Traffic Cone (28-inch)	43
—	Type C steady-burn warning light, attached to channelizing d...	6
—	Type III barricade — three horizontal striped rails, full lane width	4
—	Portable light plant for work area illumination	1
—	Portable traffic signal (standard, compact, AFAD, or RDTs)	2

TOTAL DEVICES 82

SEE DEVICE LIST (XLSX) FOR BID QUANTITIES.

PROJECT:	I-25 & Alameda Interchange Phase 3B Utility Relocation and Storm Drain Improvements Pa...
LOCATION:	4700-4998 South Colorado Boulevard between East Bayaud Avenue and East Alameda Aven...
COORDINATES:	—
MHT TYPE:	FLAGGER ALTERNATING TRAFFIC — 2-LANE UNDIVIDED
MUTCD:	TA-10
CDOT:	S-630-1
ORIENTATION:	Site bearing not provided
SCALE:	1" = 244 ft
DATE:	2026-08-22
SHEET:	1 OF 1
DRAWN BY:	MHT Tool (auto-generated)
STATUS:	DRAFT — Not for stamping