


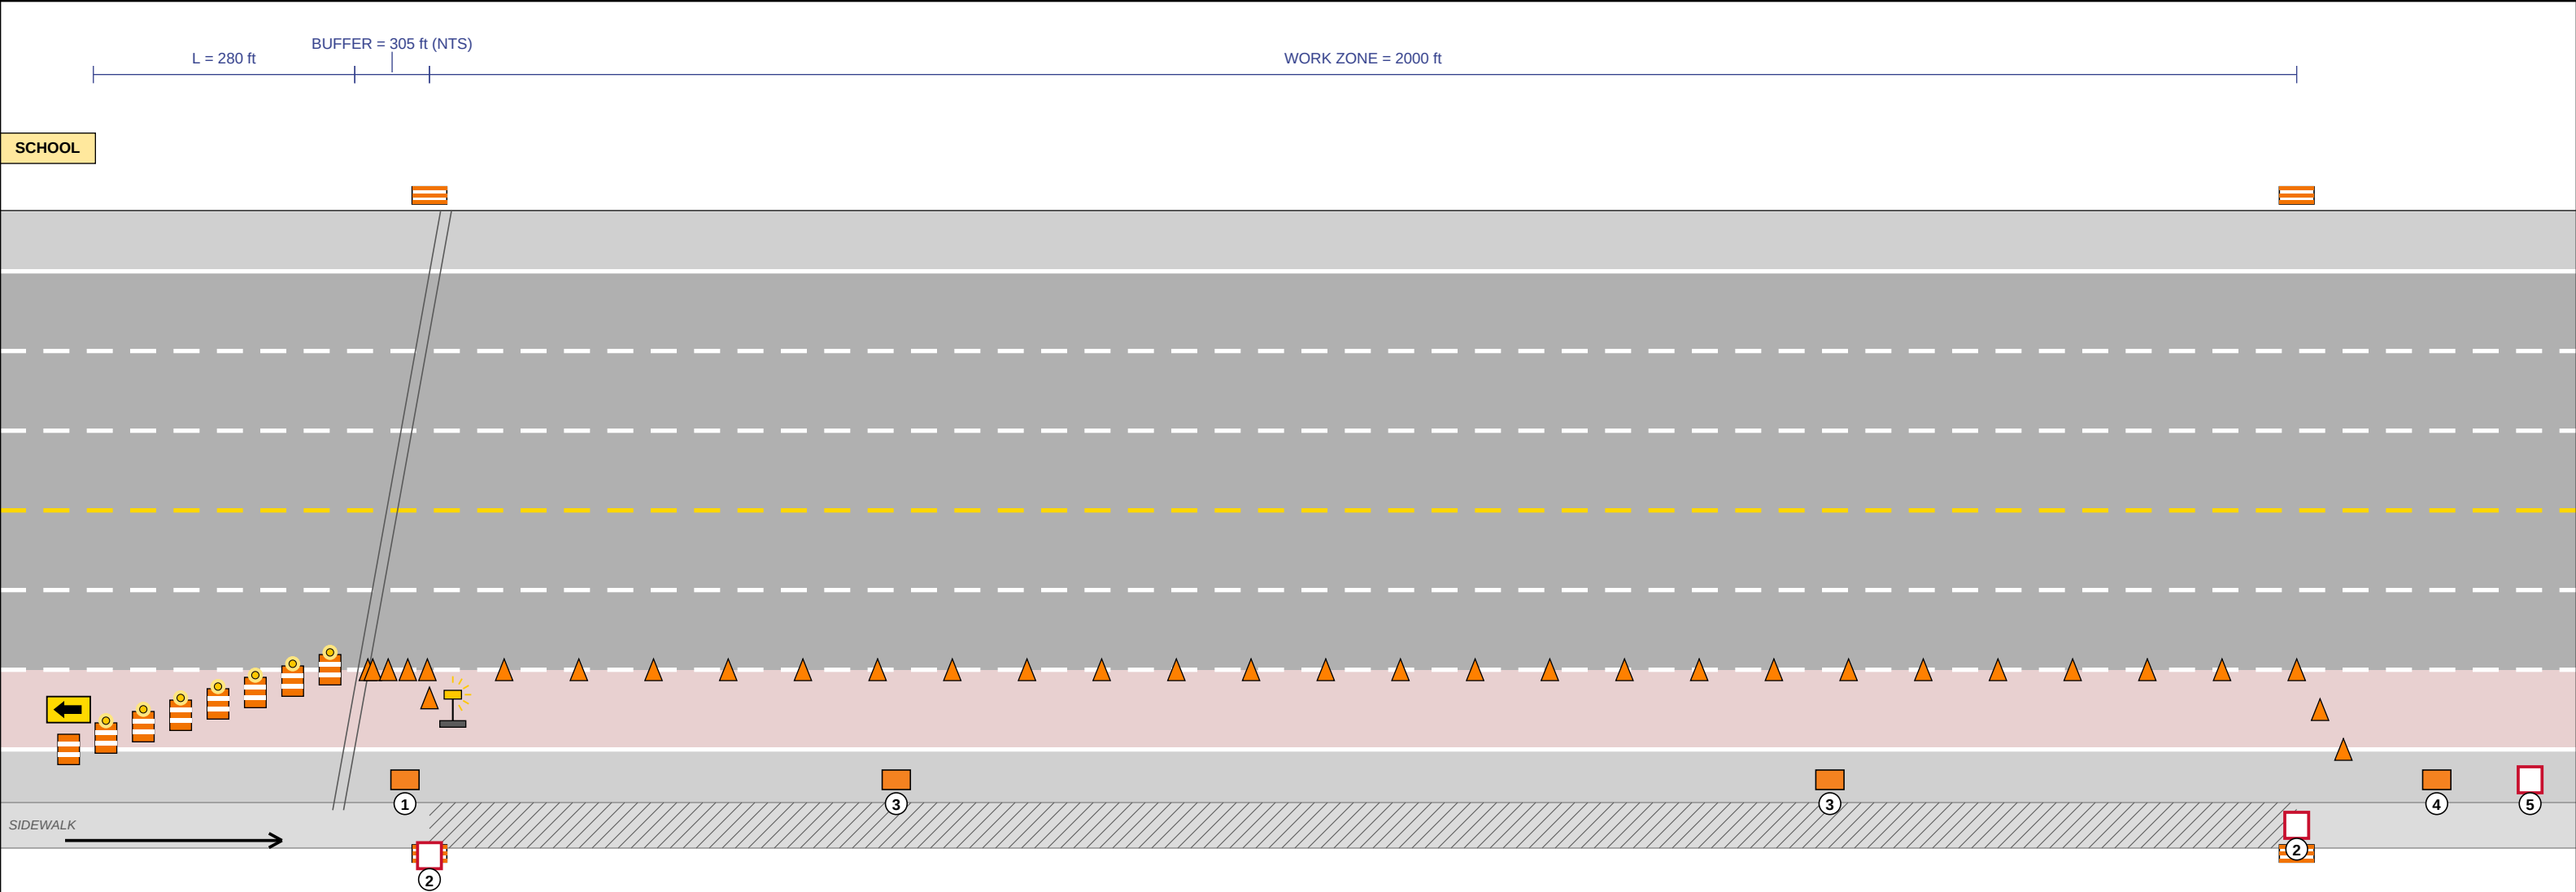

LEGEND

- Arrow Board
- Type III Barricade
- Traffic Cone (28-inch)
- Channelizing Drum
- Portable Light Plant
- Type C Warning Light (steady)

SIGN CATEGORIES

- Warning sign (W series, e.g. W20-1)
- Construction guide (G series, e.g. G20-2)
- Regulatory sign (R series, e.g. R9-9)
- School sign (S series, e.g. S1-1)

+2 MORE — SEE DEVICE LIST (XLSX)

Scale 1" = 167 ft applies to the work zone + taper. Buffer compressed; lateral offset exaggerated.

NOTES & SIGN SCHEDULE

PARAMETERS			
Speed limit:	40 mph	Closure:	Lane Closure Near Intersection
Work zone:	2000 ft	Lane taper (L):	280 ft
Buffer:	305 ft		

SIGN SCHEDULE		DESCRIPTION
#	CODE	
1	G20-1	ROAD CONSTRUCTION (NEXT 2000 FT)
+4 MORE SIGNS — SEE DEVICE LIST (XLSX)		

ADVANCE WARNING SIGNS (off-page upstream of taper)			
CODE	DESCRIPTION	DISTANCE	CODE
+5 MORE ADVANCE SIGNS — SEE CREW NARRATIVE & DEVICE LIST			

Reference: CDOT S-630-1, MUTCD 11th Ed. Part 6 (effective 2026-01-18), Colorado Supplement.
† TC PERMIT LEAD TIME — Handout may state processing time vs. the page's advance-notice ask; render 10 until the city clarifies. (Thornton ROW page: 10 business days minimum (5 if no construction permit); Construction & TC Permit handout: processed 2 business days (5 with street closure))
CROSS-STREET CONTROL PER CDOT S-630-1 SHEET 10, CASES 18/19 — NOT DRAWN. SEE DEVICE LIST, CREW NARRATIVE, AND AUDIT.
Plate typifies corner-quadrant work with a cross-street closure train; this plan places advance sets only (corner work tracked at issue #128).
Opposing mainline direction not signed (undivided single-side convention; the plate signs both directions).
Plate typifies rural sign placement; urban applications require block-based placement (Sheet 10 Note 1).
CLOSED LANE DRAWN AS THE RIGHTMOST LANE — MODELING ASSUMPTION; NO MUTCD RULE SELECTS THE LANE (THE WORK LOCATION DOES). IF THE WORK OCCUPIES A DIFFERENT LANE, THIS PLAN DOES NOT APPLY AS DRAWN.
GENERATED BY CONSTRUCT — DRAFT FOR PE REVIEW. NOT A SEALED PLAN.
Verify all dimensions before use.

TRAFFIC CONTROL DEVICE SUMMARY

MUTCD	DEVICE	QTY
G20-1	ROAD CONSTRUCTION (NEXT 2000 FT)	1
G20-2	END ROAD WORK	1
G20-5P	CONSTRUCTION ZONE plaque	2
R2-10	BEGIN DOUBLE FINES ZONE	1
R2-11	END DOUBLE FINES ZONE	1
R9-9	SIDEWALK CLOSED	2
S1-1	SCHOOL	2
W20-1	ROAD WORK AHEAD	1
W20-5R	RIGHT LANE CLOSED AHEAD	1
W4-2R	RIGHT LANE ENDS	1
—	36-inch channelizing drum with alternating orange/white stripes	8
—	Traffic Cone (28-inch)	33
—	Type C steady-burn warning light, attached to channelizing d...	7
—	Type III barricade — three horizontal striped rails, full lane width	4
—	Trailer-mounted flashing arrow board (Type A, B, or C)	1
—	Portable light plant for work area illumination	1
—	Advance Warning Signs	1

TOTAL DEVICES 68

SEE DEVICE LIST (XLSX) FOR BID QUANTITIES.

PROJECT:	I-25 & Alameda Interchange Phase 3B Utility Relocation and Storm Drain Improvements Pa...
LOCATION:	4700-4998 South Colorado Boulevard between East Bayaud Avenue and East Alameda Aven...
COORDINATES:	—
MHT TYPE:	LANE CLOSURE NEAR INTERSECTION — UNDIVIDED
MUTCD:	TA-22
CDOT:	S-630-1
ORIENTATION:	Site bearing not provided
SCALE:	1" = 167 ft
DATE:	2026-08-22
SHEET:	1 OF 1
DRAWN BY:	MHT Tool (auto-generated)
STATUS:	DRAFT — Not for stamping