


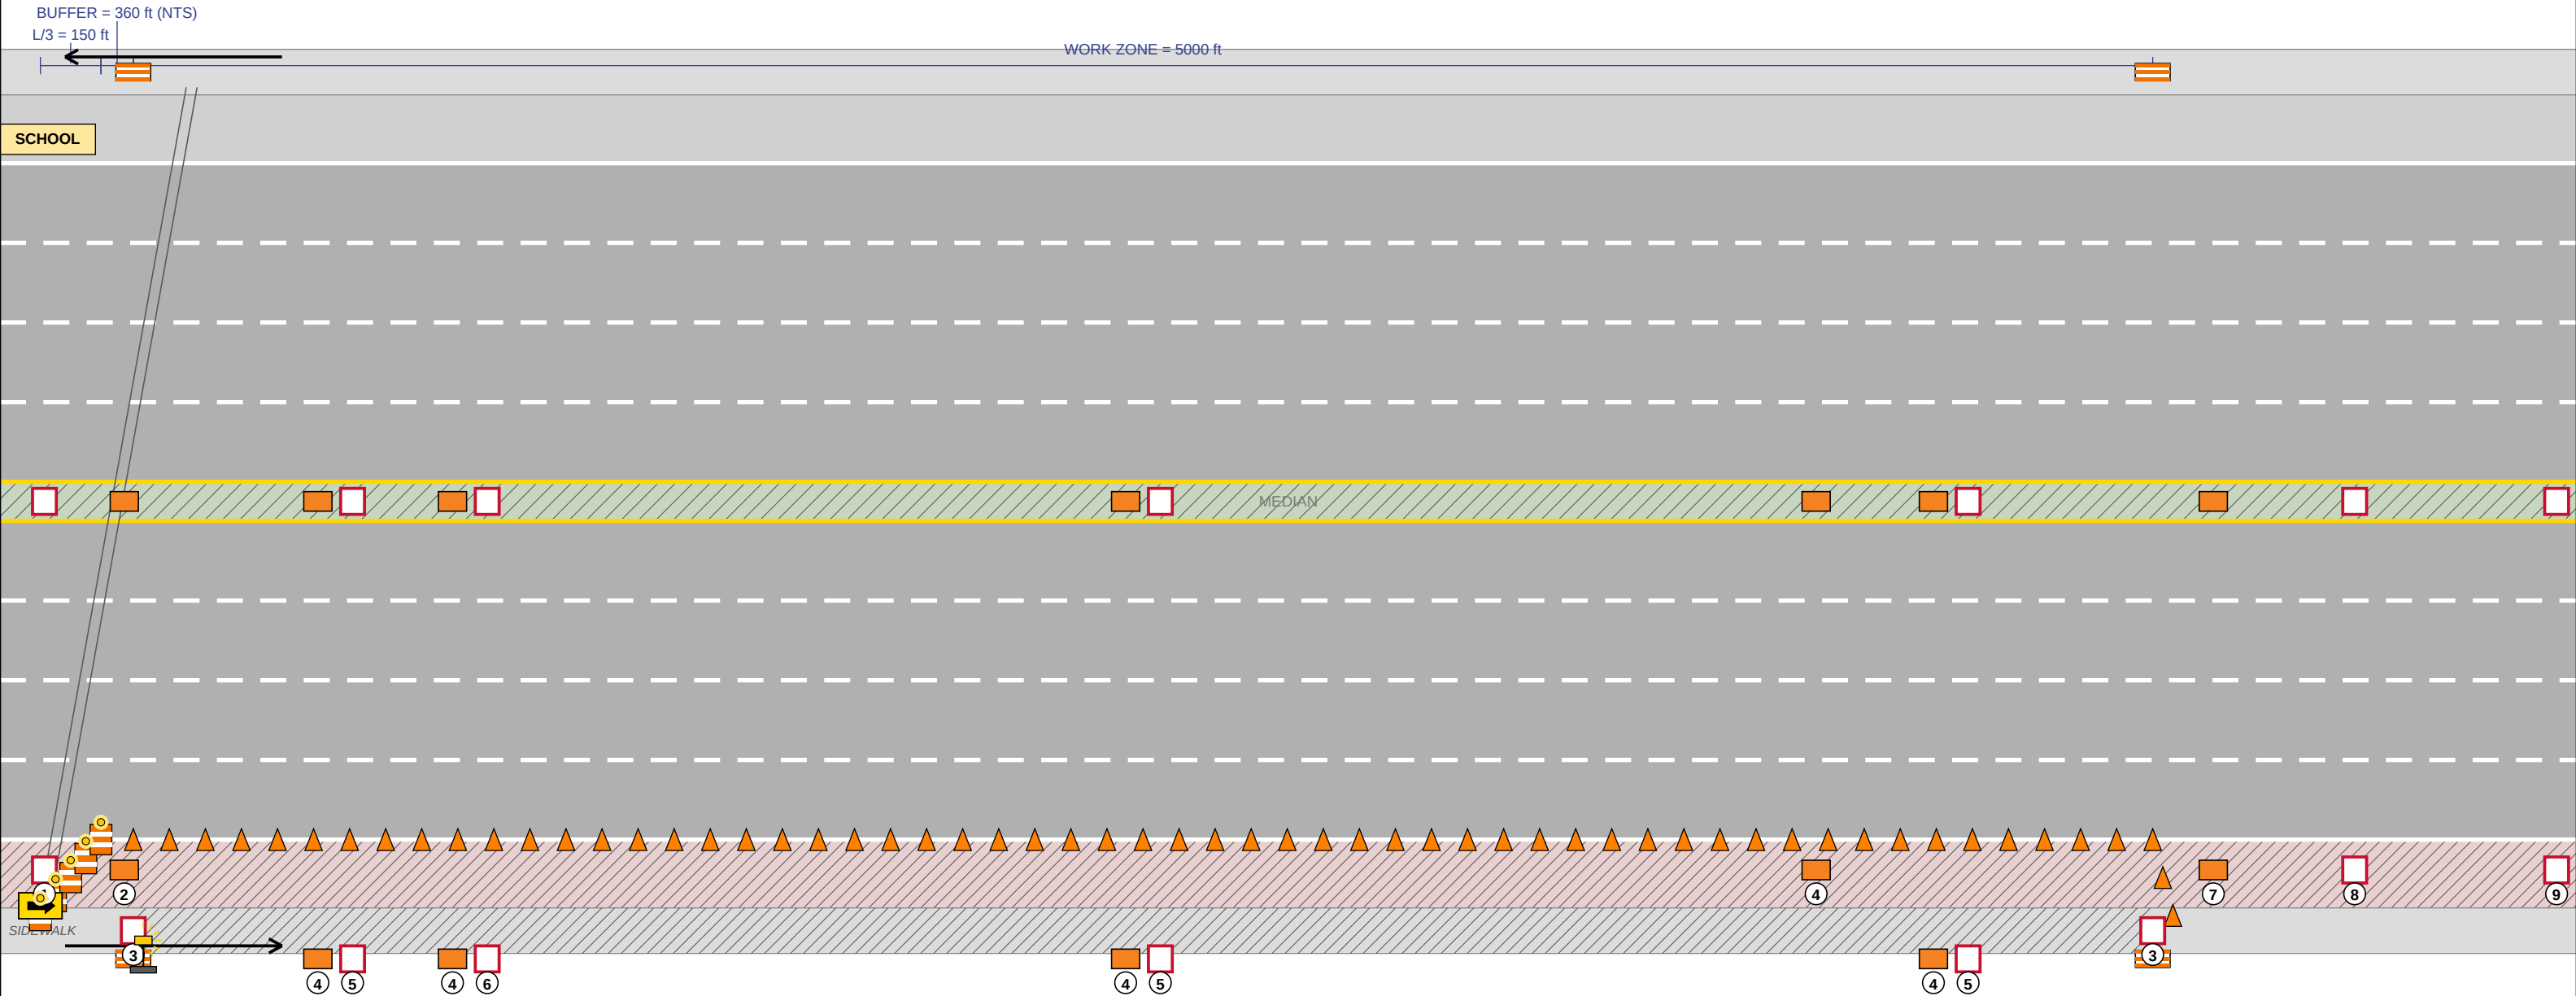

LEGEND

- Arrow Board
- Type III Barricade
- Traffic Cone (36-inch)
- Channelizing Drum
- Portable Light Plant
- Type C Warning Light (steady)

SIGN CATEGORIES

- Warning sign (W series, e.g. W20-1)
- Construction guide (G series, e.g. G20-2)
- Regulatory sign (R series, e.g. R9-9)
- School sign (S series, e.g. S1-1)

+3 MORE — SEE DEVICE LIST (XLSX)

Scale 1" = 387 ft applies to the work zone + taper. Buffer compressed; lateral offset exaggerated.

NOTES & SIGN SCHEDULE

PARAMETERS

Speed limit:	45 mph	Closure:	Shoulder Closure
Work zone:	5000 ft	Shoulder taper (L/3):	150 ft
Buffer:	360 ft		

SIGN SCHEDULE

#	CODE	DESCRIPTION
1	R2-10	BEGIN DOUBLE FINES ZONE
2	G20-1	ROAD CONSTRUCTION (NEXT 5000 FT)
3	R9-9	SIDEWALK CLOSED

+6 MORE SIGNS — SEE DEVICE LIST (XLSX)

ADVANCE WARNING SIGNS (off-page upstream of taper)

CODE	DESCRIPTION	DISTANCE	CODE	DESCRIPTION	DISTANCE
------	-------------	----------	------	-------------	----------

+6 MORE ADVANCE SIGNS — SEE CREW NARRATIVE & DEVICE LIST

Reference: CDOT S-630-1, MUTCD 11th Ed. Part 6 (effective 2026-01-18), Colorado Supplement.
† OVERNIGHT EXCAVATIONS — Render the prohibition; the flashing-barricade rule applies only under a written Engineer exception (Q-ENG-3). (ROW Permits Guide, Gen. Cond. §6: All work properly backfilled prior to end of workday; no open holes or plates overnight; 2020 Standards §3.2.8.2: When excavations must remain open overnight: properly marked, flashing barricades unless the...
† ARTERIAL LANE-CLOSURE REOPEN TIME — Rendering the 3:00 p.m. reopen per TC-1 (conservative); the statute alone would allow until 3:30 (Q-ENG-9, narrowed to this half hour). (TC-1 note T06 (2020, adopted by EMC 11-7-25): 9 a.m.–3 p.m., all lanes re-opened by 3 p.m.; EMC 11-7-14(D): peak ban resumes at 3:30 p.m.)
† TCS: REQUIRED OR ENCOURAGED — Precedence leans hard toward REQUIRED: TC-1 sits inside a document adopted into the municipal code; the softer wording is guidance beneath it. Open: what 'or be available' means (Q-ENG-8). (TC-1 T04 (2020 drawings, adopted by EMC 11-7-25): TCS shall be present on site (or be available) at all times; 2020 Standards §2.2.2.5 / ROW Permits Guide...
GENERATED BY CONSTRUCT — DRAFT FOR PE REVIEW. NOT A SEALED PLAN.
Verify all dimensions before use.

TRAFFIC CONTROL DEVICE SUMMARY

MUTCD	DEVICE	QTY
G20-1	ROAD CONSTRUCTION (NEXT 5000 FT)	2
G20-2	END ROAD WORK	2
G20-5P	CONSTRUCTION ZONE plaque	10
R2-10	BEGIN DOUBLE FINES ZONE	2
R2-11	END DOUBLE FINES ZONE	2
R2-1	SPEED LIMIT 25 (work-zone speed posting)	2
R2-1	SPEED LIMIT 45 (posted-speed restoration)	2
R2-6P	FINES DOUBLE plaque	6
R9-9	SIDEWALK CLOSED	2
S1-1	SCHOOL	2
W20-1	ROAD WORK AHEAD	2
W20-2	ROAD WORK 700 FT	2
W21-5aR	RIGHT SHOULDER CLOSED AHEAD	2
W3-5	ADVISORY SPEED 25	2
W3-5	ADVISORY SPEED 30	2
—	36-inch channelizing drum with alternating orange/white stripes	5
—	Traffic Cone (36-inch)	59
+4 MORE TYPES — SEE DEVICE LIST (XLSX)		

TOTAL DEVICES

117

SEE DEVICE LIST (XLSX) FOR BID QUANTITIES.

PROJECT:	I-25 & Alameda Interchange Phase 3B Utility Relocation and Storm Drain Improvements Pa...
LOCATION:	4700-4998 South Colorado Boulevard between East Bayaud Avenue and East Alameda Aven...
COORDINATES:	—
MHT TYPE:	SHOULDER CLOSURE — DIVIDED HIGHWAY
MUTCD:	TA-3
CDOT:	S-630-1
ORIENTATION:	Site bearing not provided

SCALE:	1" = 387 ft
DATE:	2026-08-22
SHEET:	1 OF 1

DRAWN BY:	MHT Tool (auto-generated)
STATUS:	DRAFT — Not for stamping