


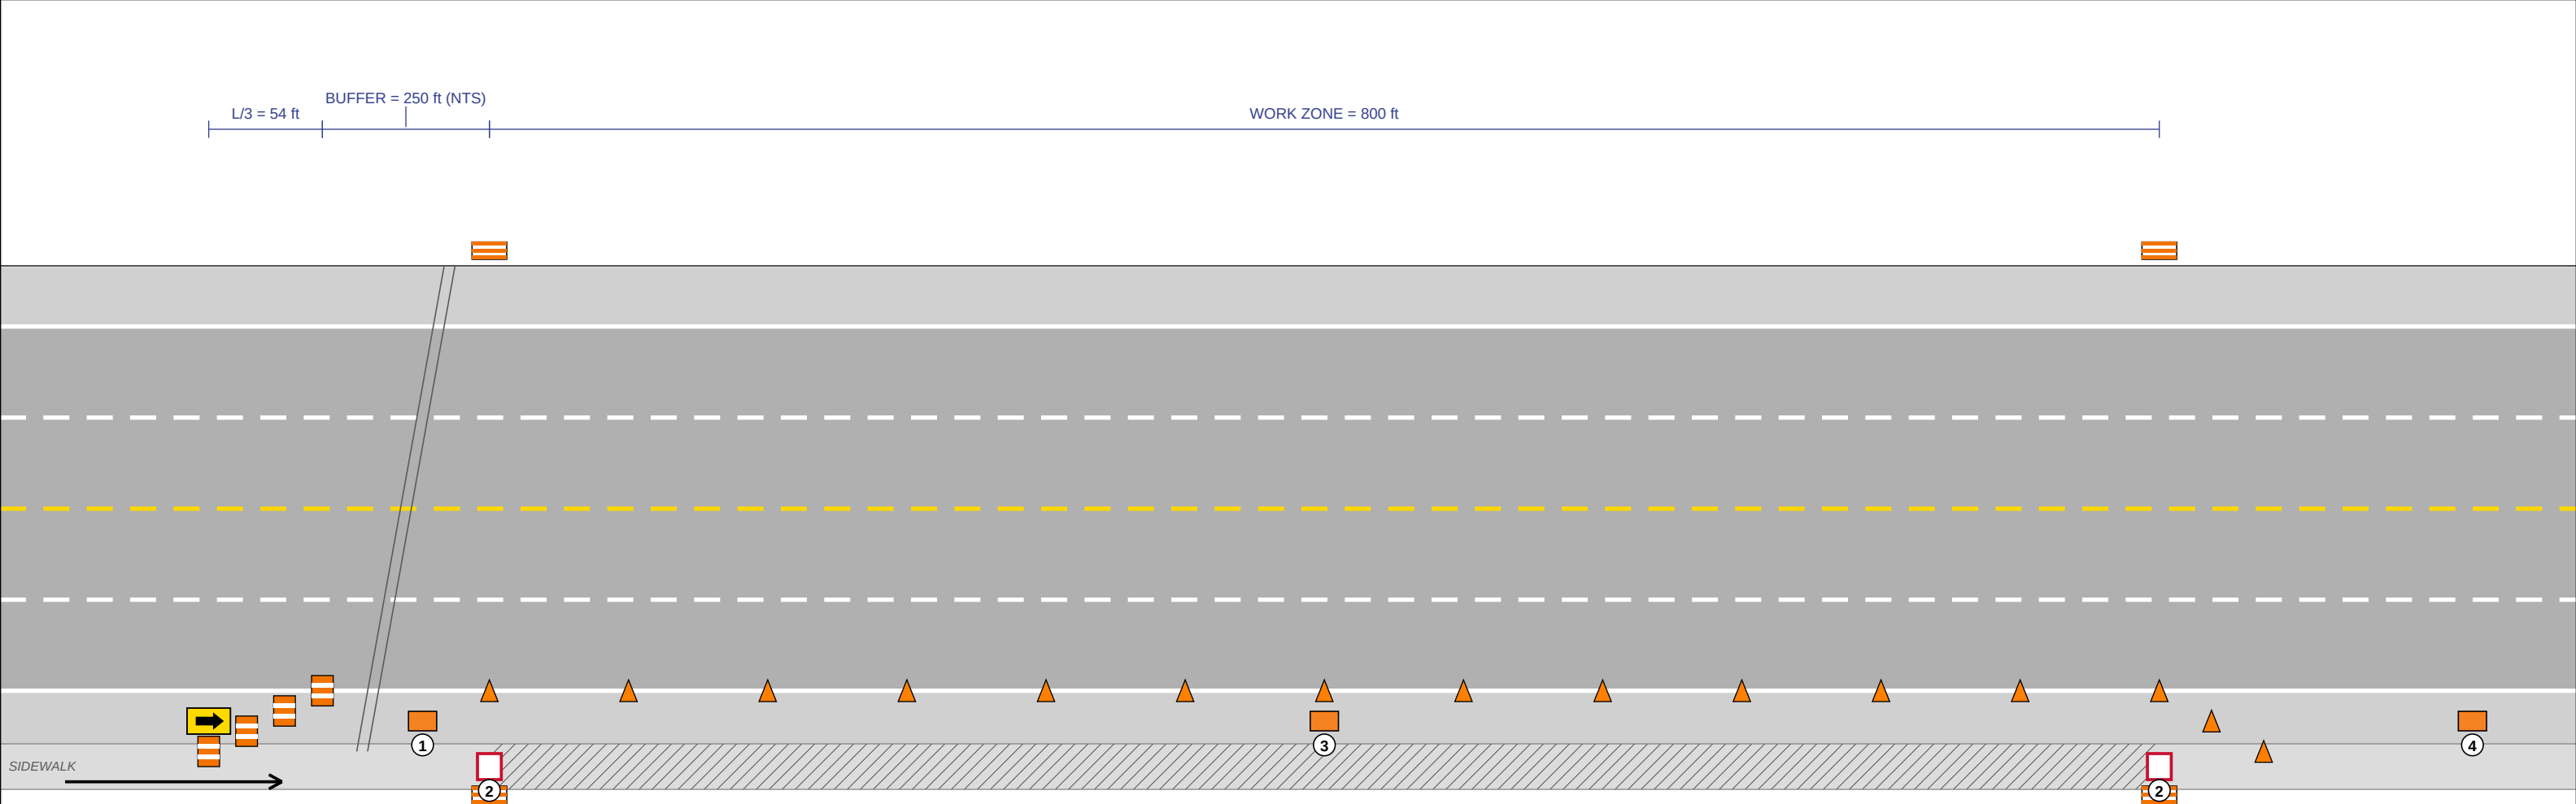

LEGEND

- Arrow Board
- Type III Barricade
- Traffic Cone (28-inch)
- Channelizing Drum
- SIGN CATEGORIES**
- Warning sign (W series, e.g. W20-1)
- Construction guide (G series, e.g. G20-2)
- Regulatory sign (R series, e.g. R9-9)

SITE CONTEXT

- Sidewalk (hatched within work zone = closed)

Scale 1" = 75 ft applies to the work zone + taper. Buffer compressed; lateral offset exaggerated.

NOTES & SIGN SCHEDULE

PARAMETERS			
Speed limit:	35 mph	Closure:	Shoulder Closure
Work zone:	800 ft	Shoulder taper (L/3):	54 ft
Buffer:	250 ft		

SIGN SCHEDULE		
#	CODE	DESCRIPTION
1	G20-1	ROAD CONSTRUCTION (NEXT 800 FT)
2	R9-9	SIDEWALK CLOSED
3	G20-5P	CONSTRUCTION ZONE plaque
4	G20-2	END ROAD WORK

ADVANCE WARNING SIGNS (off-page upstream of taper)		
CODE	DESCRIPTION	DISTANCE
W21-5aR	RIGHT SHOULDER CLOSED AHEAD	100 ft
W20-2	ROAD WORK 200 FT	200 ft
W20-1	ROAD WORK AHEAD	300 ft

Reference: CDOT S-630-1, MUTCD 11th Ed. Part 6 (effective 2026-01-18), Colorado Supplement.
GENERATED BY CONESTRUCT — DRAFT FOR PE REVIEW. NOT A SEALED PLAN.
Verify all dimensions before use.

TRAFFIC CONTROL DEVICE SUMMARY

MUTCD	DEVICE	QTY
G20-1	ROAD CONSTRUCTION (NEXT 800 FT)	1
G20-2	END ROAD WORK	1
G20-5P	CONSTRUCTION ZONE plaque	1
R9-9	SIDEWALK CLOSED	2
W20-1	ROAD WORK AHEAD	1
W20-2	ROAD WORK 200 FT	1
W21-5aR	RIGHT SHOULDER CLOSED AHEAD	1
—	36-inch channelizing drum with alternating orange/white stripes	4
—	Traffic Cone (28-inch)	15
—	Type III barricade — three horizontal striped rails, full lane width	4
—	Trailer-mounted flashing arrow board (Type A, B, or C)	1

TOTAL DEVICES 32

SEE DEVICE LIST (XLSX) FOR BID QUANTITIES.

PROJECT: Colfax Water Main
LOCATION: E Colfax Ave at Race St
COORDINATES: —

MHT TYPE: SHOULDER CLOSURE — 4-LANE UNDIVIDED
MUTCD: TA-3
CDOT: S-630-1
ORIENTATION: Site bearing not provided

SCALE: 1" = 75 ft
DATE: 2026-08-22
SHEET: 1 OF 1

DRAWN BY: MHT Tool (auto-generated)
STATUS: DRAFT — Not for stamping