
METHOD OF HANDLING TRAFFIC · 30 MPH

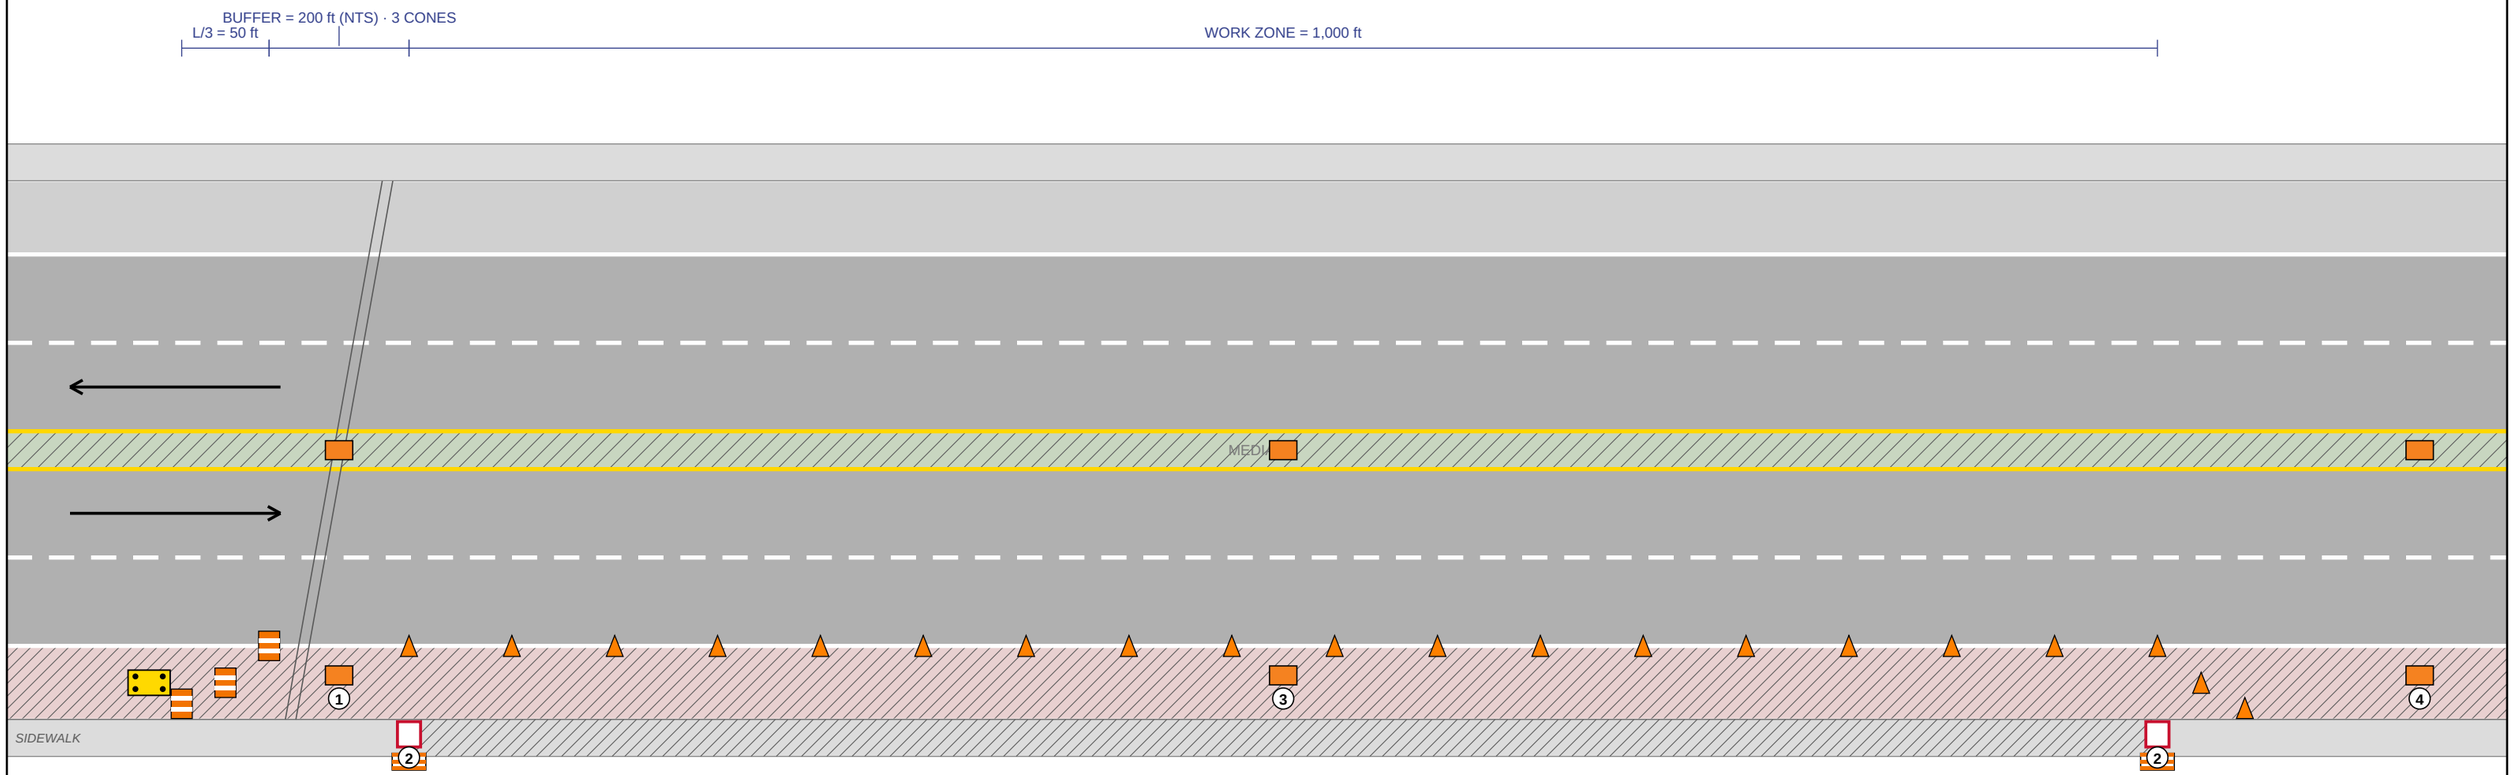

LEGEND

- Arrow Board (caution mode)
- Type III Barricade
- Traffic Cone (28-inch)
- Channelizing Drum

SIGN CATEGORIES

- Warning sign (W series, e.g. W20-1)
- Construction guide (G series, e.g. G20-2)
- Regulatory sign (R series, e.g. R9-9)

SITE CONTEXT

- Sidewalk (hatched within work zone = closed)

+1 MORE. SEE DEVICE LIST (XLSX)

Scale 1" = 87 ft applies to the work zone + taper. Buffer compressed; lateral offset exaggerated.

NOTES & SIGN SCHEDULE

PARAMETERS

Speed limit:	**30 mph**	Closure:	**Shoulder Closure**
Work zone:	**1,000 ft**	Shoulder width:	**10 ft (assumed)**
Shoulder taper (L/3):	**50 ft**	Buffer:	**200 ft**

SIGN SCHEDULE

#	CODE	DESCRIPTION
1	**G20-1**	ROAD CONSTRUCTION (NEXT 1000 FT)
2	**R9-9**	SIDEWALK CLOSED
3	**G20-5P**	CONSTRUCTION ZONE plaque
4	**G20-2**	END ROAD WORK

ADVANCE WARNING SIGNS (off-page upstream of taper)

CODE	DESCRIPTION	DISTANCE
W21-5aR	RIGHT SHOULDER CLOSED AHEAD	100 ft
W20-2	ROAD WORK 200 FT	200 ft
W20-1	ROAD WORK AHEAD	300 ft

TRAFFIC CONTROL DEVICE SUMMARY

MUTCD	DEVICE	QTY
G20-1	ROAD CONSTRUCTION (NEXT 1000 FT)	2
G20-2	END ROAD WORK	2
G20-5P	CONSTRUCTION ZONE plaque	2
R9-9	SIDEWALK CLOSED	2
W20-1	ROAD WORK AHEAD	2
W20-2	ROAD WORK 200 FT	2
W21-5aR	RIGHT SHOULDER CLOSED AHEAD	2
—	36-inch channelizing drum with alternating orange/white stripes	3
—	Traffic Cone (28-inch)	23
—	Type III barricade: three horizontal striped rails, full lane width	2
—	Trailer-mounted flashing arrow board (Type A, B, or C)	1
TOTAL DEVICES		**43**

SEE DEVICE LIST (XLSX) FOR BID QUANTITIES.

PROJECT:	Untitled Project
LOCATION:	—
COORDINATES:	39.73997, -104.96632
MHT TYPE:	SHOULDER CLOSURE · DIVIDED HIGHWAY
MUTCD:	TA-3
CDOT:	S-630-1
SCALE:	1" = 87 ft
DATE:	2026-10-17
SHEET:	1 OF 2
AERIAL:	See page 2
DRAWN BY:	MHT Tool (auto-generated)
STATUS:	**DRAFT: Not for stamping**


Reference: CDOT S-630-1, MUTCD 11th Edition Part 6, Colorado Supplement (effective January 18, 2026).

GENERATED BY CONESTRUCT. DRAFT FOR PE REVIEW. NOT A SEALED PLAN.

Verify all dimensions before use.

METHOD OF HANDLING TRAFFIC · 30 MPH

AERIAL CONTEXT

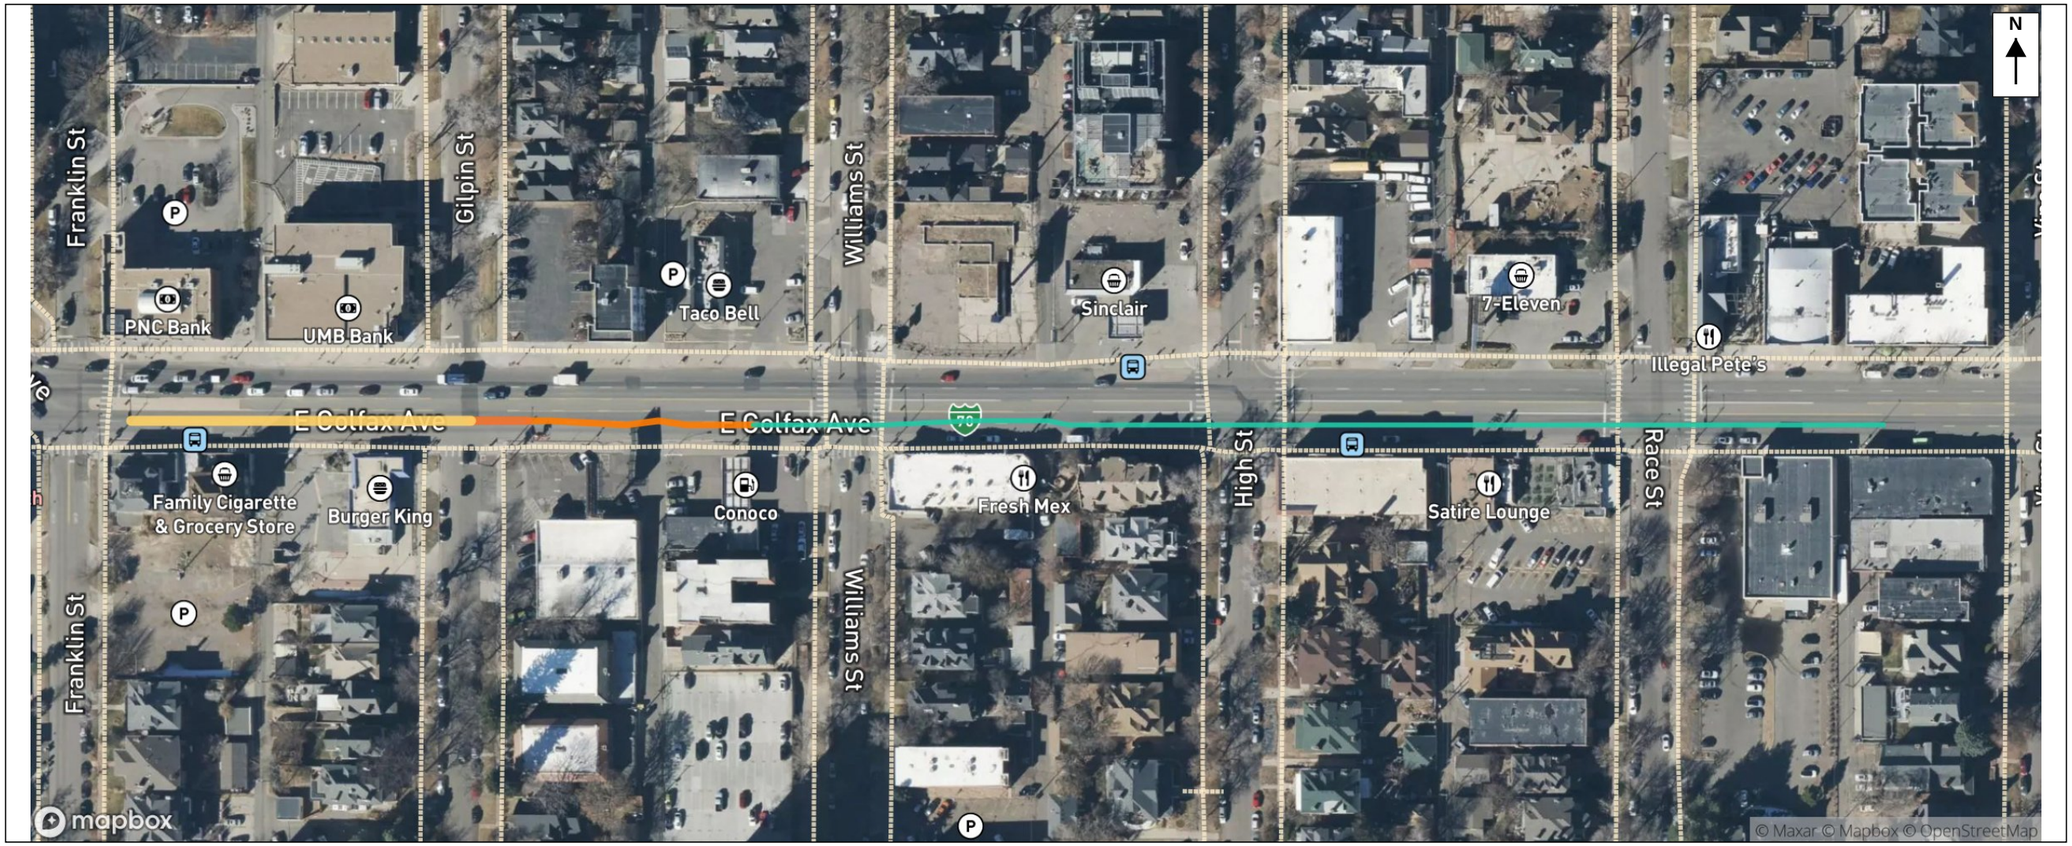

SITE: 39.73997, -104.96632

Advance warning · Taper · Buffer · Work zone · Downstream · faded: past the mapped road

Mapbox satellite imagery with street labels, for context only. Not a survey product. Verify all field conditions on site.

CORRIDOR DETAILS

Work starts:	39.73997, -104.96632
Direction of travel:	90°
Total corridor:	1,600 ft (0.30 mi)
Advance warning:	300 ft
Taper:	50 ft
Buffer:	200 ft
Work zone:	1,000 ft
Downstream:	50 ft
Centerline:	OSM, full corridor