


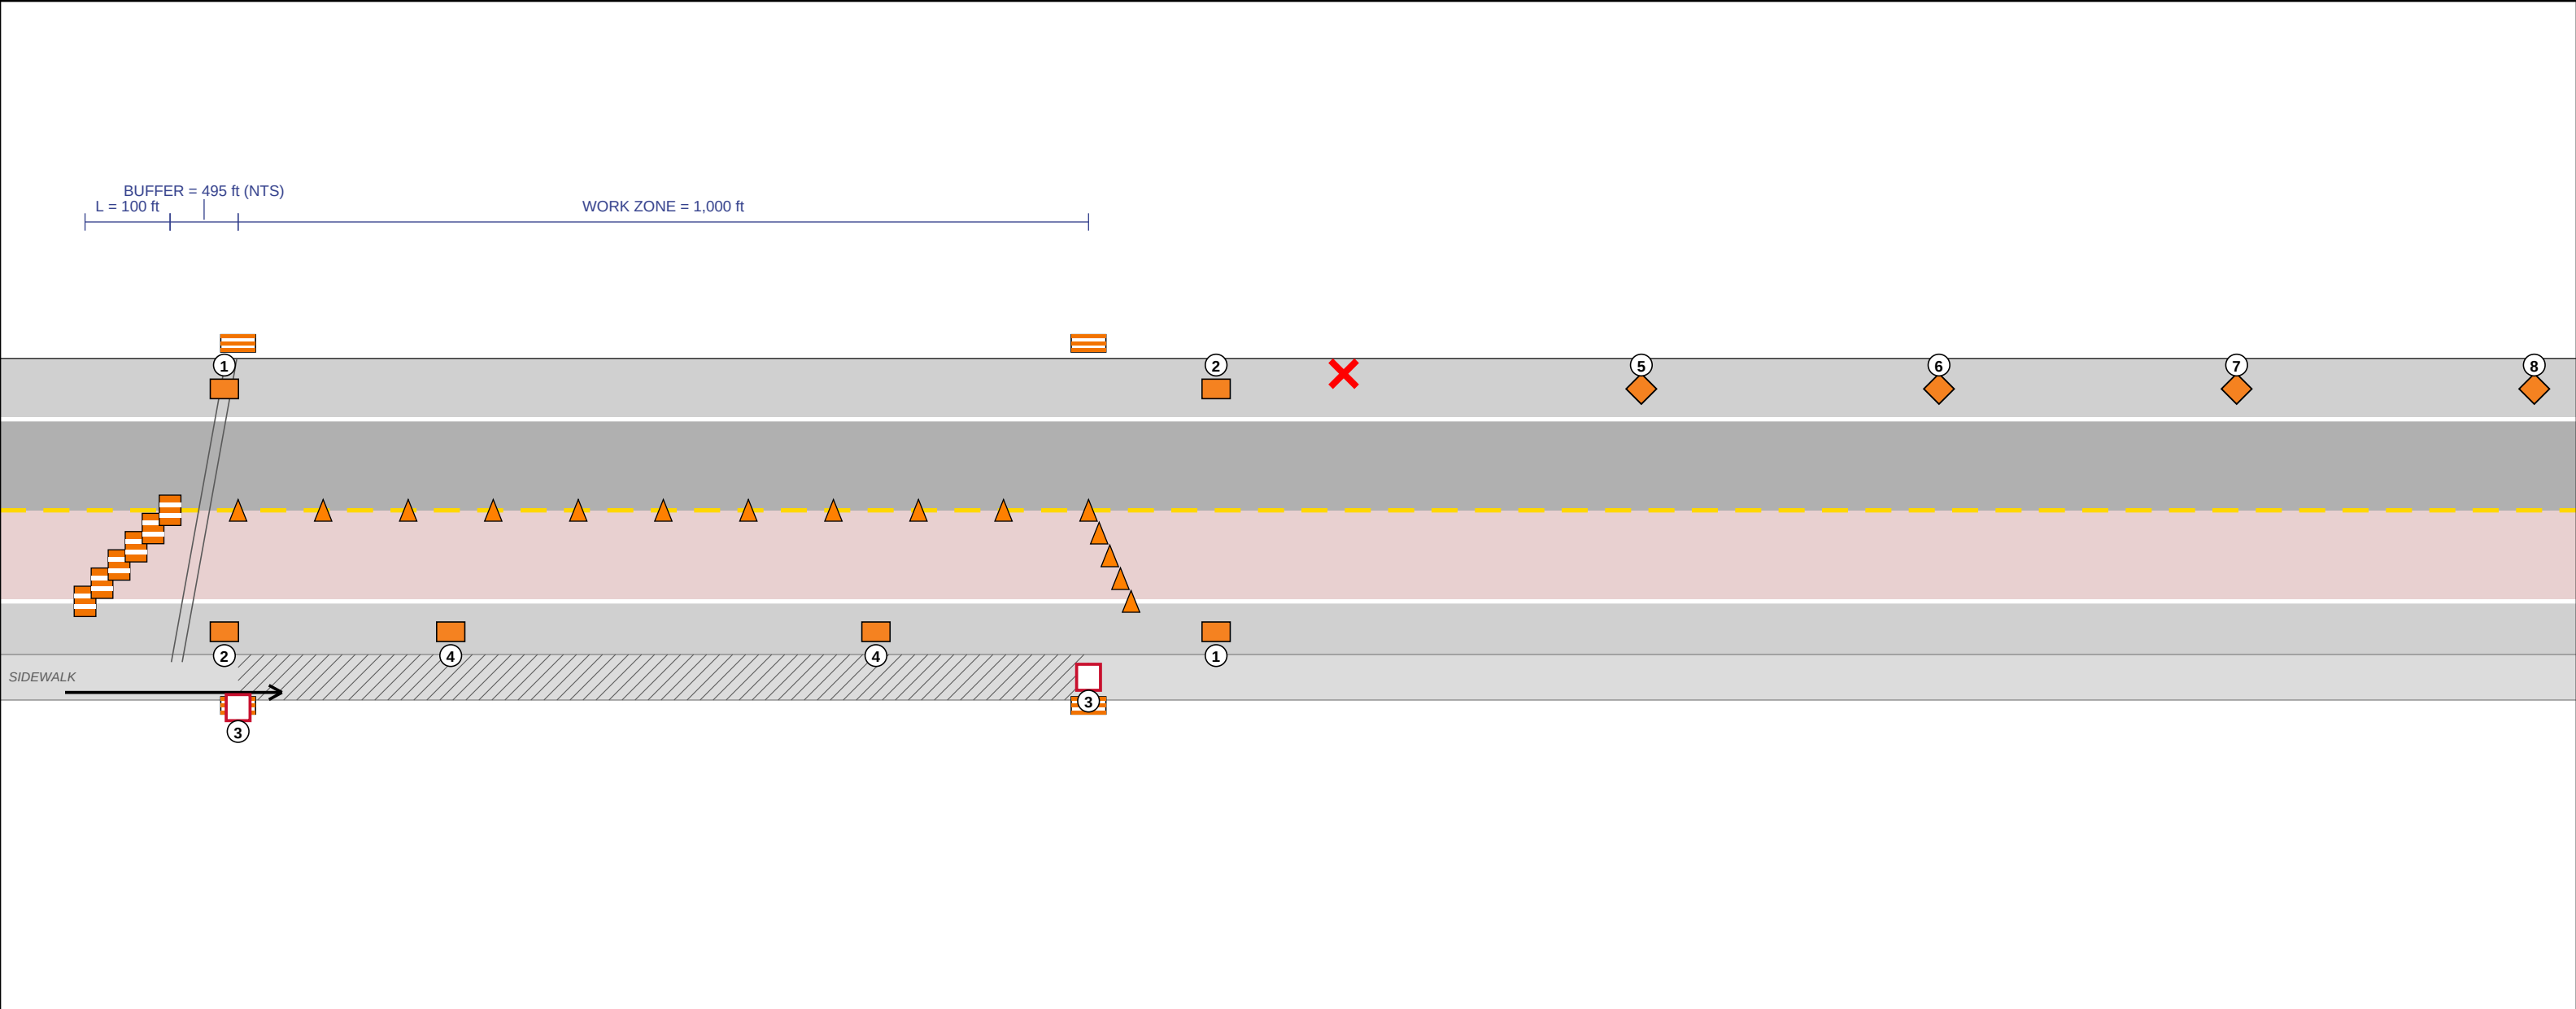

LEGEND

- Type III Barricade
- Traffic Cone (36-inch)
- Channelizing Drum
- Flagger Station

SIGN CATEGORIES

- Warning sign (W series, e.g. W20-1)
- Construction guide (G series, e.g. G20-2)
- Regulatory sign (R series, e.g. R9-9)

SITE CONTEXT

- Sidewalk (hatched within work zone = closed)

Scale 1" = 184 ft applies to the work zone + taper. Buffer compressed; lateral offset exaggerated.

NOTES & SIGN SCHEDULE

PARAMETERS			
Speed limit:	55 mph	Closure:	Flagger Alternating Traffic
Work zone:	1,000 ft	One-lane two-way taper:	100 ft
Buffer:	495 ft		

SIGN SCHEDULE		
#	CODE	DESCRIPTION
1	G20-2	END ROAD WORK
2	G20-1	ROAD CONSTRUCTION (NEXT 1000 FT)
3	R9-9	SIDEWALK CLOSED
4	G20-5P	CONSTRUCTION ZONE plaque
5	W20-7	FLAGGER AHEAD
6	W3-4	BE PREPARED TO STOP
7	W20-4	ONE LANE ROAD AHEAD
8	W20-1	ROAD WORK AHEAD

ADVANCE WARNING SIGNS & FLAGGER STATIONS (off-page upstream of taper)				
CODE	DESCRIPTION	DISTANCE	CODE	DESCRIPTION
—	FLAGGER STATION #1 (APPROACH)	100 ft	W20-4	ONE LANE ROAD AHEAD
W20-7	FLAGGER AHEAD	450 ft	W20-1	ROAD WORK AHEAD
W3-4	BE PREPARED TO STOP	800 ft		

Reference: CDOT S-630-1, MUTCD 11th Ed. Part 6 (effective 2026-01-18), Colorado Supplement.
GENERATED BY CONESTRUCT — DRAFT FOR PE REVIEW. NOT A SEALED PLAN.
Verify all dimensions before use.

TRAFFIC CONTROL DEVICE SUMMARY

MUTCD	DEVICE	QTY
G20-1	ROAD CONSTRUCTION (NEXT 1000 FT)	2
G20-2	END ROAD WORK	2
G20-5P	CONSTRUCTION ZONE plaque	2
R9-9	SIDEWALK CLOSED	2
W20-1	ROAD WORK AHEAD	2
W20-4	ONE LANE ROAD AHEAD	2
W20-7	FLAGGER AHEAD	2
W3-4	BE PREPARED TO STOP	2
—	36-inch channelizing drum with alternating orange/white stripes	6
—	Traffic Cone (36-inch)	15
—	Type III barricade — three horizontal striped rails, full lane width	4
—	Flagger position with STOP/SLOW paddle and PPE	2

TOTAL DEVICES 43

SEE DEVICE LIST (XLSX) FOR BID QUANTITIES.

PROJECT:	Untitled Project
LOCATION:	—
COORDINATES:	39.74362, -104.97070
MHT TYPE:	FLAGGER ALTERNATING TRAFFIC — 2-LANE UNDIVIDED
MUTCD:	TA-10
CDOT:	S-630-1
SCALE:	1" = 184 ft
DATE:	2026-09-26
SHEET:	1 OF 1
DRAWN BY:	MHT Tool (auto-generated)
STATUS:	DRAFT — Not for stamping