# METHOD OF HANDLING TRAFFIC · Audit N12 · 45 MPH

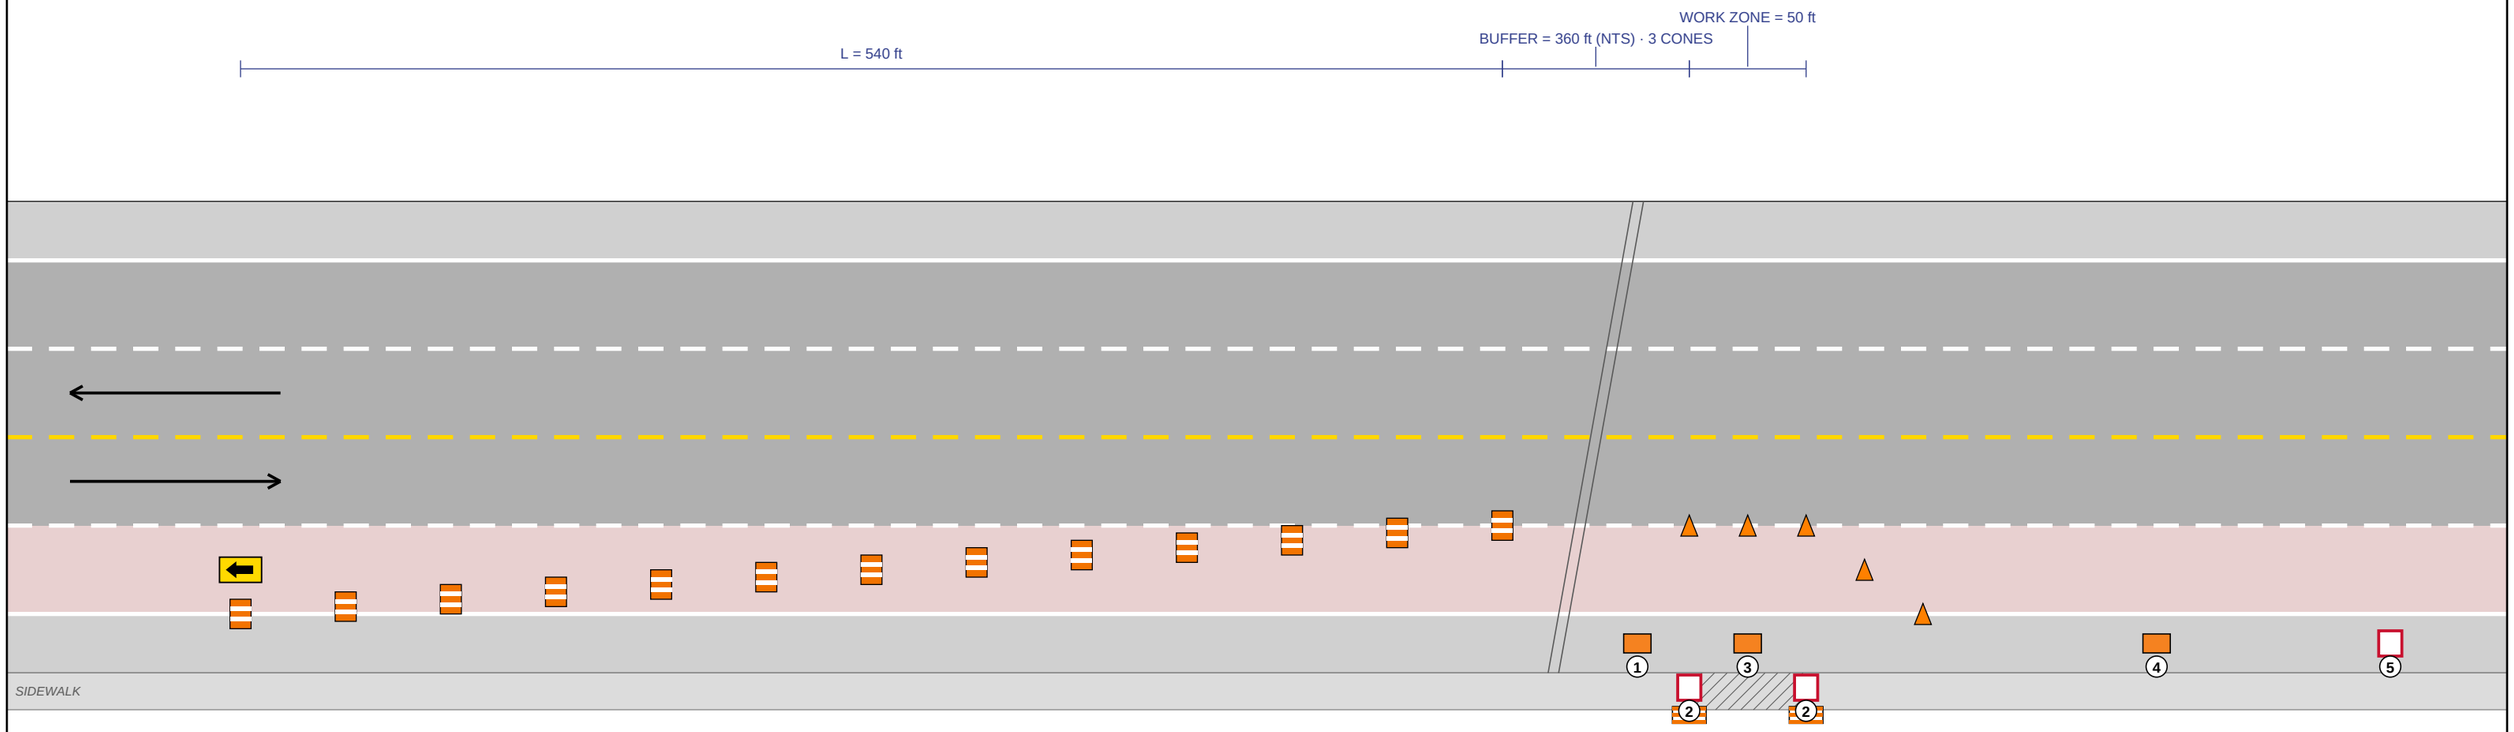


## LEGEND

- Arrow Board
- Type III Barricade
- Traffic Cone (36-inch)
- Channelizing Drum

### SIGN CATEGORIES

- Warning sign (W series, e.g. W20-1)
- Construction guide (G series, e.g. G20-2)
- Regulatory sign (R series, e.g. R9-9)

### SITE CONTEXT

- Sidewalk (hatched within work zone = closed)

*Scale 1" = 65 ft applies to the work zone + taper. Buffer compressed; lateral offset exaggerated.*

## NOTES & SIGN SCHEDULE

### PARAMETERS

| | | | |
|---|---|---|---|
| Speed limit: | **45 mph** | Closure: | **Lane Closure Near Intersection** |
| Work zone: | **50 ft** | Lane taper (L): | **540 ft** |
| Buffer: | **360 ft** | | |

### SIGN SCHEDULE

| # | CODE | DESCRIPTION |
|---|---|---|
| 1 | **G20-1** | ROAD CONSTRUCTION (NEXT 50 FT) |
| 2 | **R9-9** | SIDEWALK CLOSED |
| 3 | **G20-5P** | WORK ZONE plaque |
| 4 | **G20-2** | END ROAD WORK |
| 5 | **R2-11** | END DOUBLE FINES ZONE |

### ADVANCE WARNING SIGNS (off-page upstream of taper)

| CODE | DESCRIPTION | DISTANCE |
|---|---|---|
| **W4-2R** | RIGHT LANE ENDS | 350 ft |
| **W20-5R** | RIGHT LANE CLOSED AHEAD | 700 ft |

**+2 MORE ADVANCE SIGNS (R2-10, W20-1). SEE CREW NARRATIVE & DEVICE LIST**

**CROSS-STREET CONTROL PER CDOT S-630-1 SHEET 10, CASES 18/19: NOT DRAWN. PLATE DEPARTURES: SEE AUDIT. SEE DEVICE LIST, CREW NARRATIVE, AND AUDIT.**
**CLOSED LANE DRAWN AS THE RIGHTMOST LANE: A MODELING ASSUMPTION; NO MUTCD RULE SELECTS THE LANE (THE WORK LOCATION DOES). IF THE WORK OCCUPIES A DIFFERENT LANE, THIS PLAN DOES NOT APPLY AS DRAWN.**

## TRAFFIC CONTROL DEVICE SUMMARY

| MUTCD | DEVICE | QTY |
|---|---|---|
| G20-1 | ROAD CONSTRUCTION (NEXT 50 FT) | 1 |
| G20-2 | END ROAD WORK | 1 |
| G20-5P | WORK ZONE plaque | 1 |
| R2-10 | BEGIN DOUBLE FINES ZONE | 3 |
| R2-11 | END DOUBLE FINES ZONE | 3 |
| R9-9 | SIDEWALK CLOSED | 2 |
| W20-1 | ROAD WORK AHEAD | 3 |
| W20-5R | RIGHT LANE CLOSED AHEAD | 1 |
| W4-2R | RIGHT LANE ENDS | 1 |
| — | 36-inch channelizing drum with alternating orange/white stripes | 13 |
| — | Traffic Cone (36-inch) | 8 |
| — | Type III barricade: three horizontal striped rails, full lane width | 2 |
| — | Trailer-mounted flashing arrow board (Type A, B, or C) | 1 |
| **TOTAL DEVICES** | | **40** |

*SEE DEVICE LIST (XLSX) FOR BID QUANTITIES.*

| | |
|---|---|
| PROJECT: | Audit N12 |
| LOCATION: | — |
| COORDINATES: | 39.74014, -105.13434 |
| MHT TYPE: | LANE CLOSURE NEAR INTERSECTION · UNDIVIDED |
| MUTCD: | TA-21 |
| CDOT: | S-630-1 |
| SCALE: | 1" = 65 ft |
| DATE: | 2026-10-24 |
| SHEET: | 1 OF 1 |
| DRAWN BY: | MHT Tool (auto-generated) |
| STATUS: | **DRAFT: Not for stamping** |

*Reference: CDOT S-630-1, MUTCD 11th Edition Part 6, Colorado Supplement (effective January 18, 2026).*
**GENERATED BY CONESTRUCT. DRAFT FOR PE REVIEW. NOT A SEALED PLAN.**
*Verify all dimensions before use.*