METHOD OF HANDLING TRAFFIC · Audit N14 · 55 MPH

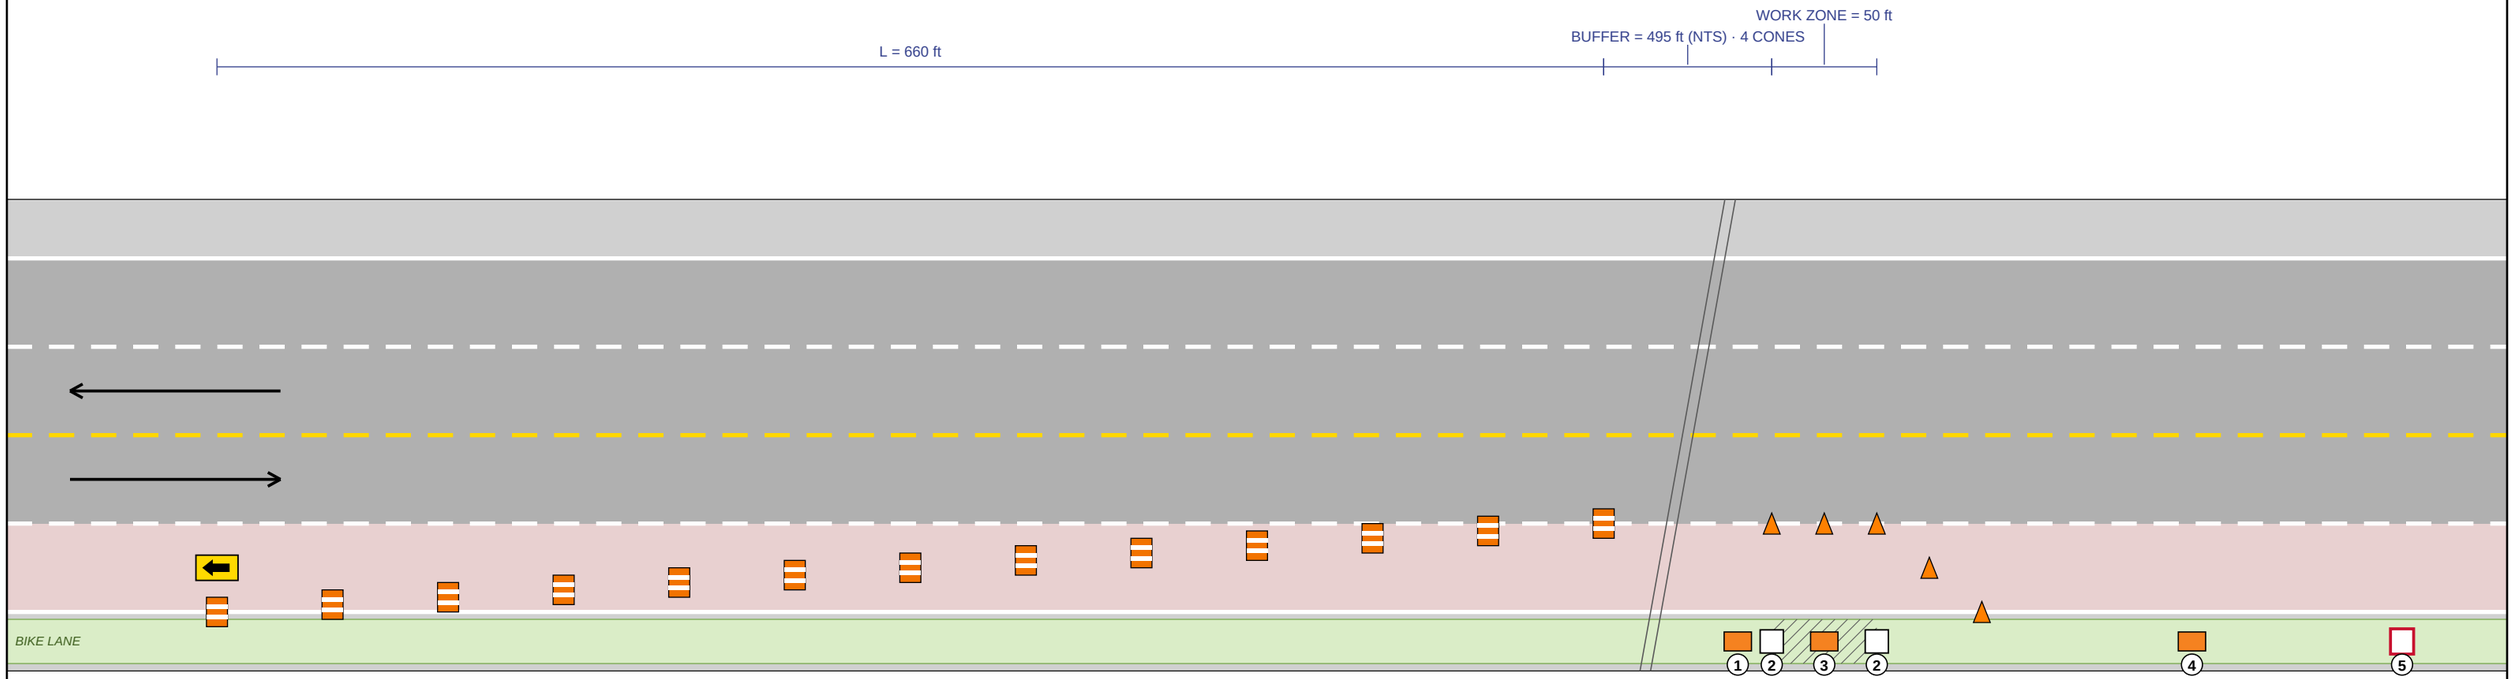

LEGEND

- Arrow Board
- Traffic Cone (36-inch)
- Channelizing Drum

SIGN CATEGORIES

- Warning sign (W series, e.g. W20-1)
- Construction guide (G series, e.g. G20-2)
- Regulatory sign (R series, e.g. R9-9)
- Route guidance (M series, e.g. M4-9a)

SITE CONTEXT

- Bike lane (hatched within work zone = closed)

Scale 1" = 72 ft applies to the work zone + taper. Buffer compressed; lateral offset exaggerated.

NOTES & SIGN SCHEDULE

PARAMETERS

Speed limit:	**55 mph**	Closure:	**Lane Closure Near Intersection**
Work zone:	**50 ft**	Lane taper (L):	**660 ft**
Buffer:	**495 ft**		

SIGN SCHEDULE

#	CODE	DESCRIPTION
1	**G20-1**	ROAD CONSTRUCTION (NEXT 50 FT)
2	**M4-9a**	BIKE DETOUR
3	**G20-5P**	WORK ZONE plaque
4	**G20-2**	END ROAD WORK
5	**R2-11**	END DOUBLE FINES ZONE

ADVANCE WARNING SIGNS (off-page upstream of taper)

CODE	DESCRIPTION	DISTANCE
W4-2R	RIGHT LANE ENDS	350 ft
W20-5R	RIGHT LANE CLOSED AHEAD	700 ft

+2 MORE ADVANCE SIGNS (R2-10, W20-1). SEE CREW NARRATIVE & DEVICE LIST

CROSS-STREET CONTROL PER CDOT S-630-1 SHEET 10, CASES 18/19: NOT DRAWN. PLATE DEPARTURES: SEE AUDIT. SEE DEVICE LIST, CREW NARRATIVE, AND AUDIT.
CLOSED LANE DRAWN AS THE RIGHTMOST LANE: A MODELING ASSUMPTION; NO MUTCD RULE SELECTS THE LANE (THE WORK LOCATION DOES). IF THE WORK OCCUPIES A DIFFERENT LANE, THIS PLAN DOES NOT APPLY AS DRAWN.

TRAFFIC CONTROL DEVICE SUMMARY

MUTCD	DEVICE	QTY
G20-1	ROAD CONSTRUCTION (NEXT 50 FT)	1
G20-2	END ROAD WORK	1
G20-5P	WORK ZONE plaque	1
M4-9a	BIKE DETOUR	2
R2-10	BEGIN DOUBLE FINES ZONE	2
R2-11	END DOUBLE FINES ZONE	2
W20-1	ROAD WORK AHEAD	2
W20-5R	RIGHT LANE CLOSED AHEAD	1
W4-2R	RIGHT LANE ENDS	1
—	36-inch channelizing drum with alternating orange/white stripes	13
—	Traffic Cone (36-inch)	9
—	Trailer-mounted flashing arrow board (Type A, B, or C)	1
TOTAL DEVICES		**36**

SEE DEVICE LIST (XLSX) FOR BID QUANTITIES.

PROJECT:	Audit N14
LOCATION:	—
COORDINATES:	39.88688, -104.84575
MHT TYPE:	LANE CLOSURE NEAR INTERSECTION · UNDIVIDED
MUTCD:	TA-21
CDOT:	S-630-1
SCALE:	1" = 72 ft
DATE:	2026-10-24
SHEET:	1 OF 1
DRAWN BY:	MHT Tool (auto-generated)
STATUS:	**DRAFT: Not for stamping**

Reference: CDOT S-630-1, MUTCD 11th Edition Part 6, Colorado Supplement (effective January 18, 2026).
GENERATED BY CONESTRUCT. DRAFT FOR PE REVIEW. NOT A SEALED PLAN.
Verify all dimensions before use.