METHOD OF HANDLING TRAFFIC · Spec4 Test · 55 MPH

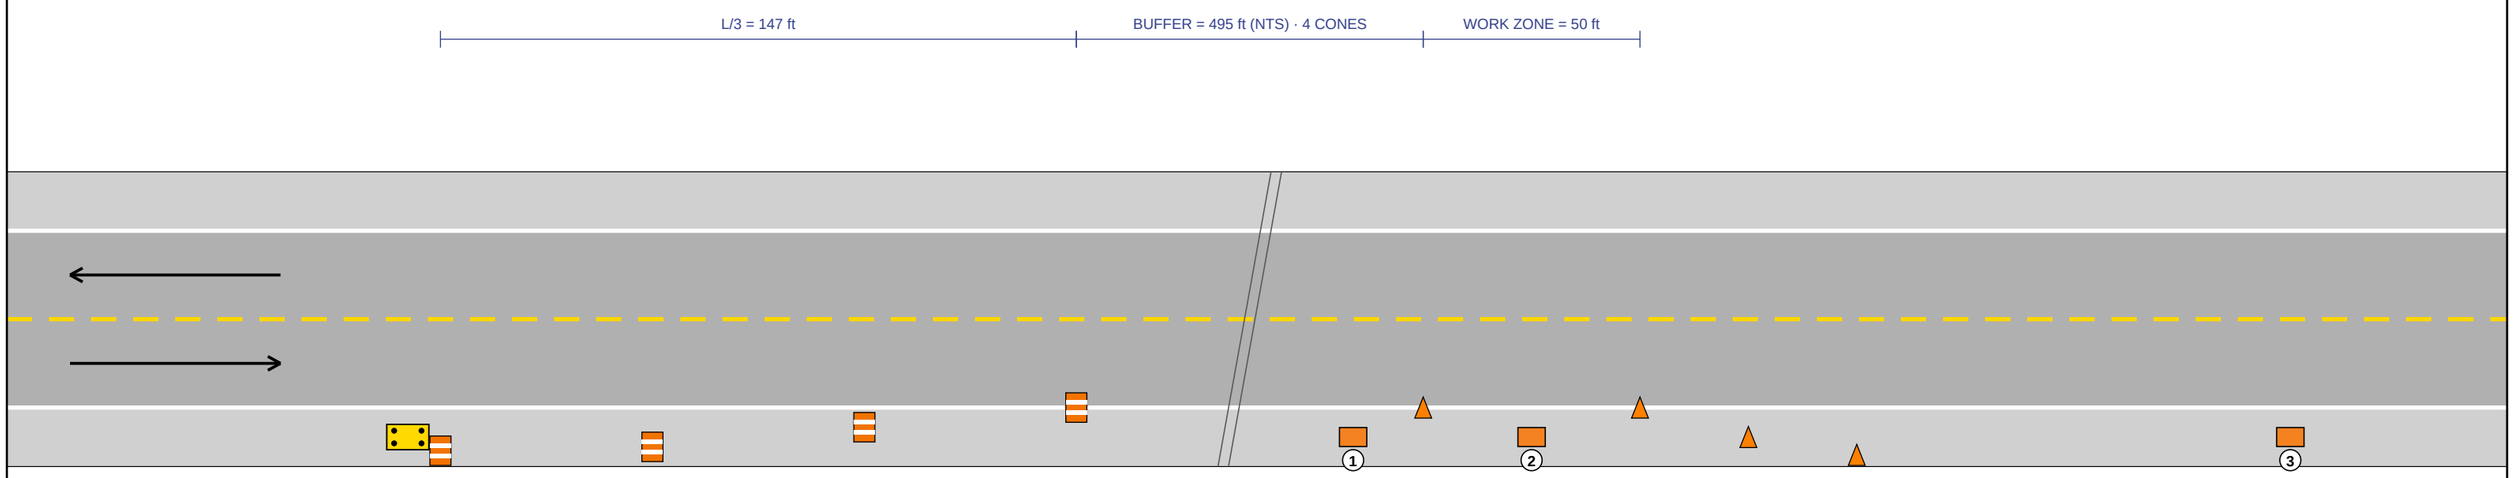

LEGEND

- Arrow Board (caution mode)
- Traffic Cone (36-inch)
- Channelizing Drum

SIGN CATEGORIES

- Warning sign (W series, e.g. W20-1)
- Construction guide (G series, e.g. G20-2)

Scale 1" = 35 ft applies to the work zone + taper. Buffer compressed; lateral offset exaggerated.

NOTES & SIGN SCHEDULE

PARAMETERS

Speed limit:	**55 mph**	Closure:	**Shoulder Closure**
Work zone:	**50 ft**	Shoulder width:	**8 ft (assumed)**
Shoulder taper (L/3):	**147 ft**	Buffer:	**495 ft**

SIGN SCHEDULE

#	CODE	DESCRIPTION
1	**G20-1**	ROAD CONSTRUCTION (NEXT 50 FT)
2	**G20-5P**	WORK ZONE plaque
3	**G20-2**	END ROAD WORK

ADVANCE WARNING SIGNS (off-page upstream of taper)

CODE	DESCRIPTION	DISTANCE
W21-5aR	RIGHT SHOULDER CLOSED AHEAD	500 ft
W20-2	ROAD WORK 1000 FT	1000 ft
W20-1	ROAD WORK AHEAD	1500 ft

TRAFFIC CONTROL DEVICE SUMMARY

MUTCD	DEVICE	QTY
G20-1	ROAD CONSTRUCTION (NEXT 50 FT)	1
G20-2	END ROAD WORK	1
G20-5P	WORK ZONE plaque	1
W20-1	ROAD WORK AHEAD	1
W20-2	ROAD WORK 1000 FT	1
W21-5aR	RIGHT SHOULDER CLOSED AHEAD	1
—	36-inch channelizing drum with alternating orange/white stripes	4
—	Traffic Cone (36-inch)	8
—	Trailer-mounted flashing arrow board (Type A, B, or C)	1
TOTAL DEVICES		**19**

SEE DEVICE LIST (XLSX) FOR BID QUANTITIES.

PROJECT:	Spec4 Test
LOCATION:	—
COORDINATES:	—
MHT TYPE:	SHOULDER CLOSURE · 2-LANE UNDIVIDED
MUTCD:	TA-3
CDOT:	S-630-1
ORIENTATION:	*Site bearing not provided*
SCALE:	1" = 35 ft
DATE:	2026-10-24
SHEET:	1 OF 1
DRAWN BY:	MHT Tool (auto-generated)
STATUS:	**DRAFT: Not for stamping**

Reference: CDOT S-630-1, MUTCD 11th Edition Part 6, Colorado Supplement (effective January 18, 2026).

GENERATED BY CONESTRUCT. DRAFT FOR PE REVIEW. NOT A SEALED PLAN.

Verify all dimensions before use.