


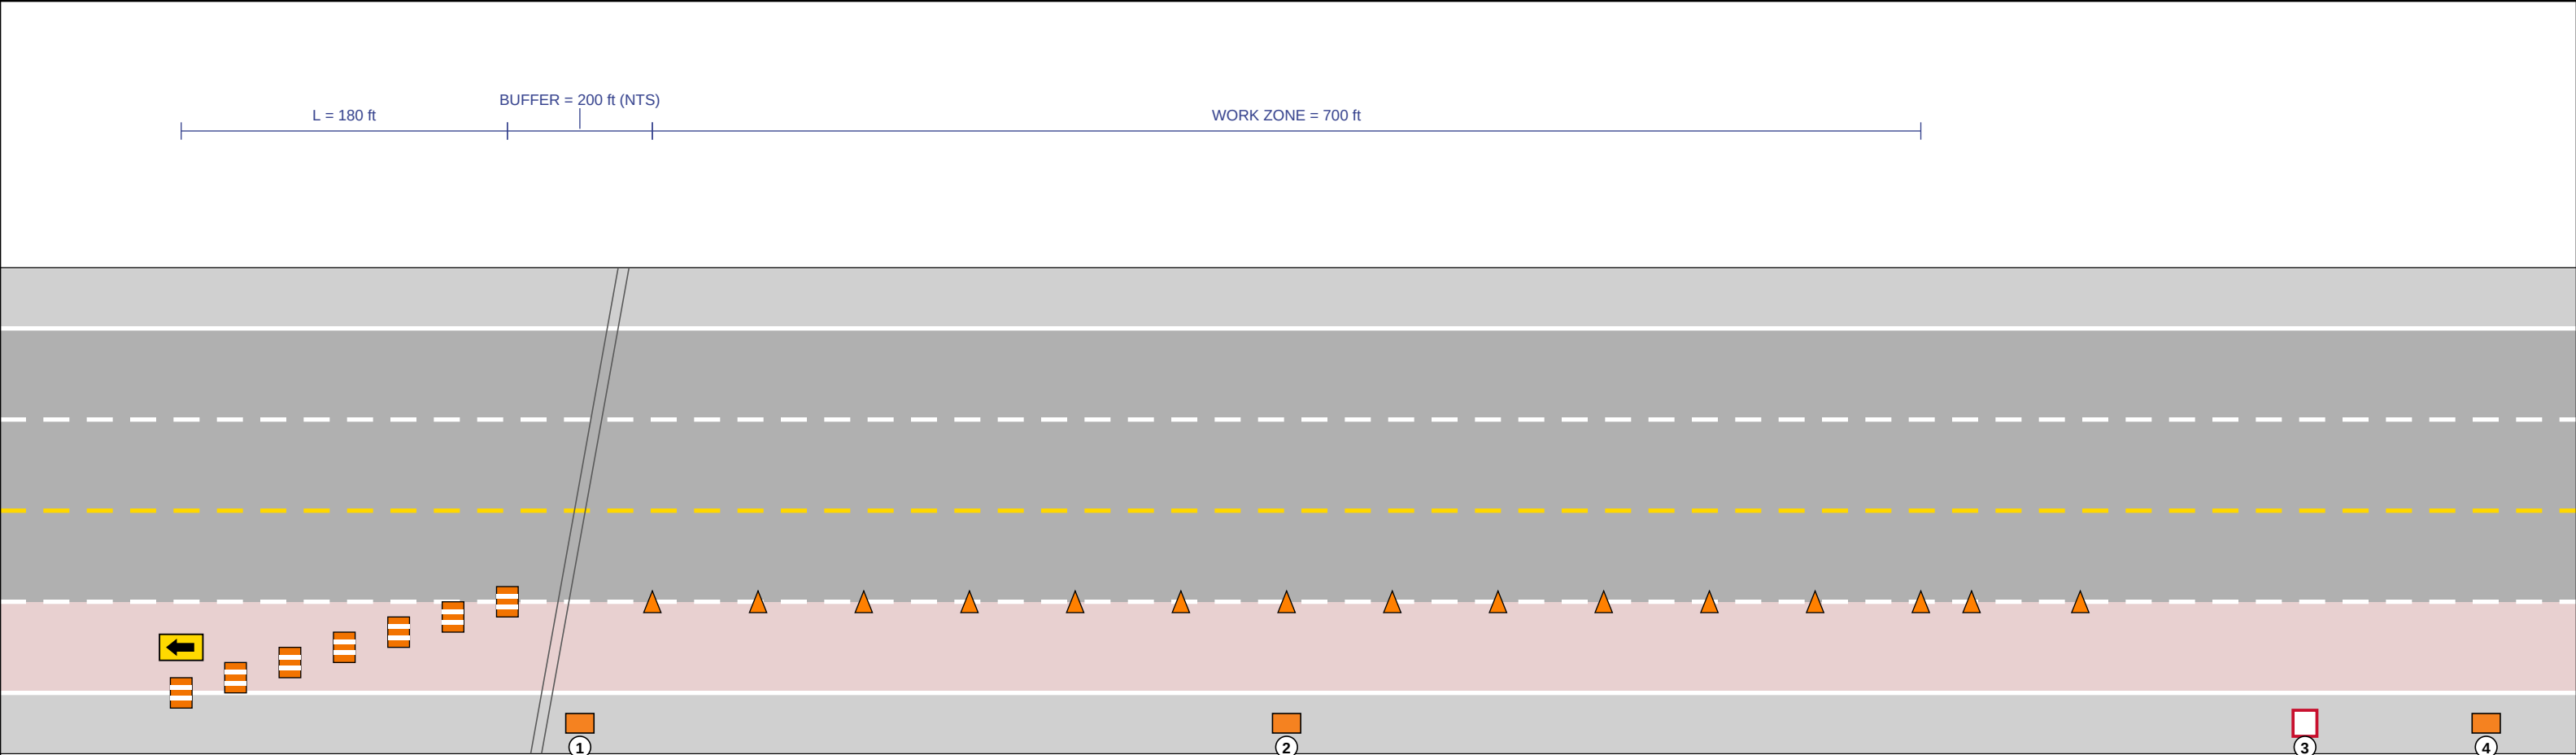

LEGEND

- Arrow Board
- Traffic Cone (28-inch)
- Channelizing Drum
- Warning sign (W series, e.g. W20-1)
- Construction guide (G series, e.g. G20-2)
- Regulatory sign (R series, e.g. R9-9)

Scale 1" = 86 ft applies to the work zone + taper. Buffer compressed; lateral offset exaggerated.

NOTES & SIGN SCHEDULE

PARAMETERS			
Speed limit:	30 mph	Closure:	Lane Closure Near Intersection
Work zone:	700 ft	Lane taper (L):	180 ft
Buffer:	200 ft		

SIGN SCHEDULE		
#	CODE	DESCRIPTION
1	G20-1	ROAD CONSTRUCTION (NEXT 700 FT)
2	G20-5P	CONSTRUCTION ZONE plaque
3	R2-11	END DOUBLE FINES ZONE
4	G20-2	END ROAD WORK

ADVANCE WARNING SIGNS (off-page upstream of taper)					
CODE	DESCRIPTION	DISTANCE	CODE	DESCRIPTION	DISTANCE
W4-2R	RIGHT LANE ENDS	100 ft	R2-10	BEGIN DOUBLE FINES ZONE	250 ft
W20-5R	RIGHT LANE CLOSED AHEAD	200 ft	W20-1	ROAD WORK AHEAD	300 ft

Reference: CDOT S-630-1, MUTCD 11th Ed. Part 6 (effective 2026-01-18), Colorado Supplement.
CROSS-STREET CONTROL PER CDOT S-630-1 SHEET 10, CASES 18/19 — NOT DRAWN. SEE DEVICE LIST, CREW NARRATIVE, AND AUDIT.
Plate typifies corner-quadrant work with a cross-street closure train; this plan places advance sets only (corner work tracked at issue #128).
Opposing mainline direction not signed (undivided single-side convention; the plate signs both directions).
Plate typifies rural sign placement; urban applications require block-based placement (Sheet 10 Note 1).
CLOSED LANE DRAWN AS THE RIGHTMOST LANE — MODELING ASSUMPTION; NO MUTCD RULE SELECTS THE LANE (THE WORK LOCATION DOES). IF THE WORK OCCUPIES A DIFFERENT LANE, THIS PLAN DOES NOT APPLY AS DRAWN.
GENERATED BY CONESTRUCT — DRAFT FOR PE REVIEW. NOT A SEALED PLAN.
Verify all dimensions before use.

TRAFFIC CONTROL DEVICE SUMMARY

MUTCD	DEVICE	QTY
G20-1	ROAD CONSTRUCTION (NEXT 700 FT)	1
G20-2	END ROAD WORK	1
G20-5P	CONSTRUCTION ZONE plaque	1
R2-10	BEGIN DOUBLE FINES ZONE	1
R2-11	END DOUBLE FINES ZONE	1
W20-1	ROAD WORK AHEAD	1
W20-5R	RIGHT LANE CLOSED AHEAD	1
W4-2R	RIGHT LANE ENDS	1
—	36-inch channelizing drum with alternating orange/white stripes	7
—	Traffic Cone (28-inch)	15
—	Trailer-mounted flashing arrow board (Type A, B, or C)	1


TOTAL DEVICES 31

SEE DEVICE LIST (XLSX) FOR BID QUANTITIES.

PROJECT:	Untitled Project
LOCATION:	—
COORDINATES:	39.73978, -104.96348
MHT TYPE:	LANE CLOSURE NEAR INTERSECTION — UNDIVIDED
MUTCD:	TA-21
CDOT:	S-630-1
SCALE:	1" = 86 ft
DATE:	2026-08-04
SHEET:	1 OF 2
AERIAL:	See page 2

DRAWN BY: MHT Tool (auto-generated)
STATUS: DRAFT — Not for stamping

AERIAL CONTEXT

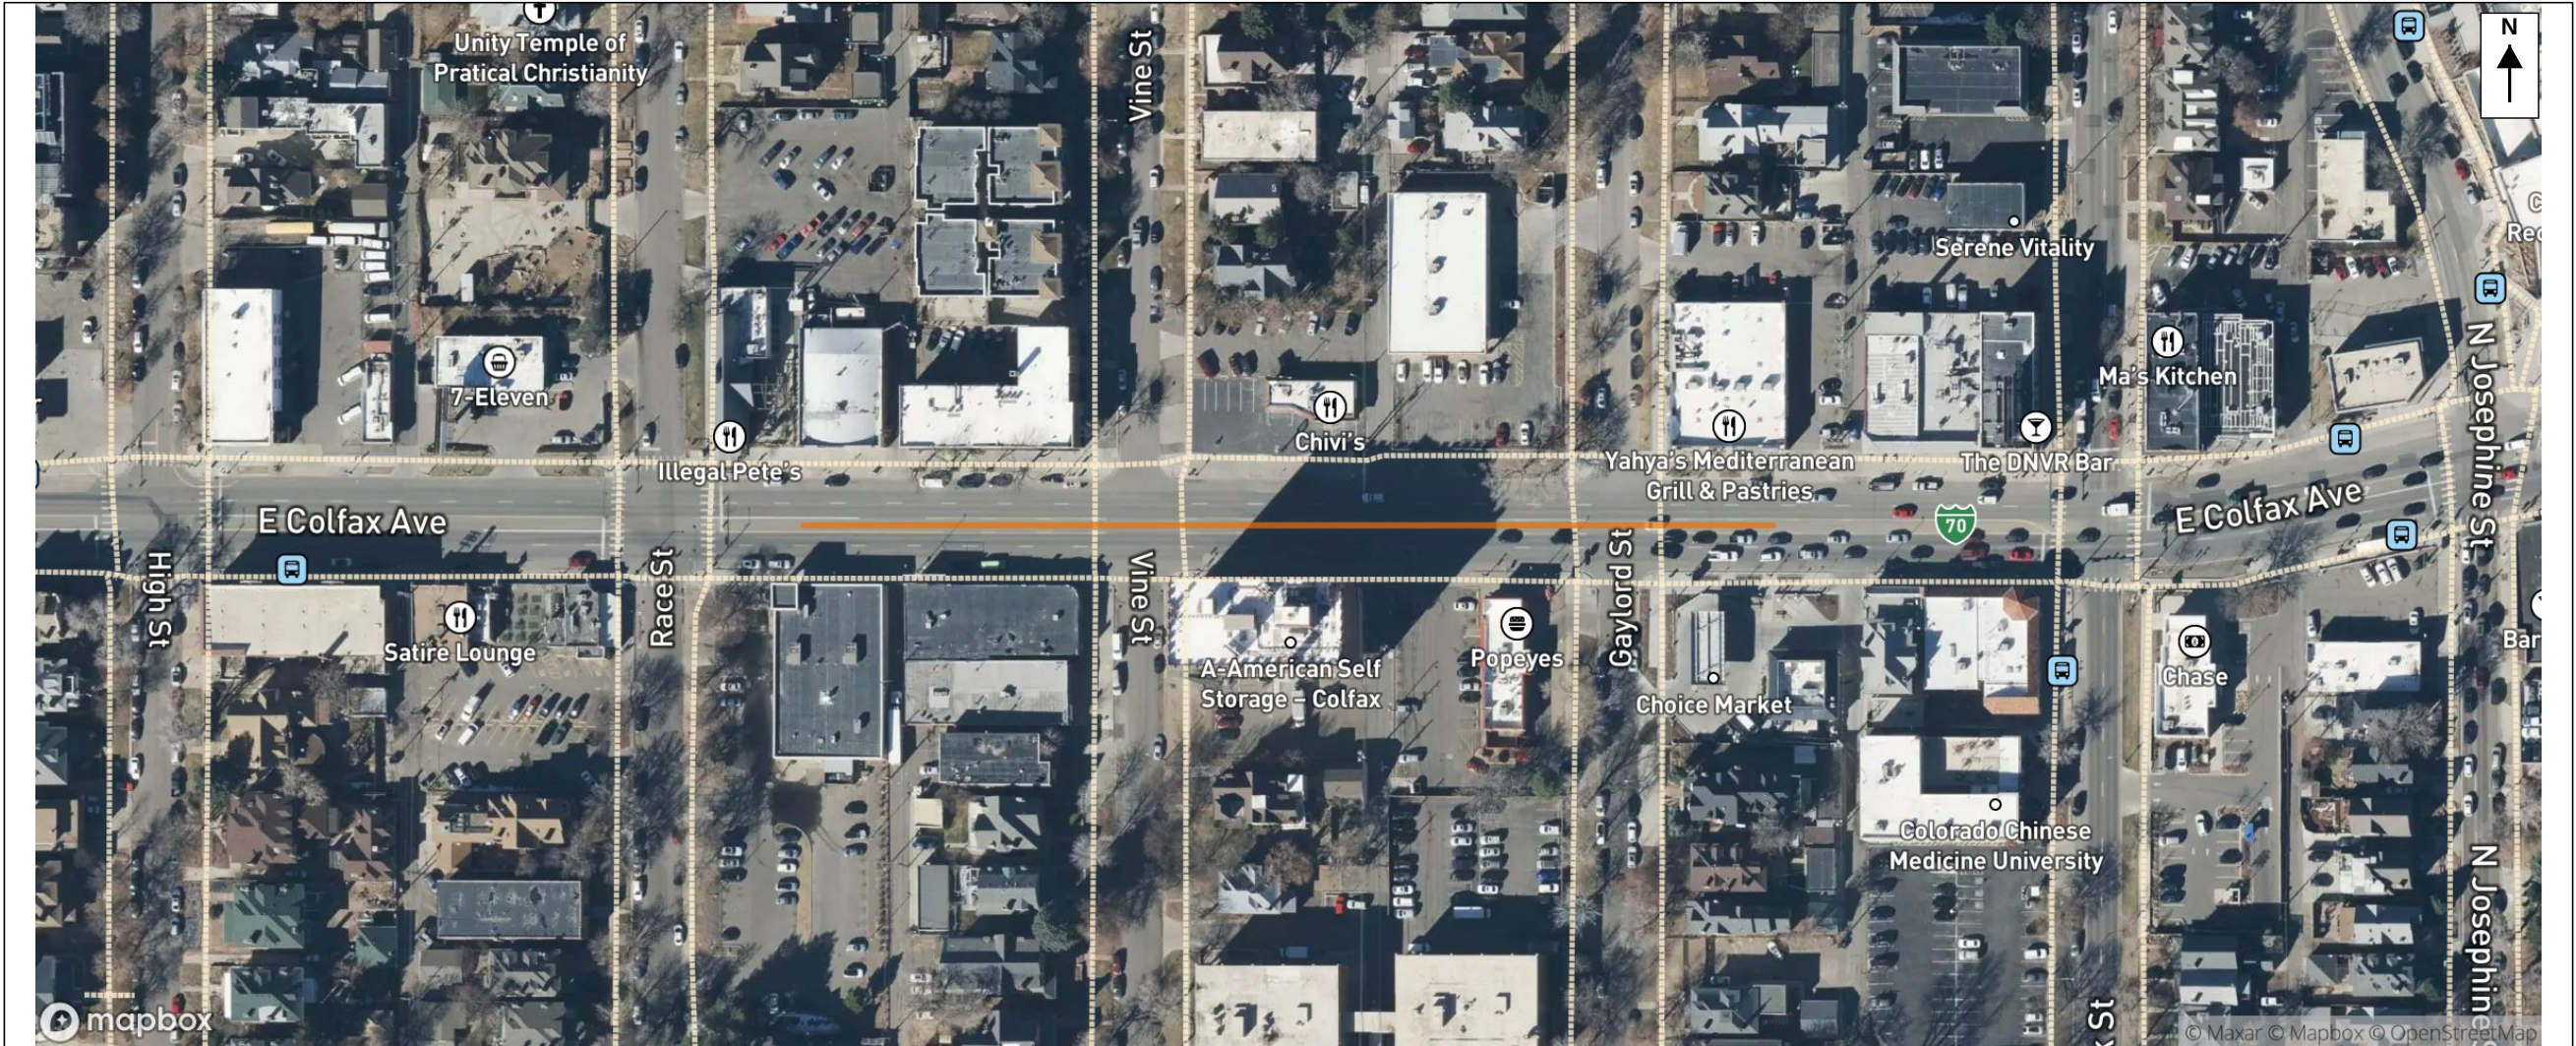

SITE: 39.73978, -104.96348

Work zone (700 ft) shown in orange. Advance warning, taper, and buffer not depicted. Mapbox satellite imagery with street labels — for context only. Not a survey product. Verify all field conditions on site.

CORRIDOR DETAILS

Anchor:	39.73978, -104.96348
Bearing:	91°
Total corridor:	1,480 ft (0.28 mi)
Advance warning:	300 ft
Taper:	180 ft
Buffer:	200 ft
Work zone:	700 ft
Downstream:	100 ft
Centerline:	OSM, full corridor